



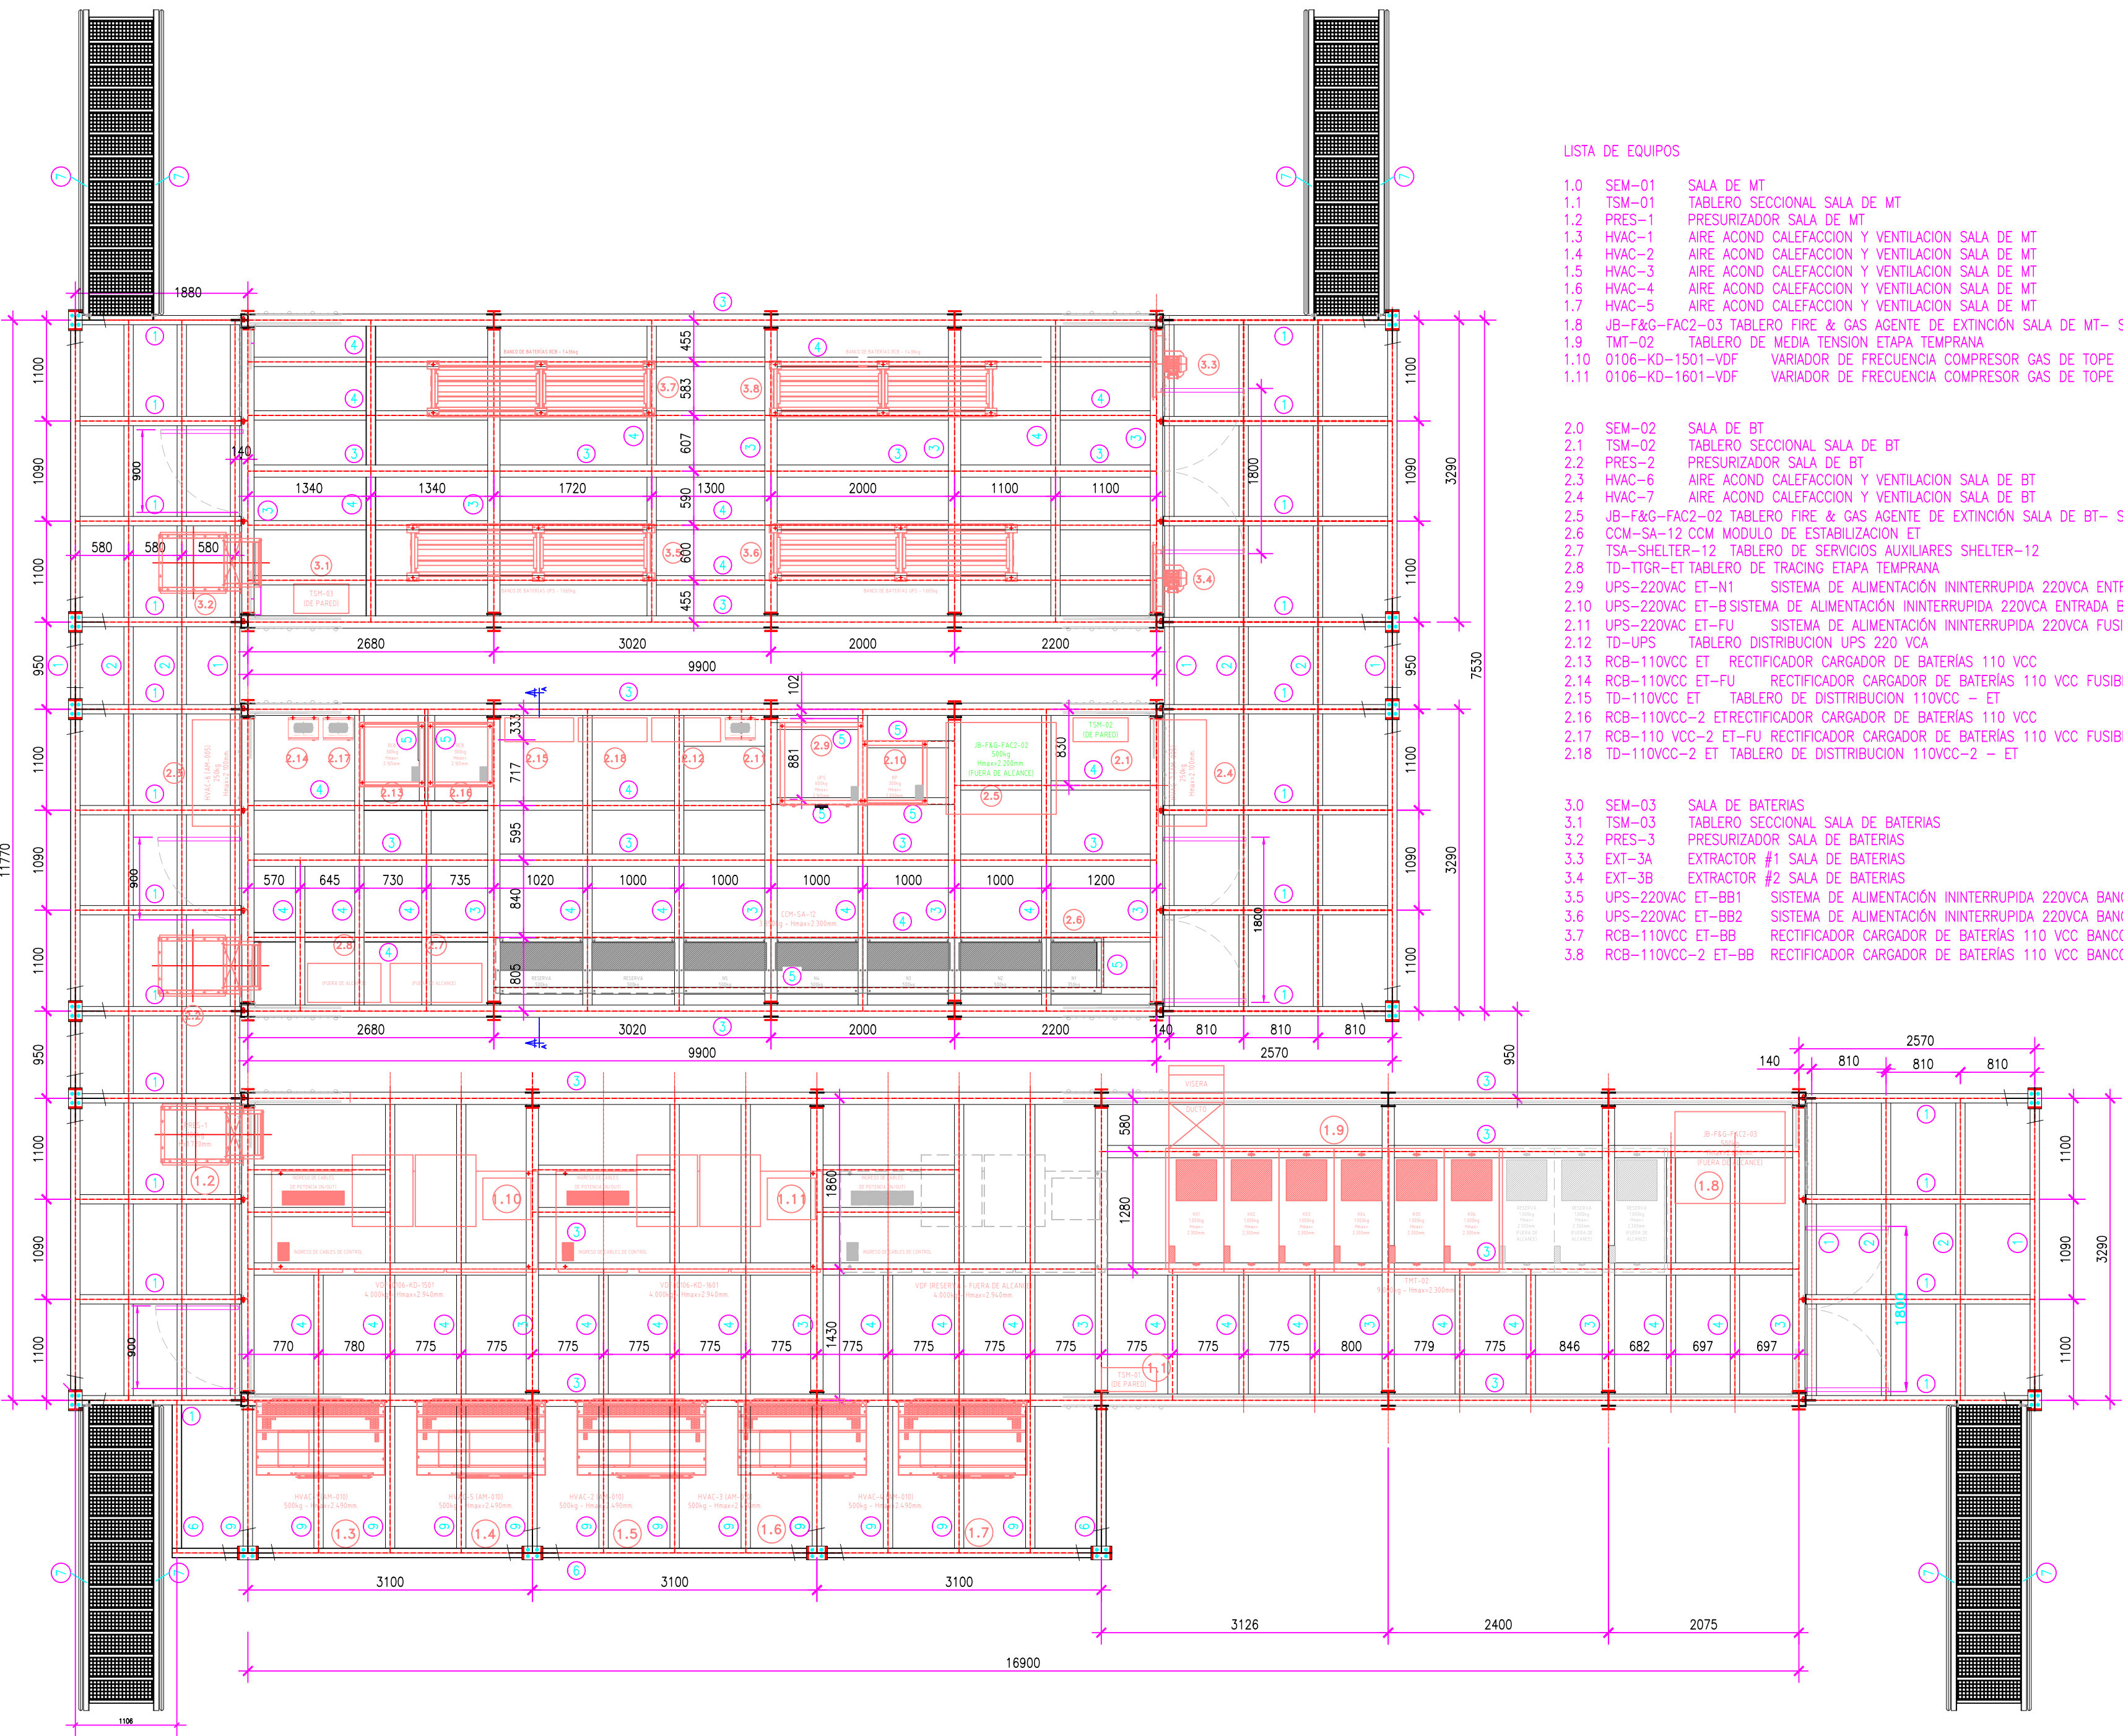


LAYOUT GENERAL SEM-01 / SEM-02 / SEM-03
ESCALA 1:50

LISTADO DE PERFILES			
POS	SECCIÓN	h [mm]	bf [mm]
1	W8x13	203	102
2	W6x9	148	100
3	W8x21	210	134
4	W6x12	153	102
5	L3"x1/4"	76.2	76.2
6	W8x15	206	102
7	UPN 140	140	60
8	W6x15	152	152
9	W6x16	160	102

ESQUEMA DETALLE CERRAMIENTO
ESCALA 1:50

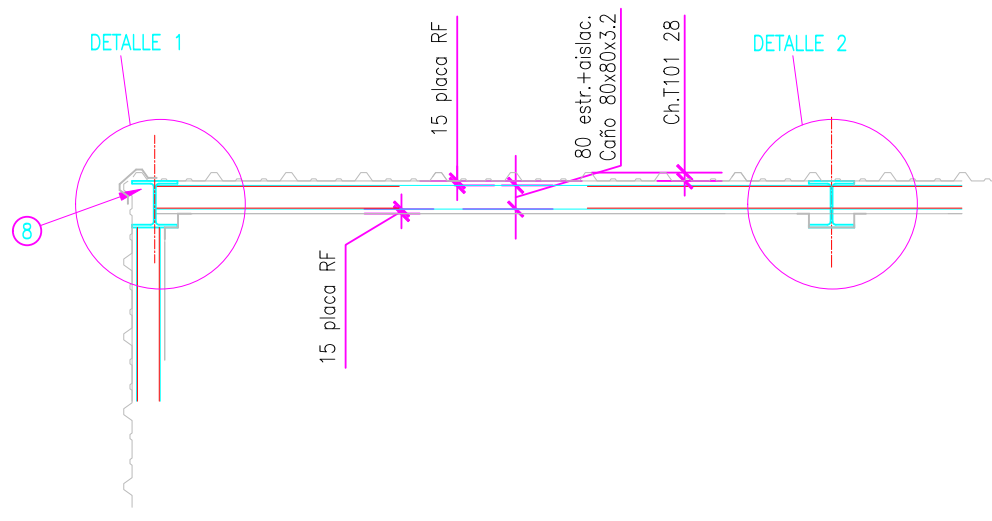


DETALLE 1
ESCALA 1:10

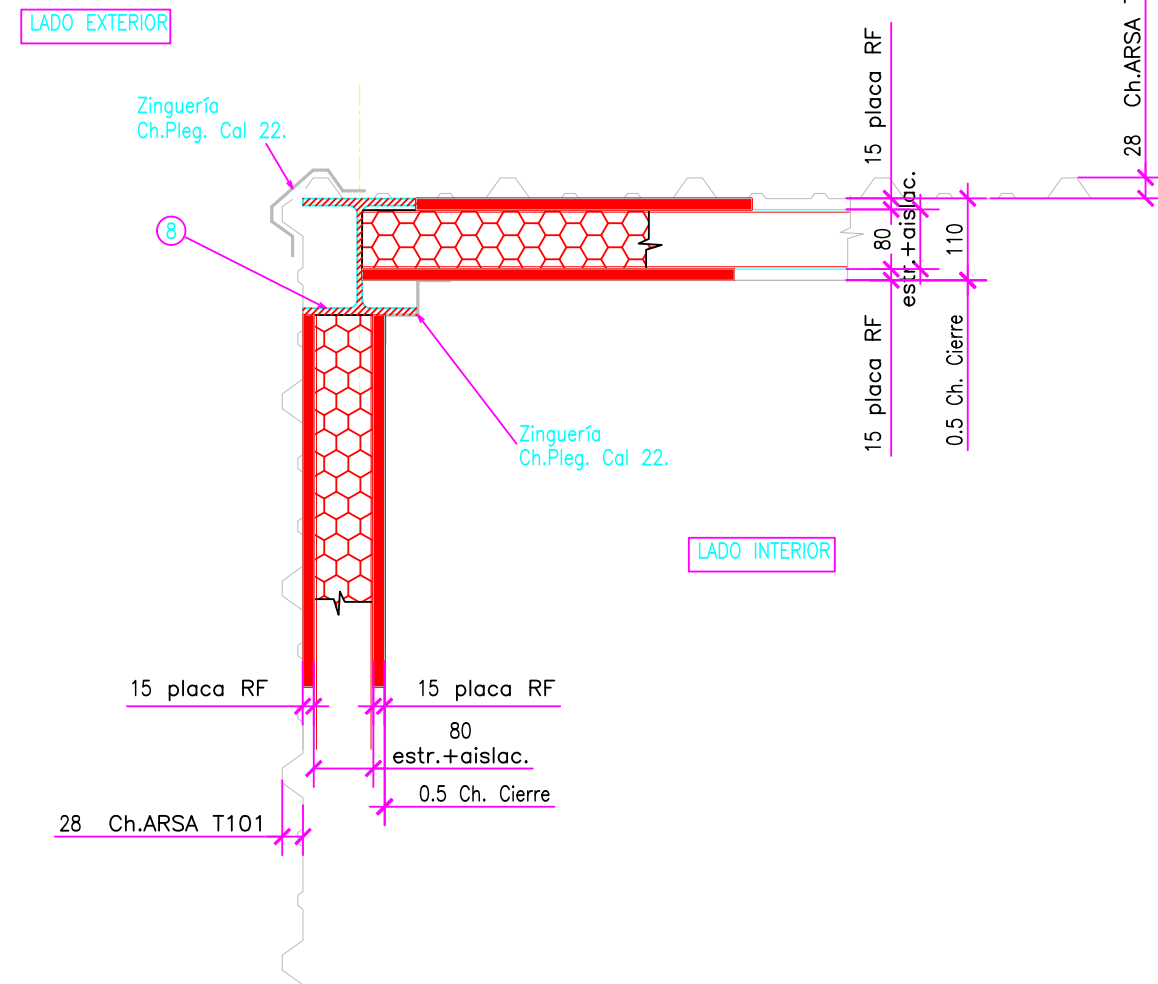

LISTA DE EQUIPOS

- 1.0 SEM-01 SALA DE MT
1.1 TSM-01 TABLERO SECCIONAL SALA DE MT
1.2 PRES-1 PRESURIZADOR SALA DE MT
1.3 HVAC-1 AIRE ACOND CALEFACCION Y VENTILACION SALA DE MT
1.4 HVAC-2 AIRE ACOND CALEFACCION Y VENTILACION SALA DE MT
1.5 HVAC-3 AIRE ACOND CALEFACCION Y VENTILACION SALA DE MT
1.6 HVAC-4 AIRE ACOND CALEFACCION Y VENTILACION SALA DE MT
1.7 HVAC-5 AIRE ACOND CALEFACCION Y VENTILACION SALA DE MT
1.8 JB-F&G-FAC2-03 TABLERO FIRE & GAS AGENTE DE EXTINCION SALA DE MT- SEM-01
1.9 TMT-02 TABLERO DE MEDIA TENSION ETAPA TEMPRANA
1.10 0106-KD-1501-VDF VARIADOR DE FRECUENCIA COMPRESOR GAS DE TOPE
1.11 0106-KD-1601-VDF VARIADOR DE FRECUENCIA COMPRESOR GAS DE TOPE
- 2.0 SEM-02 SALA DE BT
2.1 TSM-02 TABLERO SECCIONAL SALA DE BT
2.2 PRES-2 PRESURIZADOR SALA DE BT
2.3 HVAC-6 AIRE ACOND CALEFACCION Y VENTILACION SALA DE BT
2.4 HVAC-7 AIRE ACOND CALEFACCION Y VENTILACION SALA DE BT
2.5 JB-F&G-FAC2-02 TABLERO FIRE & GAS AGENTE DE EXTINCION SALA DE BT- SEM-02
2.6 COM-SA-12 COM MODULO DE ESTABILIZACION ET
2.7 TSA-SHELTER-12 TABLERO DE SERVICIOS AUXILIARES SHELTER-12
2.8 TD-TIGR-ET TABLERO DE TRACING ETAPA TEMPRANA
2.9 UPS-220VAC ET-N1 SISTEMA DE ALIMENTACION ININTERRUPIDA 220VCA ENTRADA NORMAL
2.10 UPS-220VAC ET-B SISTEMA DE ALIMENTACION ININTERRUPIDA 220VCA ENTRADA BY-PASS + BSD700
2.11 UPS-220VAC ET-FU SISTEMA DE ALIMENTACION ININTERRUPIDA 220VCA FUSIBLES (UPS)
2.12 TD-UPS TABLERO DISTRIBUCION UPS 220 VCA
2.13 RCB-110VCC ET RECTIFICADOR CARGADOR DE BATERIAS 110 VCC
2.14 RCB-110VCC ET-FU RECTIFICADOR CARGADOR DE BATERIAS 110 VCC FUSIBLES (RCB-110VCC ET)
2.15 TD-110VCC ET TABLERO DE DISTRIBUCION 110VCC - ET
2.16 RCB-110VCC-2 RECTIFICADOR CARGADOR DE BATERIAS 110 VCC
2.17 RCB-110 VCC-2 ET-FU RECTIFICADOR CARGADOR DE BATERIAS 110 VCC FUSIBLES (RCB-110VCC-2 ET)
2.18 TD-110VCC-2 ET TABLERO DE DISTRIBUCION 110VCC-2 - ET
- 3.0 SEM-03 SALA DE BATERIAS
3.1 TSM-03 TABLERO SECCIONAL SALA DE BATERIAS
3.2 PRES-3 PRESURIZADOR SALA DE BATERIAS
3.3 EXT-3A EXTRACTOR #1 SALA DE BATERIAS
3.4 EXT-3B EXTRACTOR #2 SALA DE BATERIAS
3.5 UPS-220VAC ET-BB1 SISTEMA DE ALIMENTACION ININTERRUPIDA 220VCA BANCO BATERIAS N1
3.6 UPS-220VAC ET-BB2 SISTEMA DE ALIMENTACION ININTERRUPIDA 220VCA BANCO BATERIAS N2
3.7 RCB-110VCC ET-BB RECTIFICADOR CARGADOR DE BATERIAS 110 VCC BANCO BATERIAS (RCB-110VCC ET)
3.8 RCB-110VCC-2 ET-BB RECTIFICADOR CARGADOR DE BATERIAS 110 VCC BANCO BATERIAS (RCB-110VCC-2 ET)

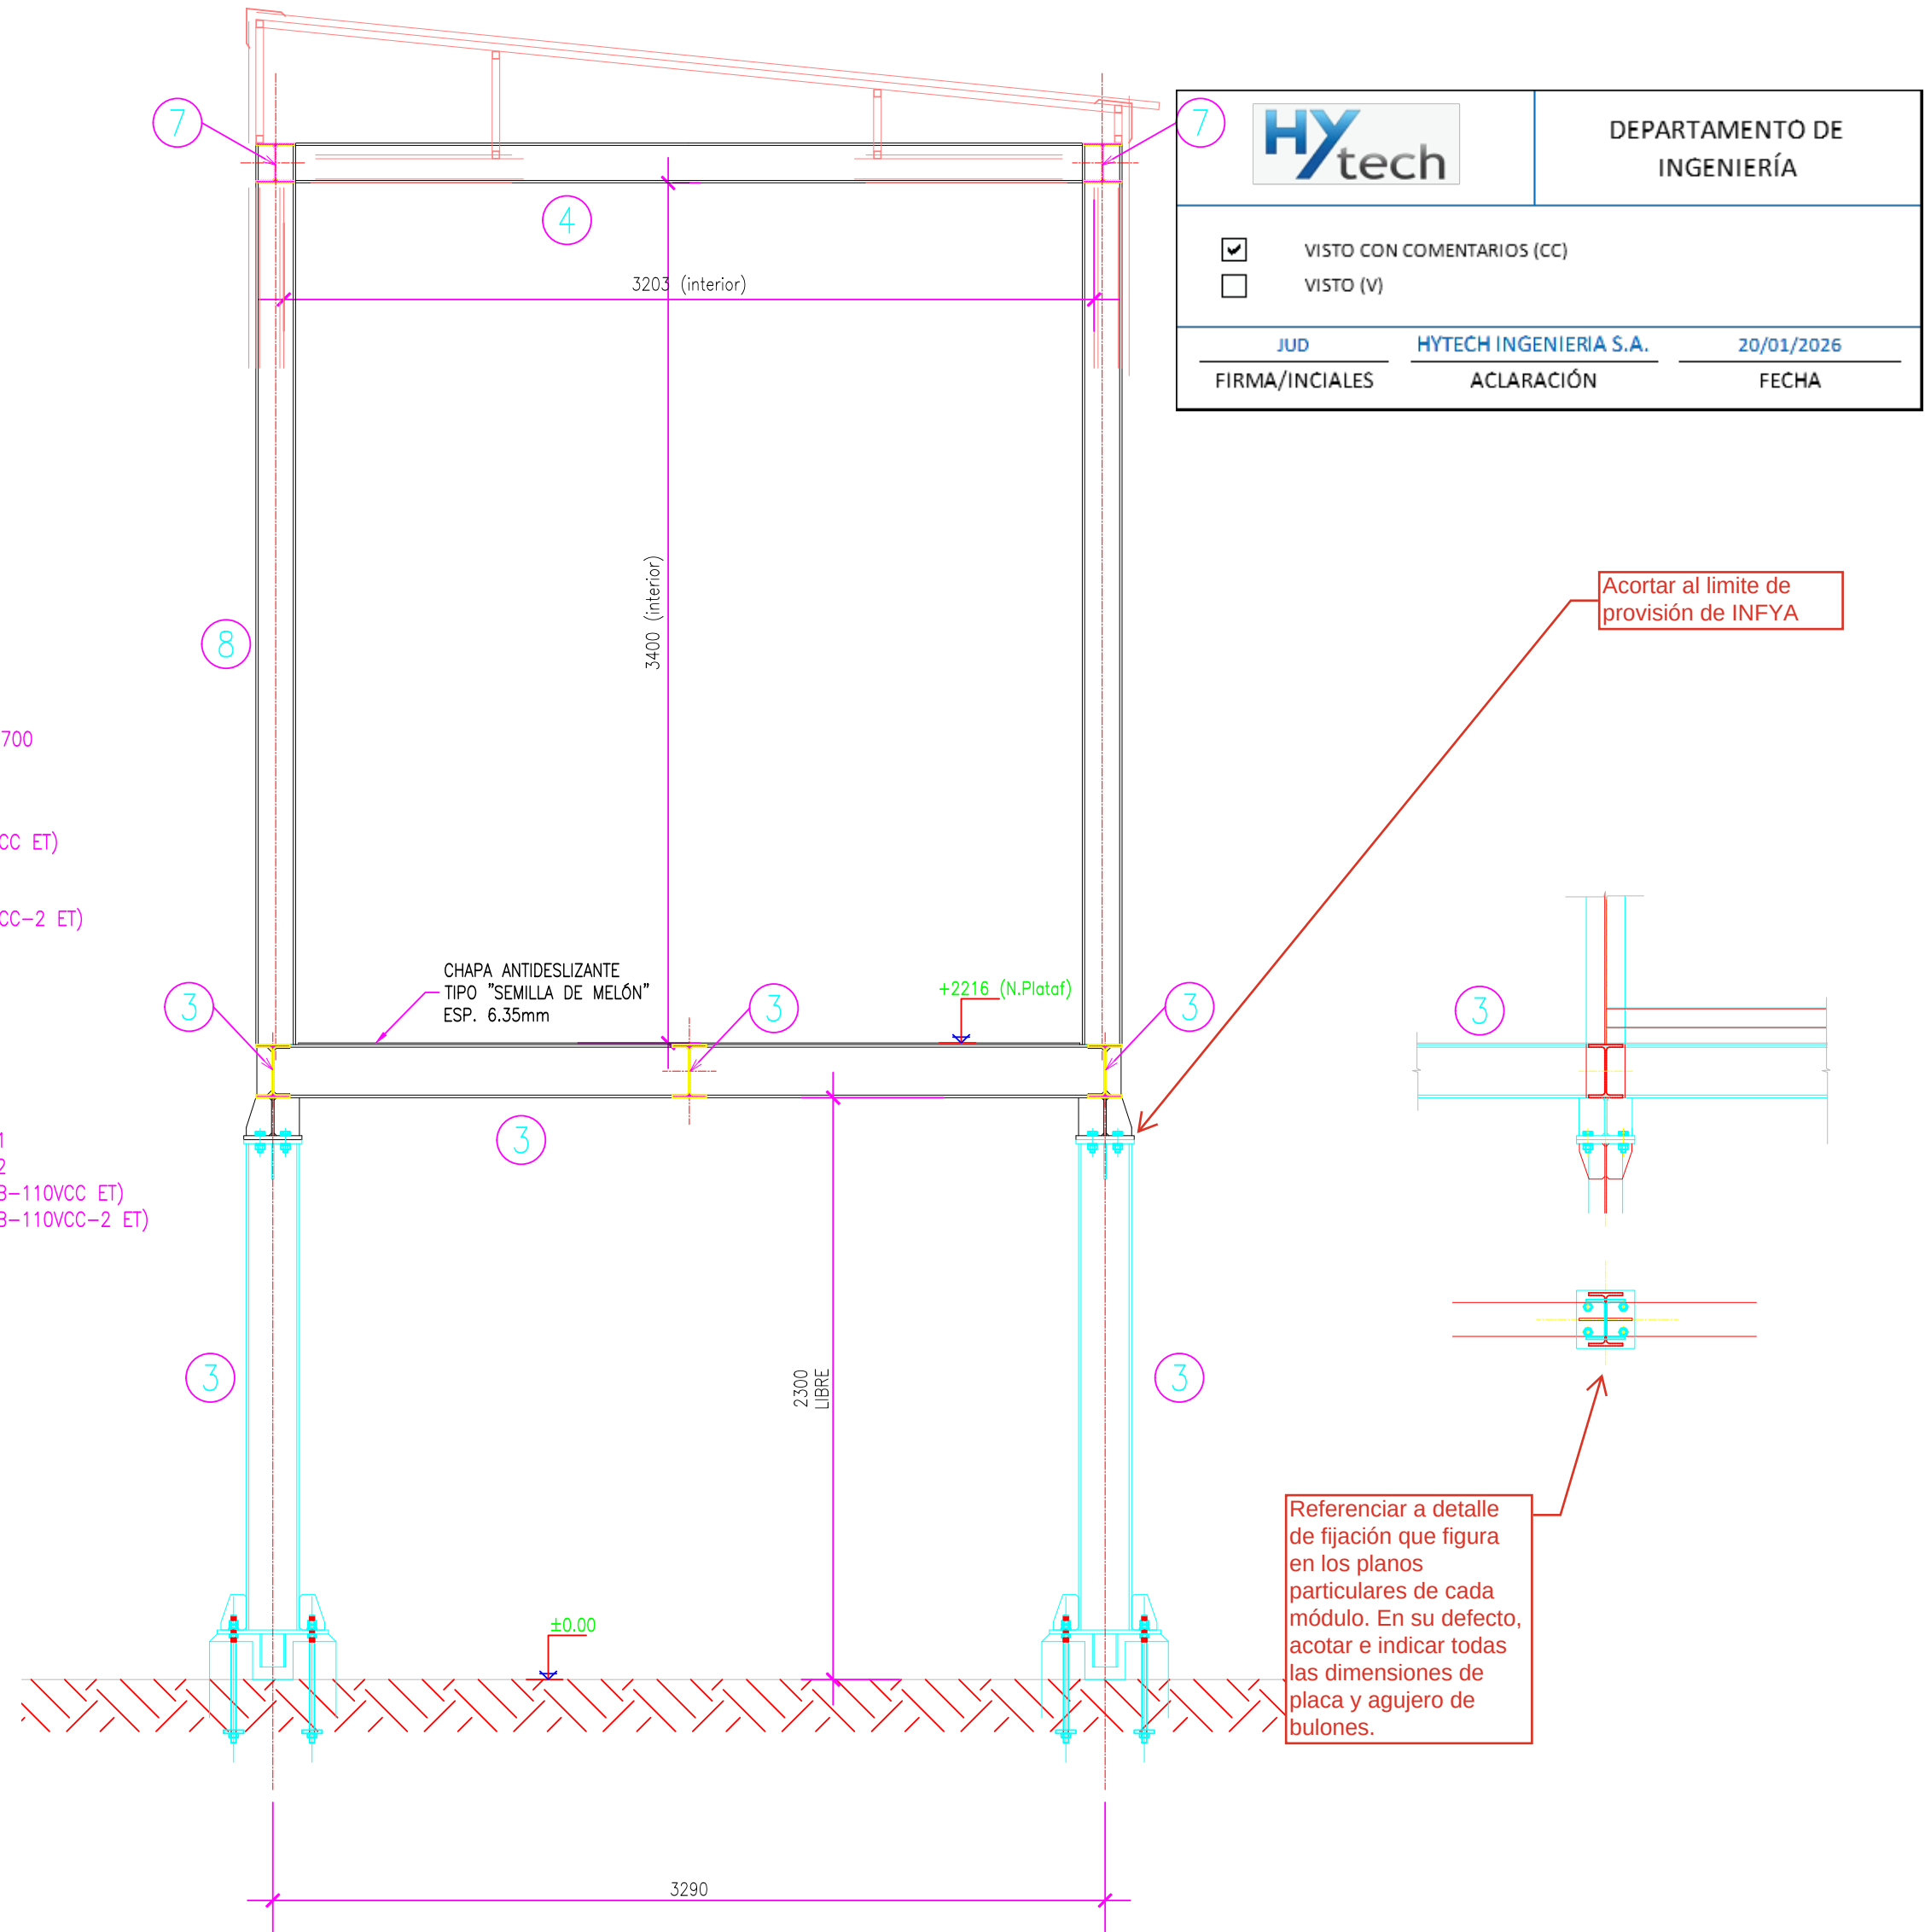

CORTE A-A
ESCALA 1:25

Confirmar que las escaleras de acceso y plataformas son parte de la provisión de INFYA.


NOTAS 1:

- MEDIDAS EN mm.
- CALIDAD PERFILES LAMINADOS W: ACERO F-36 o ASTM A-572 Gr50.
- CALIDAD PERFILES LAMINADOS, CHAPAS y PLANCHUELAS: ACERO F-24.
- LAS COLUMNAS DE SOPORTE Y LAS FUNDACIONES INDICADAS SON MERAMENTE ILUSTRATIVAS, ESTAN FUERA DEL ALCANCE DEL PROYECTO.

NOTA 2:

- NUMERACIÓN DE EQUIPOS S/ LISTADO DE EQUIPOS.

0	15/12/2025	EMISIÓN PARA APROBACIÓN	AMB	RMP	JJA
REV	FECHA	DESCRIPCIÓN	ELABORO	REVISO	APROBO
tgs			DIRECCIÓN DE OPERACIONES GERENCIA		
LUGAR: NEUQUÉN - PLANTA TRATAYÉN			TÍTULO: PLANO DE ESTRUCTURAS METÁLICAS LAYOUT GENERAL		
OBRA: SALAS ELÉCTRICAS PLANTA ESTABILIZADORA CONDENSADOS SLUG CATCHER - NGL ETAPA TEMPRANA			FECHA: 15/12/25		
ESPACIO CONTRASTA			OBRA N°: 104.728		
N° Doc. Ingeniería:			ESCALA: INDICADAS		
Rev:			HOJA: 1 de 6		
			DOCUMENTO: TE-631-104728-LY-C-1701		
			REVISIÓN: 0		

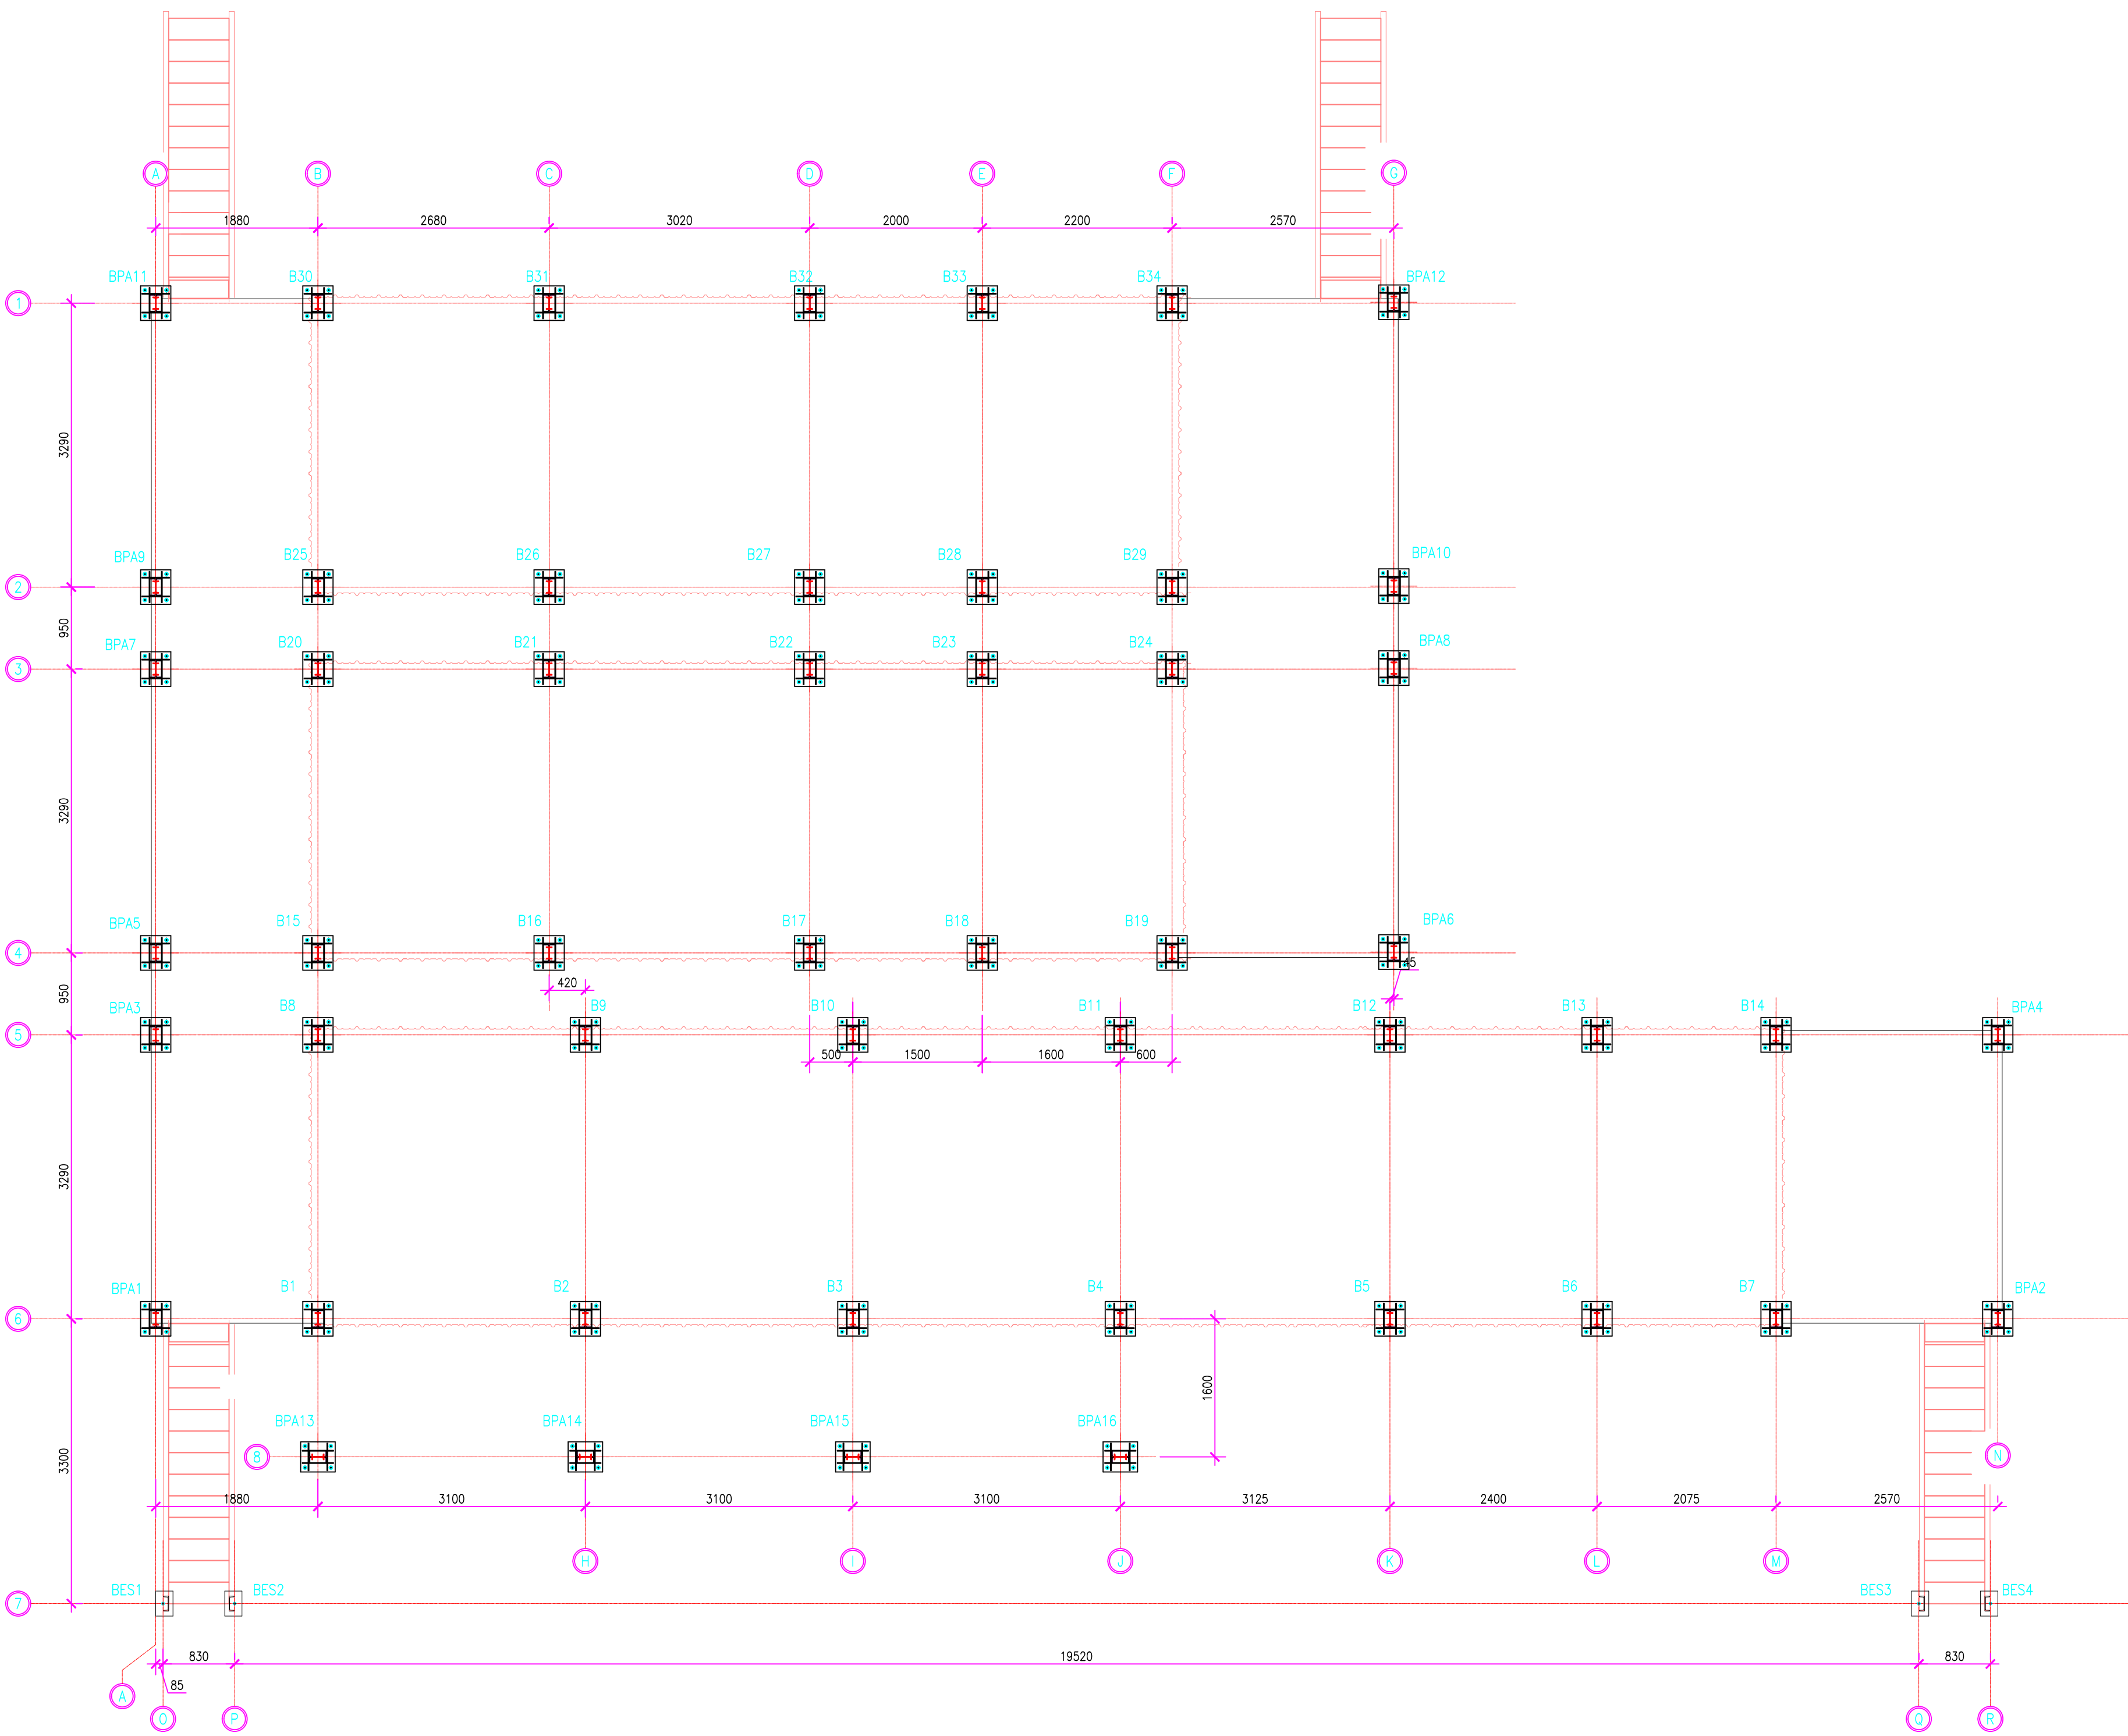


PLANTA BASES
ESCALA 1:50

Confirmar que las escaleras de acceso y plataformas son parte de la provisión de INFYA.
Indicar el esquema de vinculación de las placas de anclaje de las escalera a la fundación que será provista por terceros.


NOTAS 1:

- MEDIDAS EN mm.
- CALIDAD PERFILES LAMINADOS W: ACERO F-36 o ASTM A-572 Gr50.
- CALIDAD PERFILES LAMINADOS, CHAPAS y PLANCHUELAS: ACERO F-24.
- LAS COLUMNAS DE SOPORTE Y LAS FUNDACIONES INDICADAS SON MERAMENTE ILUSTRATIVAS, ESTAN FUERA DEL ALCANCE DEL PROYECTO.

0	15/12/2025	EMISIÓN PARA APROBACIÓN	AMB	RMP	JJA
REV.	FECHA	DESCRIPCIÓN	ELABORO	REVISO	APROBO
tgs			DIRECCIÓN DE OPERACIONES GERENCIA		
LUGAR: NEUQUÉN - PLANTA TRATAYÉN			TÍTULO: PLANO DE ESTRUCTURAS METÁLICAS REPLANTEO BASES		
OBRA: SALAS ELÉCTRICAS PLANTA ESTABILIZADORA CONDENSADOS SLUG CATCHER - NGL ETAPA TEMPORAL					
ESPACIO CONTRASTA			FECHA: 15/12/25	OBRA N°: 104.728	ESCALA: INDICADAS
DOCUMENTO:			HOJA: 2 de 6		REVISIÓN
N° Doc. Ingeniería:			Rev:		0
			TE-631-104728-LY-C-1701		

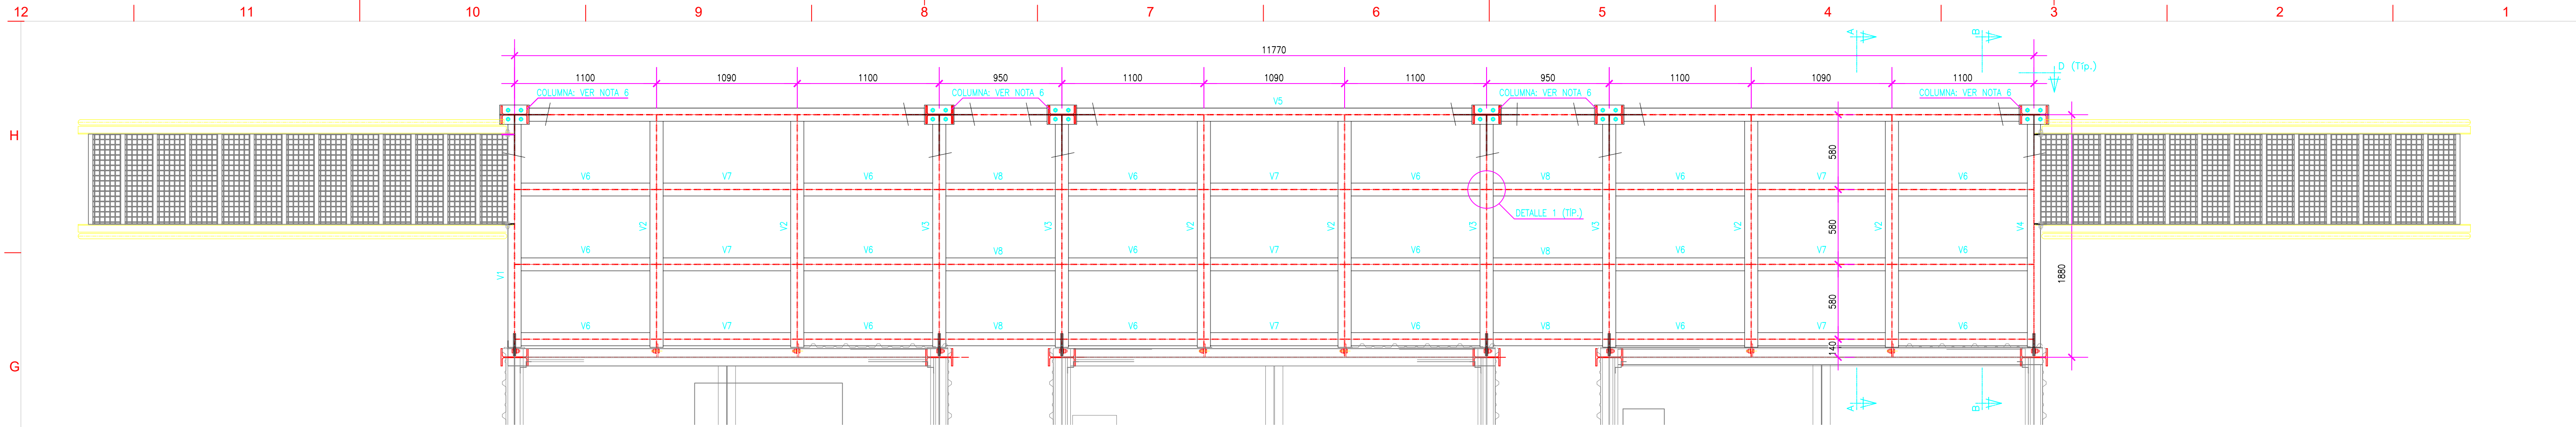


PLANTA ESTRUCTURA PLATAFORMA SEM-01 / SEM-02 / SEM-03
ESCALA 1:25

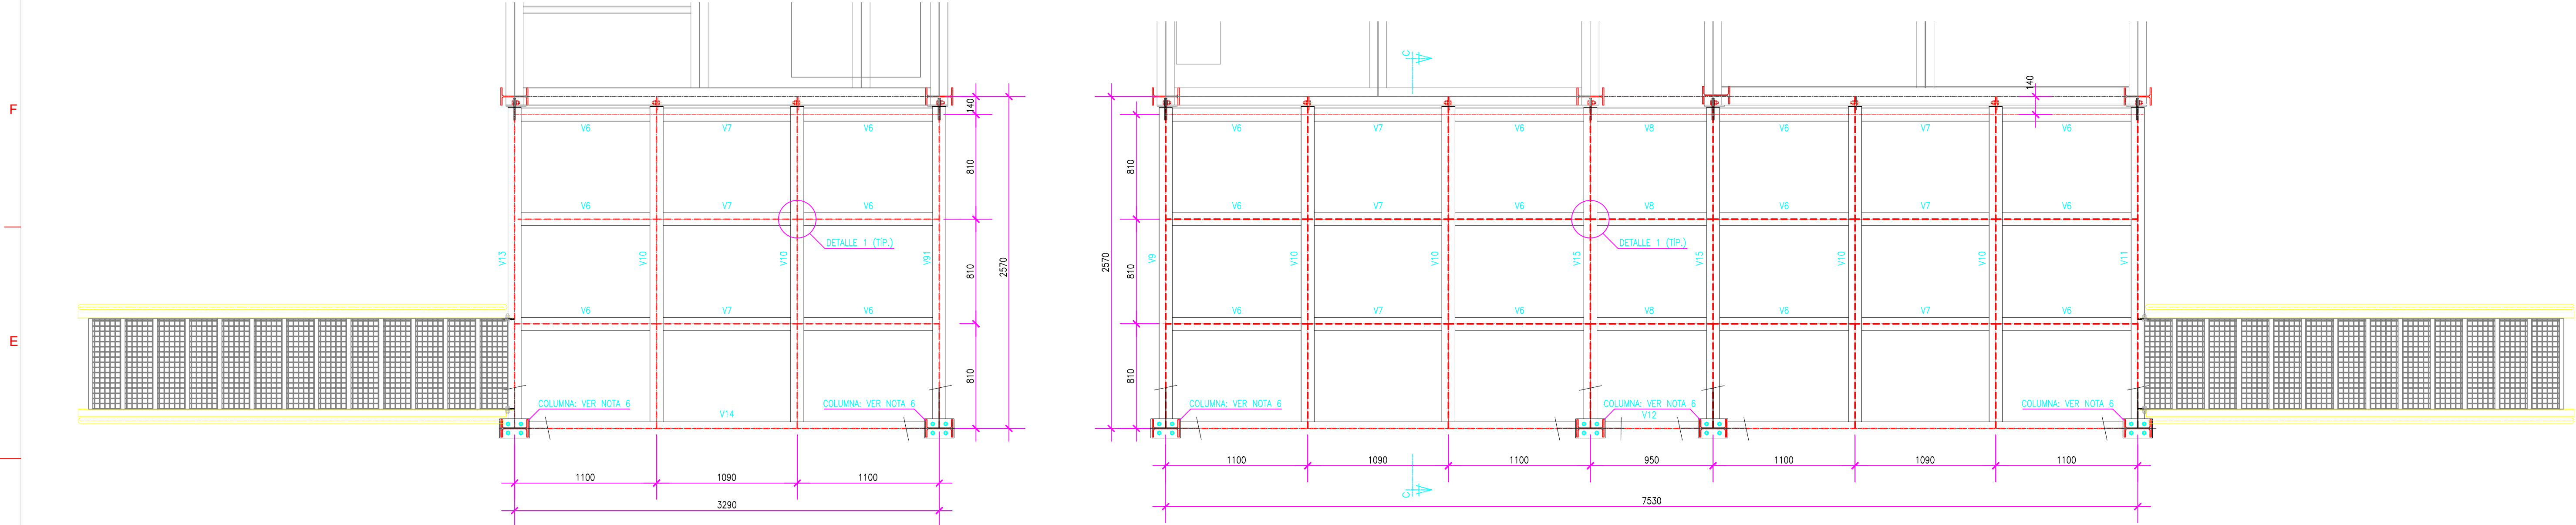


PLANTA ESTRUCTURA PLATAFORMA SEM-01
ESCALA 1:25

PLANTA ESTRUCTURA PLATAFORMA SEM-02 y SEM-03
ESCALA 1:25

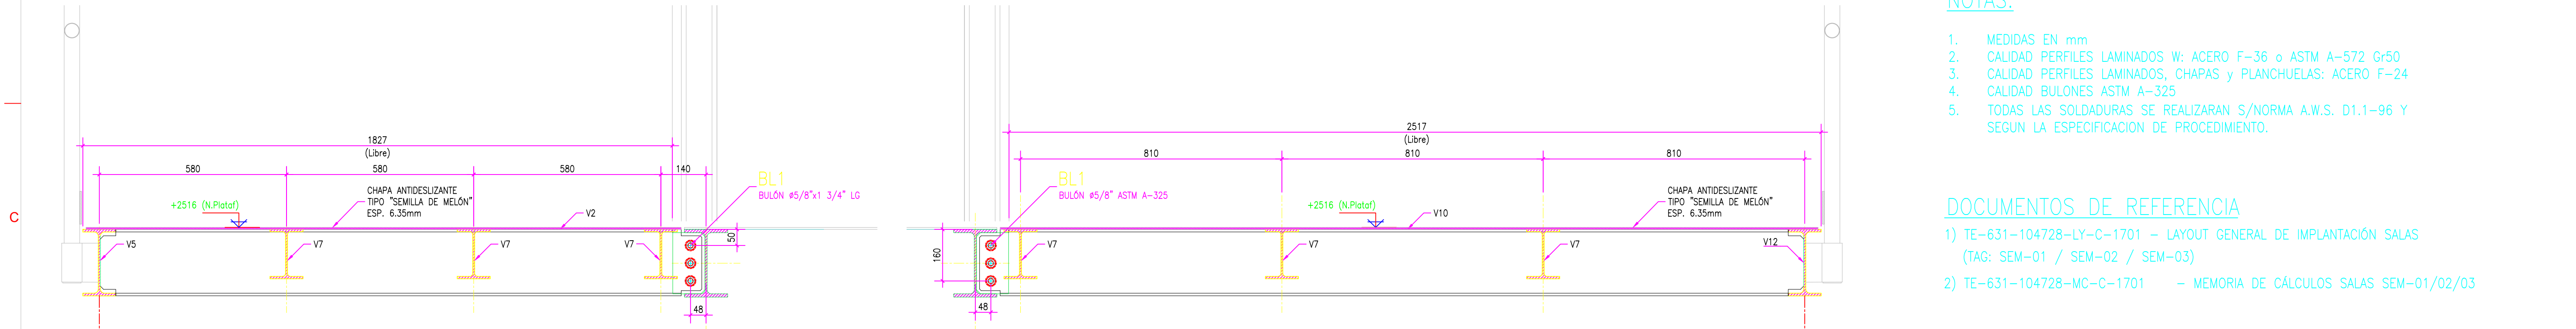

CORTE A-A
ESCALA 1:10

CORTE C-C
ESCALA 1:10

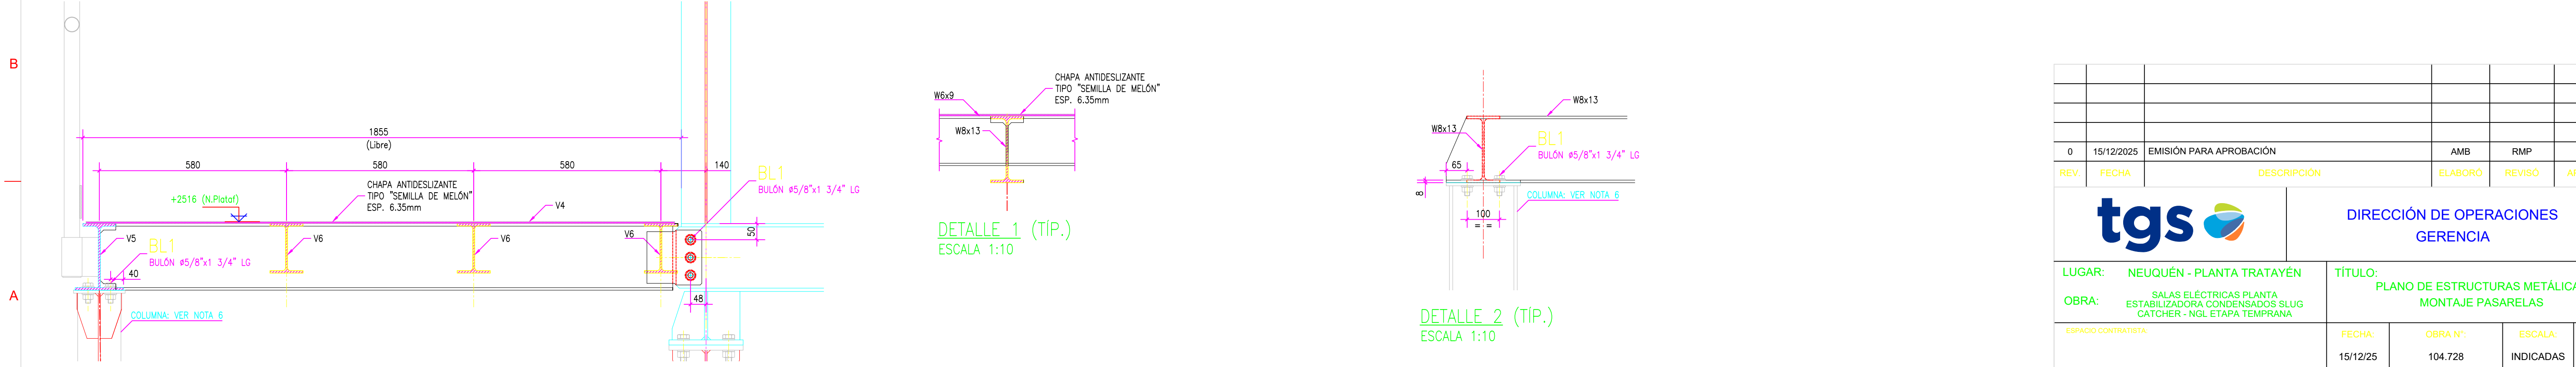

CORTE B-B
ESCALA 1:10

DETALLE 1 (TIP.)
ESCALA 1:10

DETALLE 2 (TIP.)
ESCALA 1:10


NOTAS:

1. MEDIDAS EN mm
2. CALIDAD PERFILES LAMINADOS W: ACERO F-36 o ASTM A-572 Gr50
3. CALIDAD PERFILES LAMINADOS, CHAPAS y PLANCHUELAS: ACERO F-24
4. CALIDAD BULONES ASTM A-325
5. TODAS LAS SOLDADURAS SE REALIZARAN S/NORMA A.W.S. D1.1-96 Y SEGUN LA ESPECIFICACION DE PROCEDIMIENTO.

DOCUMENTOS DE REFERENCIA

- 1) TE-631-104728-LY-C-1701 - LAYOUT GENERAL DE IMPLANTACIÓN SALAS (TAG: SEM-01 / SEM-02 / SEM-03)
- 2) TE-631-104728-MC-C-1701 - MEMORIA DE CÁLCULOS SALAS SEM-01/02/03

0	15/12/2025	EMISIÓN PARA APROBACIÓN	AMB	RMP	JJA
REV.	FECHA	DESCRIPCIÓN	ELABORÓ	REVISÓ	APROBO
tgs			DIRECCIÓN DE OPERACIONES GERENCIA		
LUGAR: NEUQUÉN - PLANTA TRATAYÉN			TÍTULO: PLANO DE ESTRUCTURAS METÁLICAS MONTAJE PASARELAS		
OBRA: SALAS ELÉCTRICAS PLANTA ESTABILIZADORA CONDENSADOS SLUG CATCHER - NGL ETAPA TEMPRANA			FECHA: 15/12/25	OBRA N°: 104.728	ESCALA: INDICADAS
N° Doc. Ingeniería:			DOCUMENTO: TE-631-104728-LY-C-1701	HOJA: 4 de 6	REVISIÓN: 0

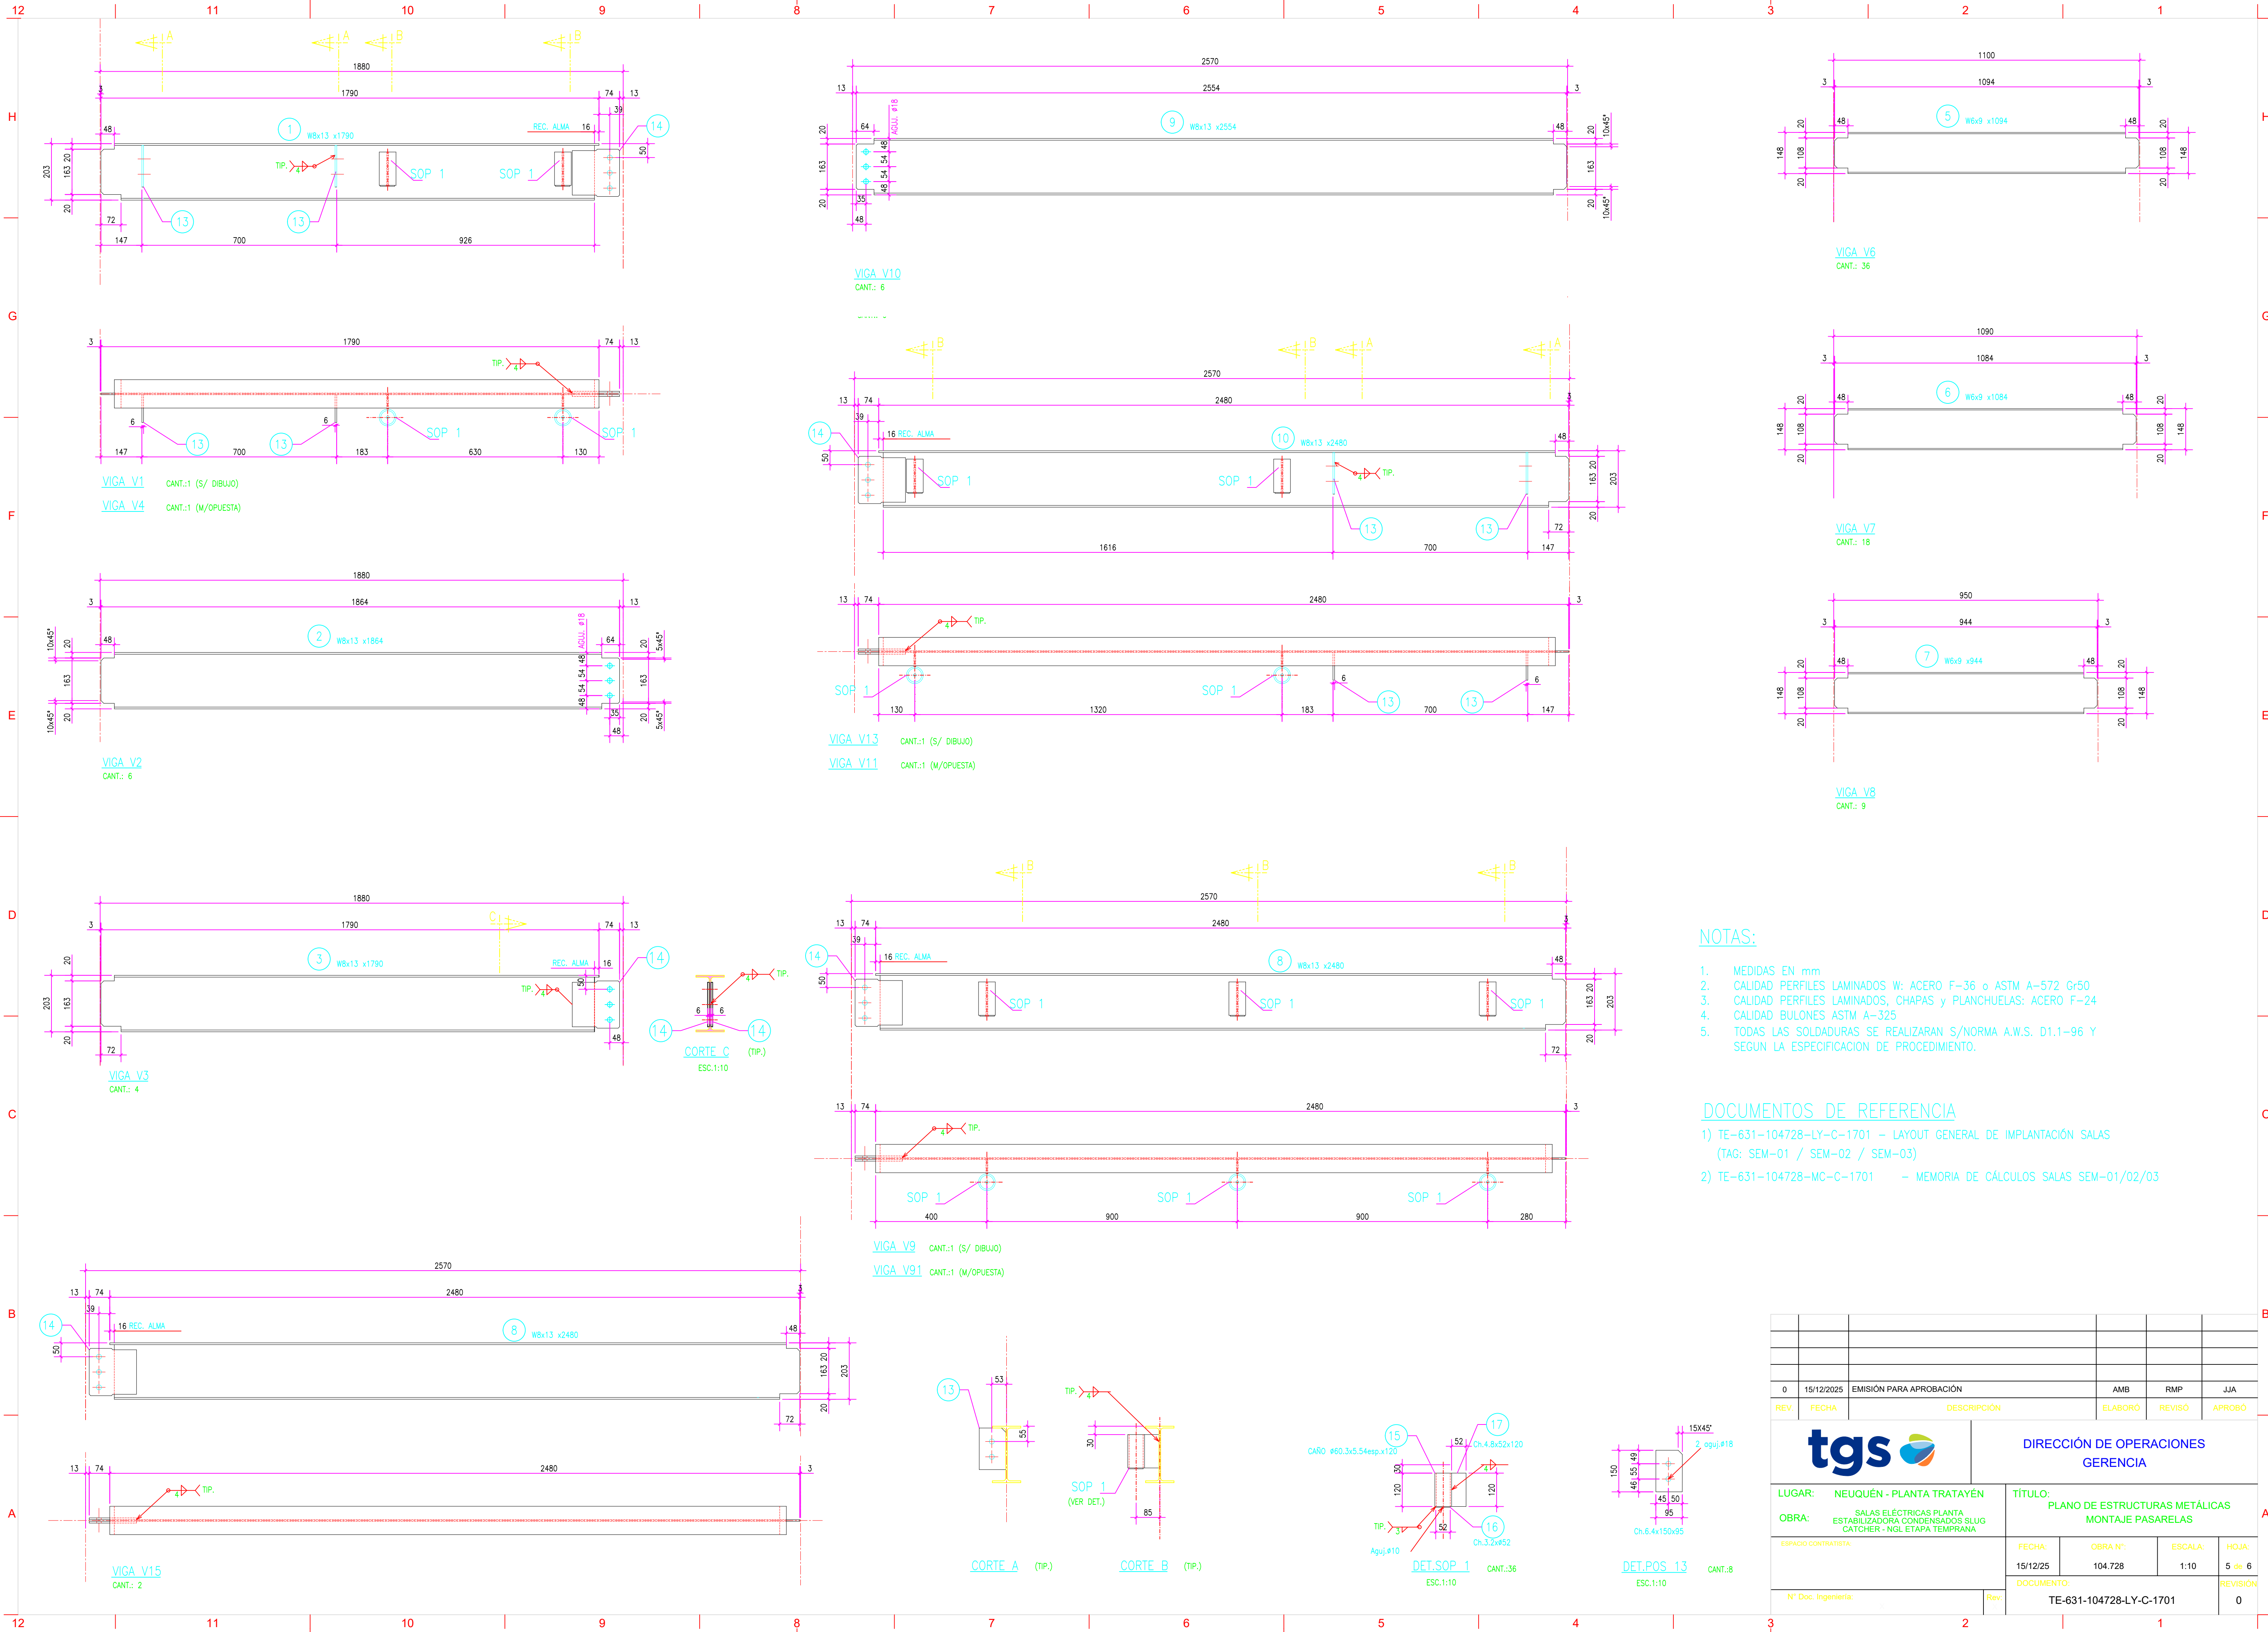


NOTAS:

- MEDIDAS EN mm
- CALIDAD PERFILES LAMINADOS W: ACERO F-36 o ASTM A-572 Gr50
- CALIDAD PERFILES LAMINADOS, CHAPAS y PLANCHUELAS: ACERO F-24
- CALIDAD BULONES ASTM A-325
- TODAS LAS SOLDADURAS SE REALIZARAN S/NORMA A.W.S. D1.1-96 Y SEGUN LA ESPECIFICACION DE PROCEDIMIENTO.

DOCUMENTOS DE REFERENCIA

- TE-631-104728-LY-C-1701 - LAYOUT GENERAL DE IMPLANTACIÓN SALAS (TAG: SEM-01 / SEM-02 / SEM-03)
- TE-631-104728-MC-C-1701 - MEMORIA DE CÁLCULOS SALAS SEM-01/02/03

0	15/12/2025	EMISIÓN PARA APROBACIÓN	AMB	RMP	JJA
REV.	FECHA	DESCRIPCIÓN	ELABORÓ	REVISÓ	APROBO
tgs			DIRECCIÓN DE OPERACIONES GERENCIA		
LUGAR: NEUQUÉN - PLANTA TRATAYÉN			TÍTULO: PLANO DE ESTRUCTURAS METÁLICAS MONTAJE PASARELAS		
OBRA: SALAS ELÉCTRICAS PLANTA ESTABILIZADORA CONDENSADOS SLUG CATCHER - NGL ETAPA TEMPRANA					
ESPACIO CONTRASTA			FECHA:	OBRA N°:	ESCALA:
			15/12/25	104.728	1:10
DOCUMENTO:			HOJA:		
N° Doc. Ingeniería:			TE-631-104728-LY-C-1701		
Rev:			REVISIÓN		
			0		

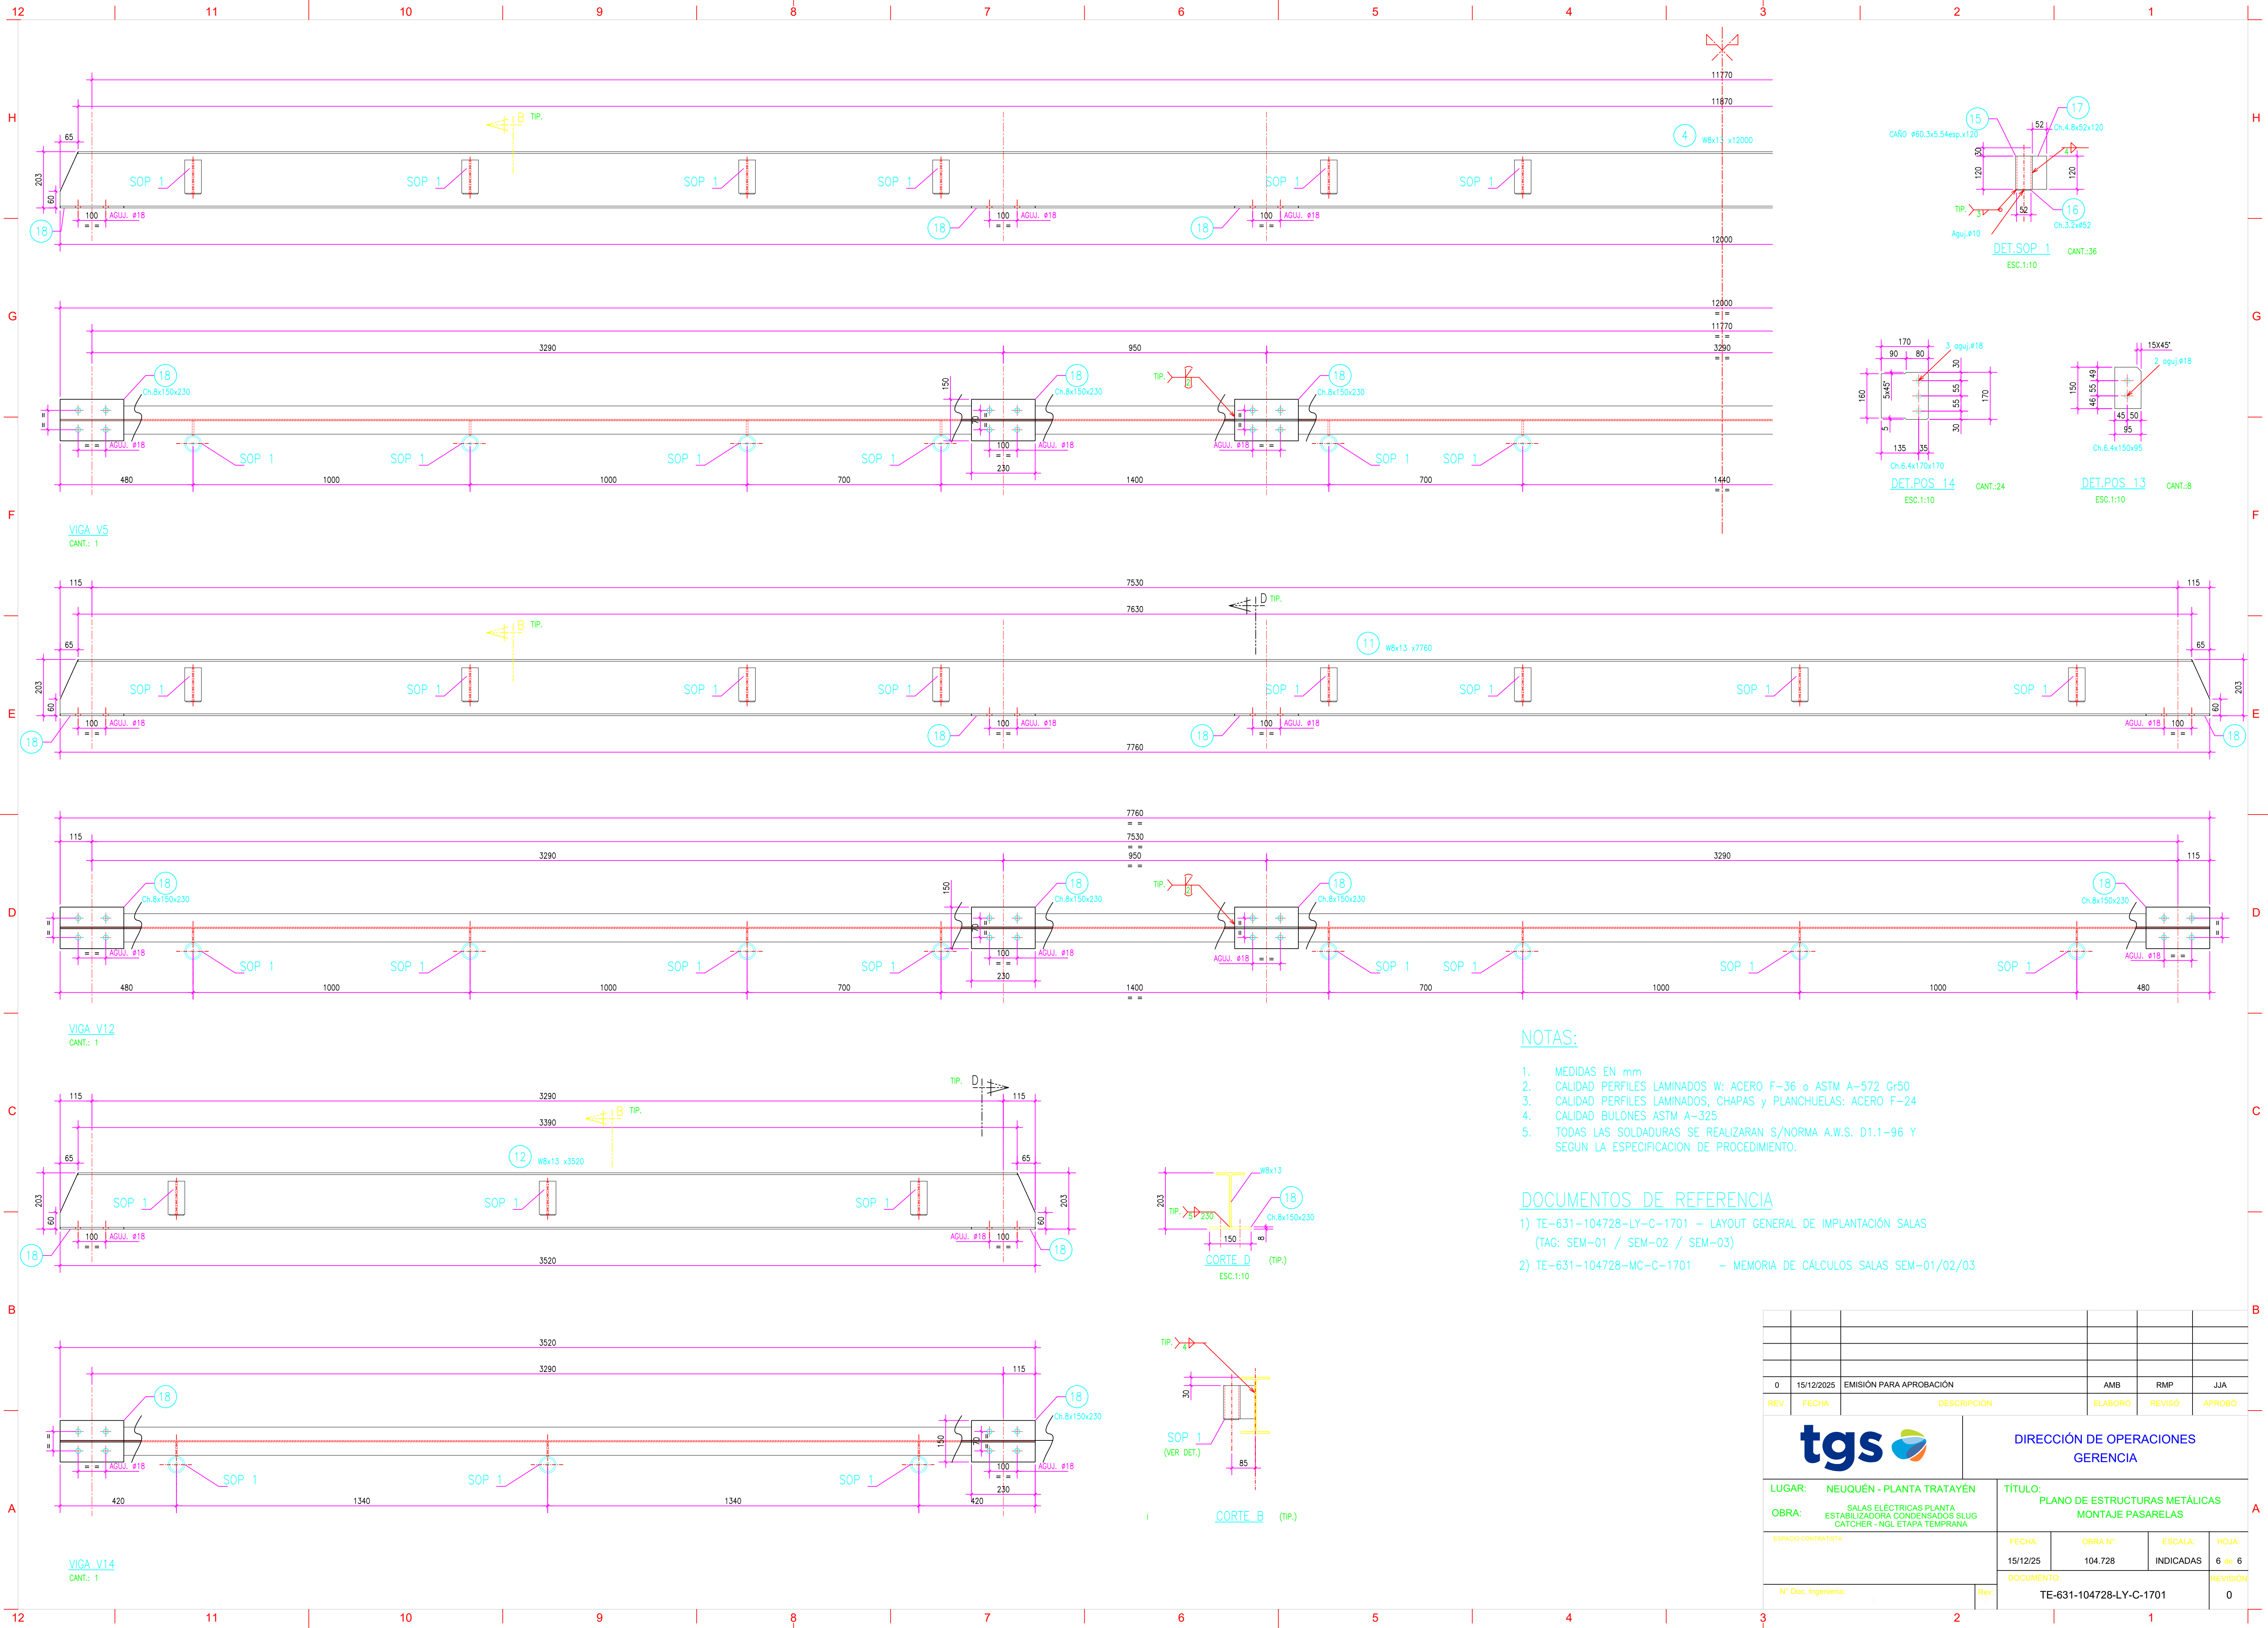

NOTAS:

- 1. MEDIDAS EN mm
- 2. CALIDAD PERFILES LAMINADOS W: ACERO F-36 o ASTM A-572 Gr50
- 3. CALIDAD PERFILES LAMINADOS, CHAPAS y PLANCHUELAS: ACERO F-24
- 4. CALIDAD BULONES ASTM A-325
- 5. TODAS LAS SOLDADURAS SE REALIZARAN S/NORMA A.W.S. D1.1-96 Y SEGUN LA ESPECIFICACION DE PROCEDIMIENTO.

DOCUMENTOS DE REFERENCIA

- 1) TE-631-104728-LY-C-1701 - LAYOUT GENERAL DE IMPLANTACIÓN SALAS (TAG: SEM-01 / SEM-02 / SEM-03)
- 2) TE-631-104728-MC-C-1701 - MEMORIA DE CÁLCULOS SALAS SEM-01/02/03

0	15/12/2025	EMISIÓN PARA APROBACIÓN		AMB	RMP
REV.	FECHA	DESCRIPCIÓN	ELABORÓ	REVISÓ	APROBÓ
tgs			DIRECCIÓN DE OPERACIONES GERENCIA		
LUGAR: NEUQUÉN - PLANTA TRATAYÉN			TÍTULO: PLANO DE ESTRUCTURAS METÁLICAS MONTAJE PASARELAS		
OBRA: SALAS ELÉCTRICAS PLANTA ESTABILIZADORA CONDENSADOS SLUG CATCHER - NGL ETAPA TEMPORARIA			FECHA: 15/12/25	OBRA N°: 104.728	ESCALA: INDICADAS
ESPACIO CONTRASTA			DOCUMENTO:	HOJA: 6 de 6	REVISIÓN
N° Doc. Ingeniería:			Rev:	TE-631-104728-LY-C-1701	0