
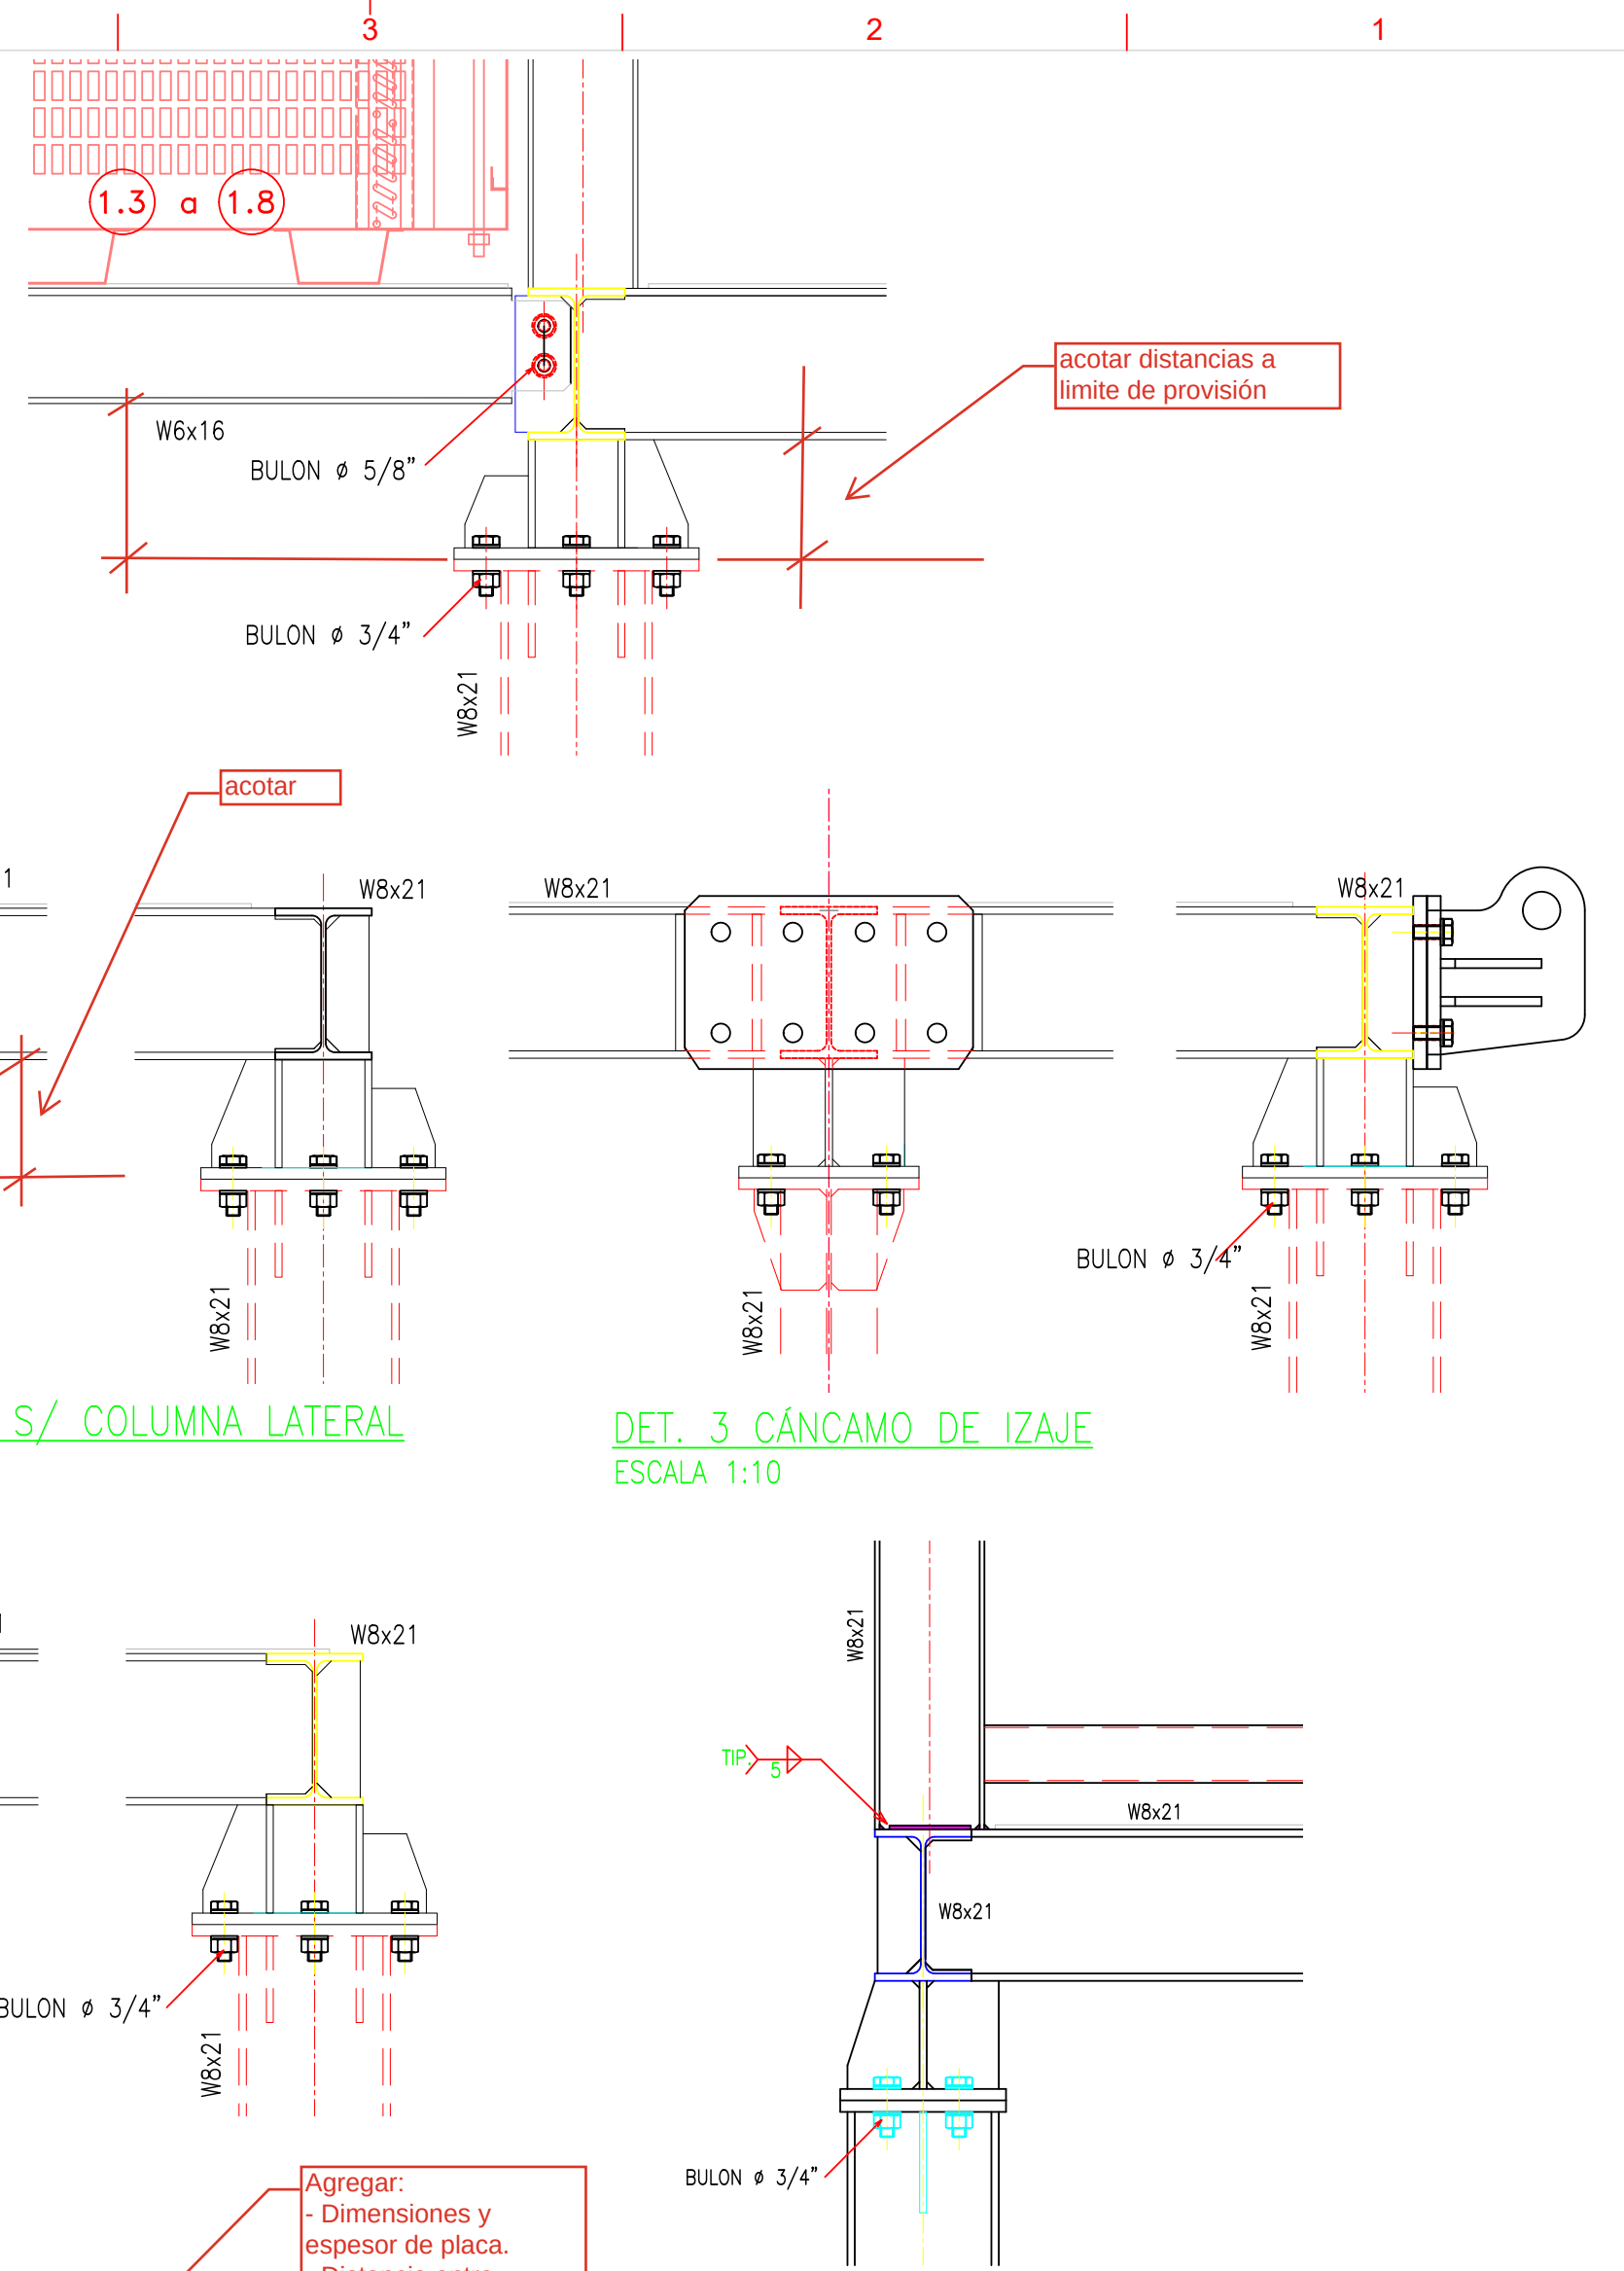


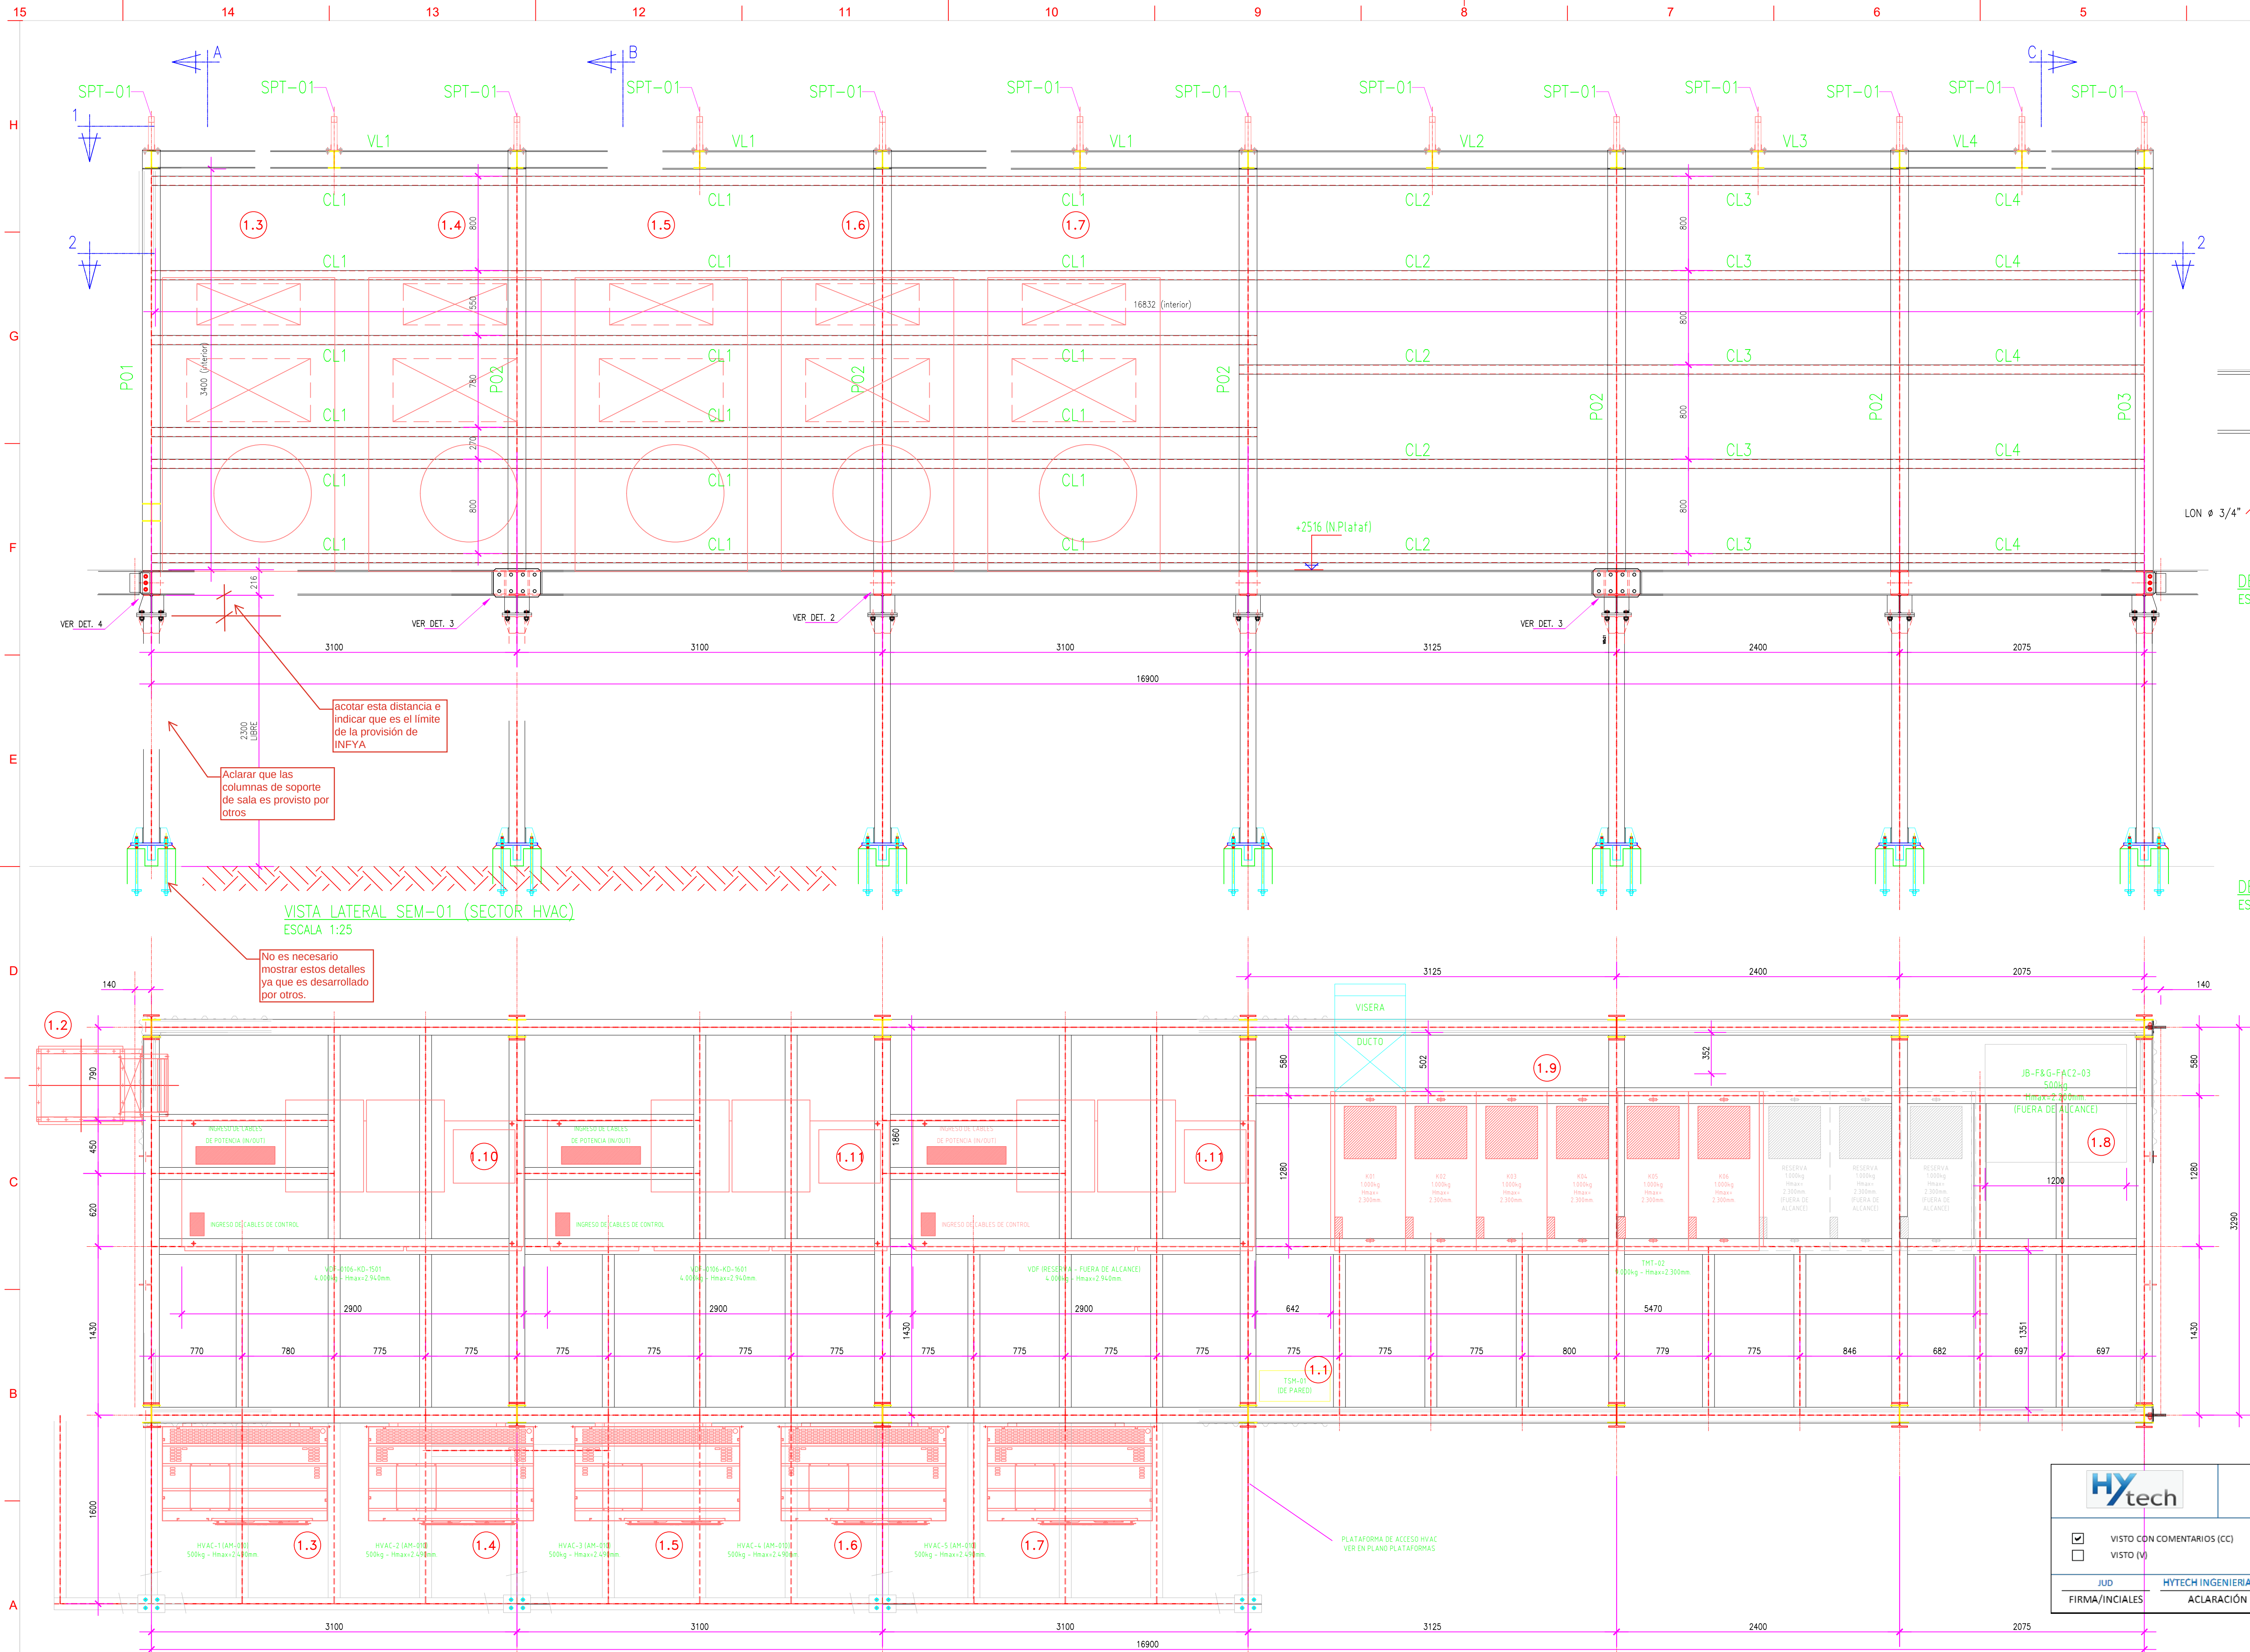

- PLANTA DET. 2,3 y 4 ESCALA 1:10
- REVISAR LAS PUNTAS DE IMPRESIÓN PARA MEJOR VISUALIZACIÓN DEL DOCUMENTO.
- REVISAR LAS DISTANCIAS ENTRE ARANDELA Y PERFIL AL QUE VERIFIQUE EL INGRESO DE LA LLAVE PARA AJUSTE.
- AGREGAR: - Dimensiones y espesor de placa. - Distancia entre bulones
- REVISAR LAS DISTANCIAS ENTRE ARANDELA Y PERFIL AL QUE VERIFIQUE EL INGRESO DE LA LLAVE PARA AJUSTE.


DOCUMENTOS DE REFERENCIA

1) TE-631-104728-LY-C-1701 - LAYOUT GENERAL DE IMPLANTACIÓN SALAS (TAG: SEM-01 / SEM-02 / SEM-03)


2) TE-631-104728-MC-C-1701 - MEMORIA DE CÁLCULOS SALAS SEM-01/02/03

HYtech		DEPARTAMENTO DE INGENIERÍA	
☒	VISTO CON COMENTARIOS (CC)		
☐	VISTO (V)		
JUD	HYTECH INGENIERÍA S.A.	20/01/2026	
FIRMA/INICIALES	ACLARACIÓN	FECHA	


tgs		DIRECCIÓN DE OPERACIONES GERENCIA	
LUGAR:	NEUQUÉN - PLANTA TRATAYÉN	TÍTULO:	
OBRA:	SALAS ELÉCTRICAS PLANTA ESTABILIZADORA CONDENSADOS SLUG CATCHER - NGL ETAPA TEMPORARIA	PLANO DE ESTRUCTURAS METÁLICAS MÓDULO N°1 (TAG: SEM-01)	
FECHA:	15/12/2025	OBRA N°:	104.728
ESCALA:	1 de 6	INDICADAS	
DOCUMENTO:	TE-631-104728-PL-C-1701	REVISIÓN	0

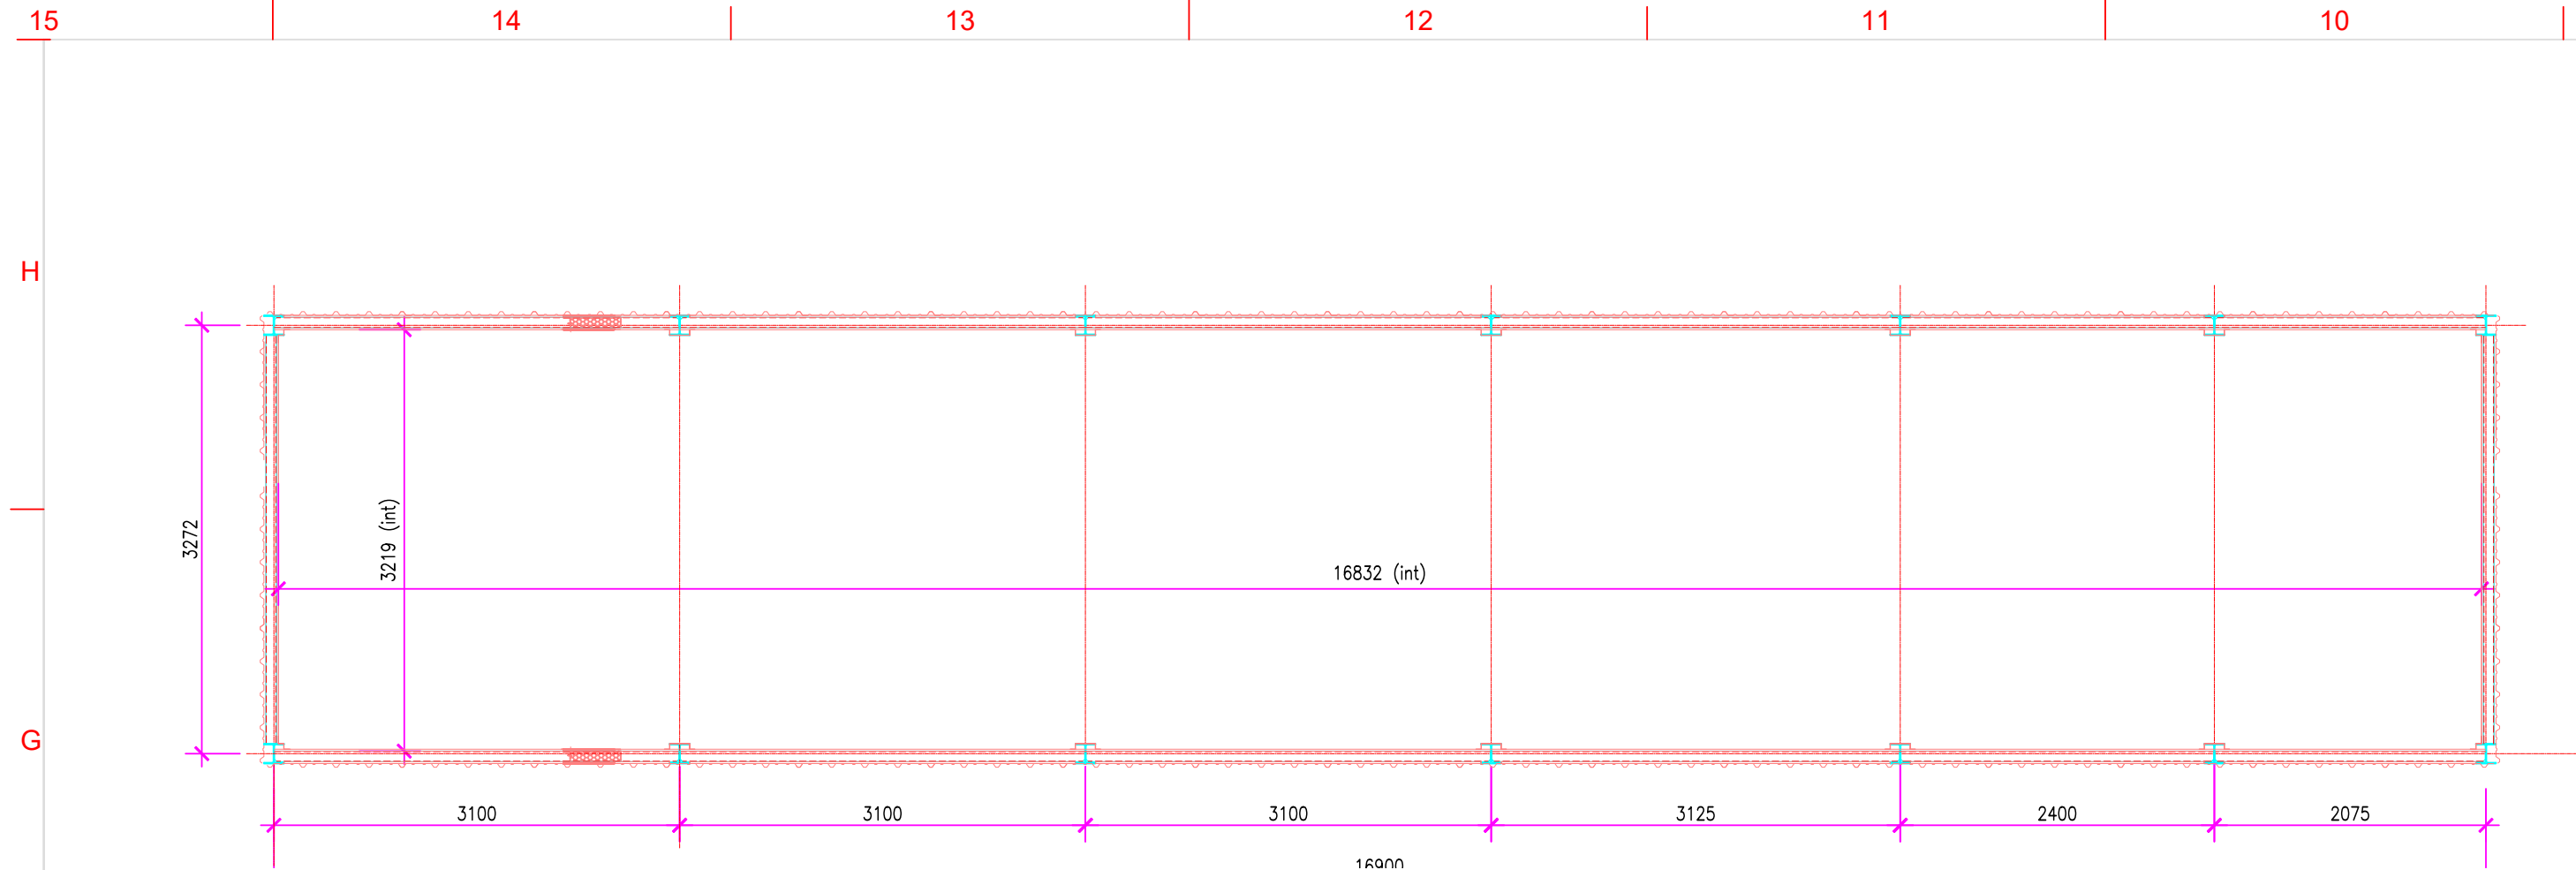


CORTE 2-2
ESCALA 1:50

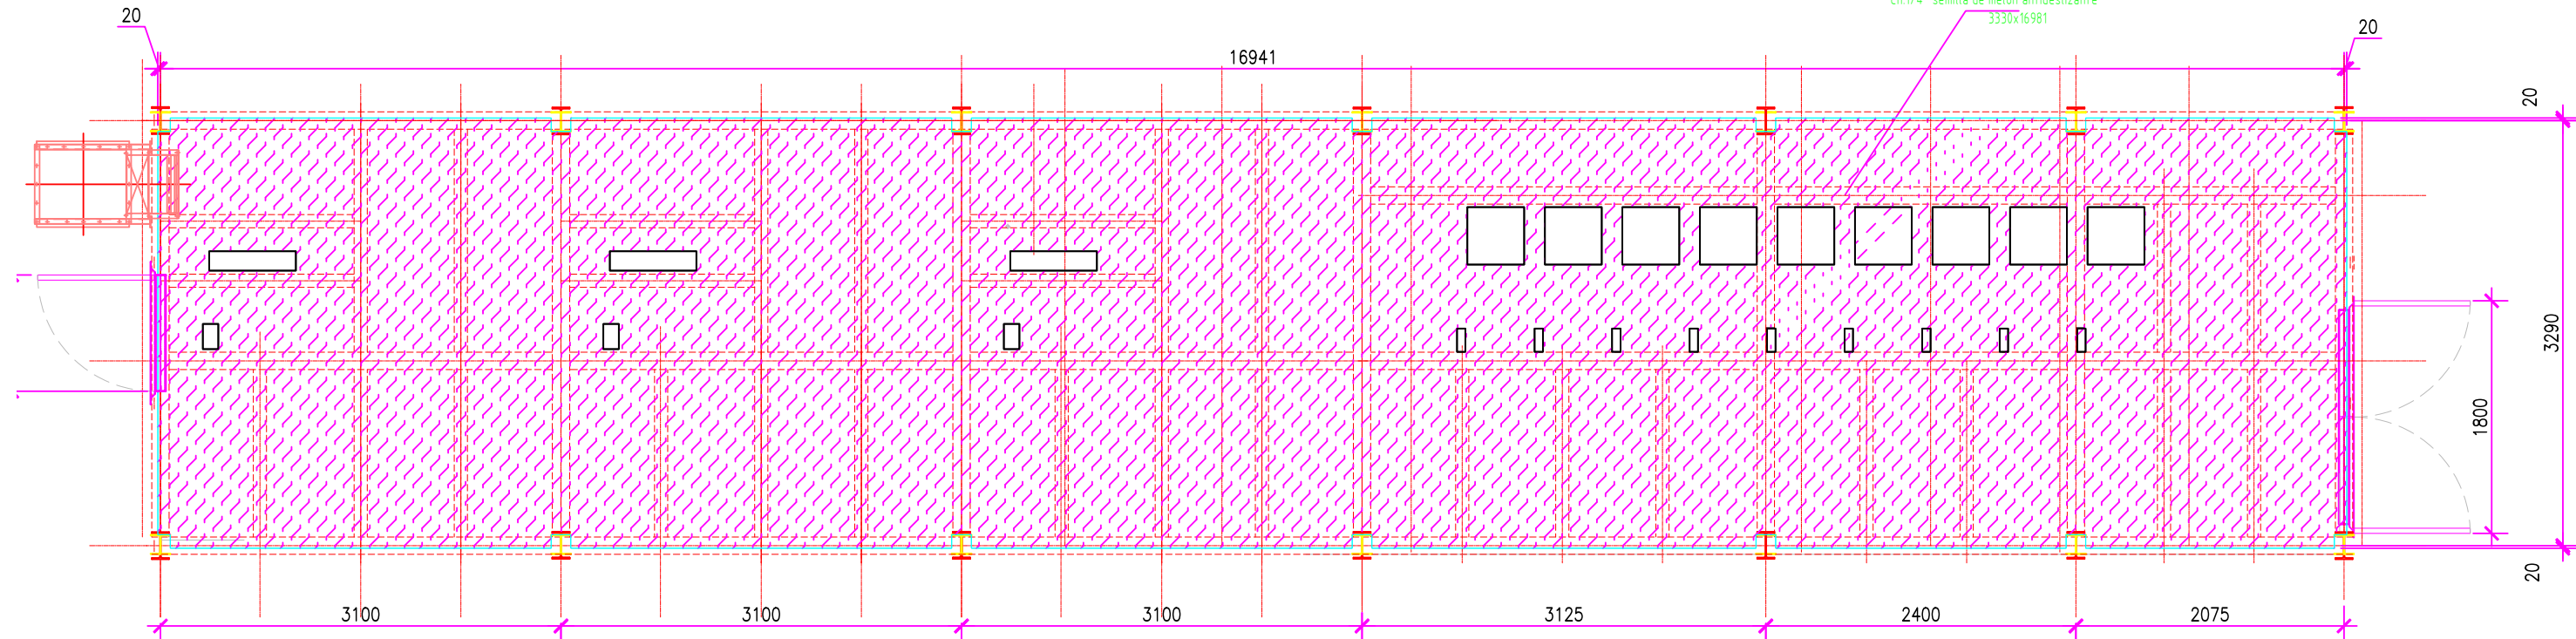



PLANTA CHAPA DE PISO PLATAFORMA PLT SEM-01
ESCALA 1:50

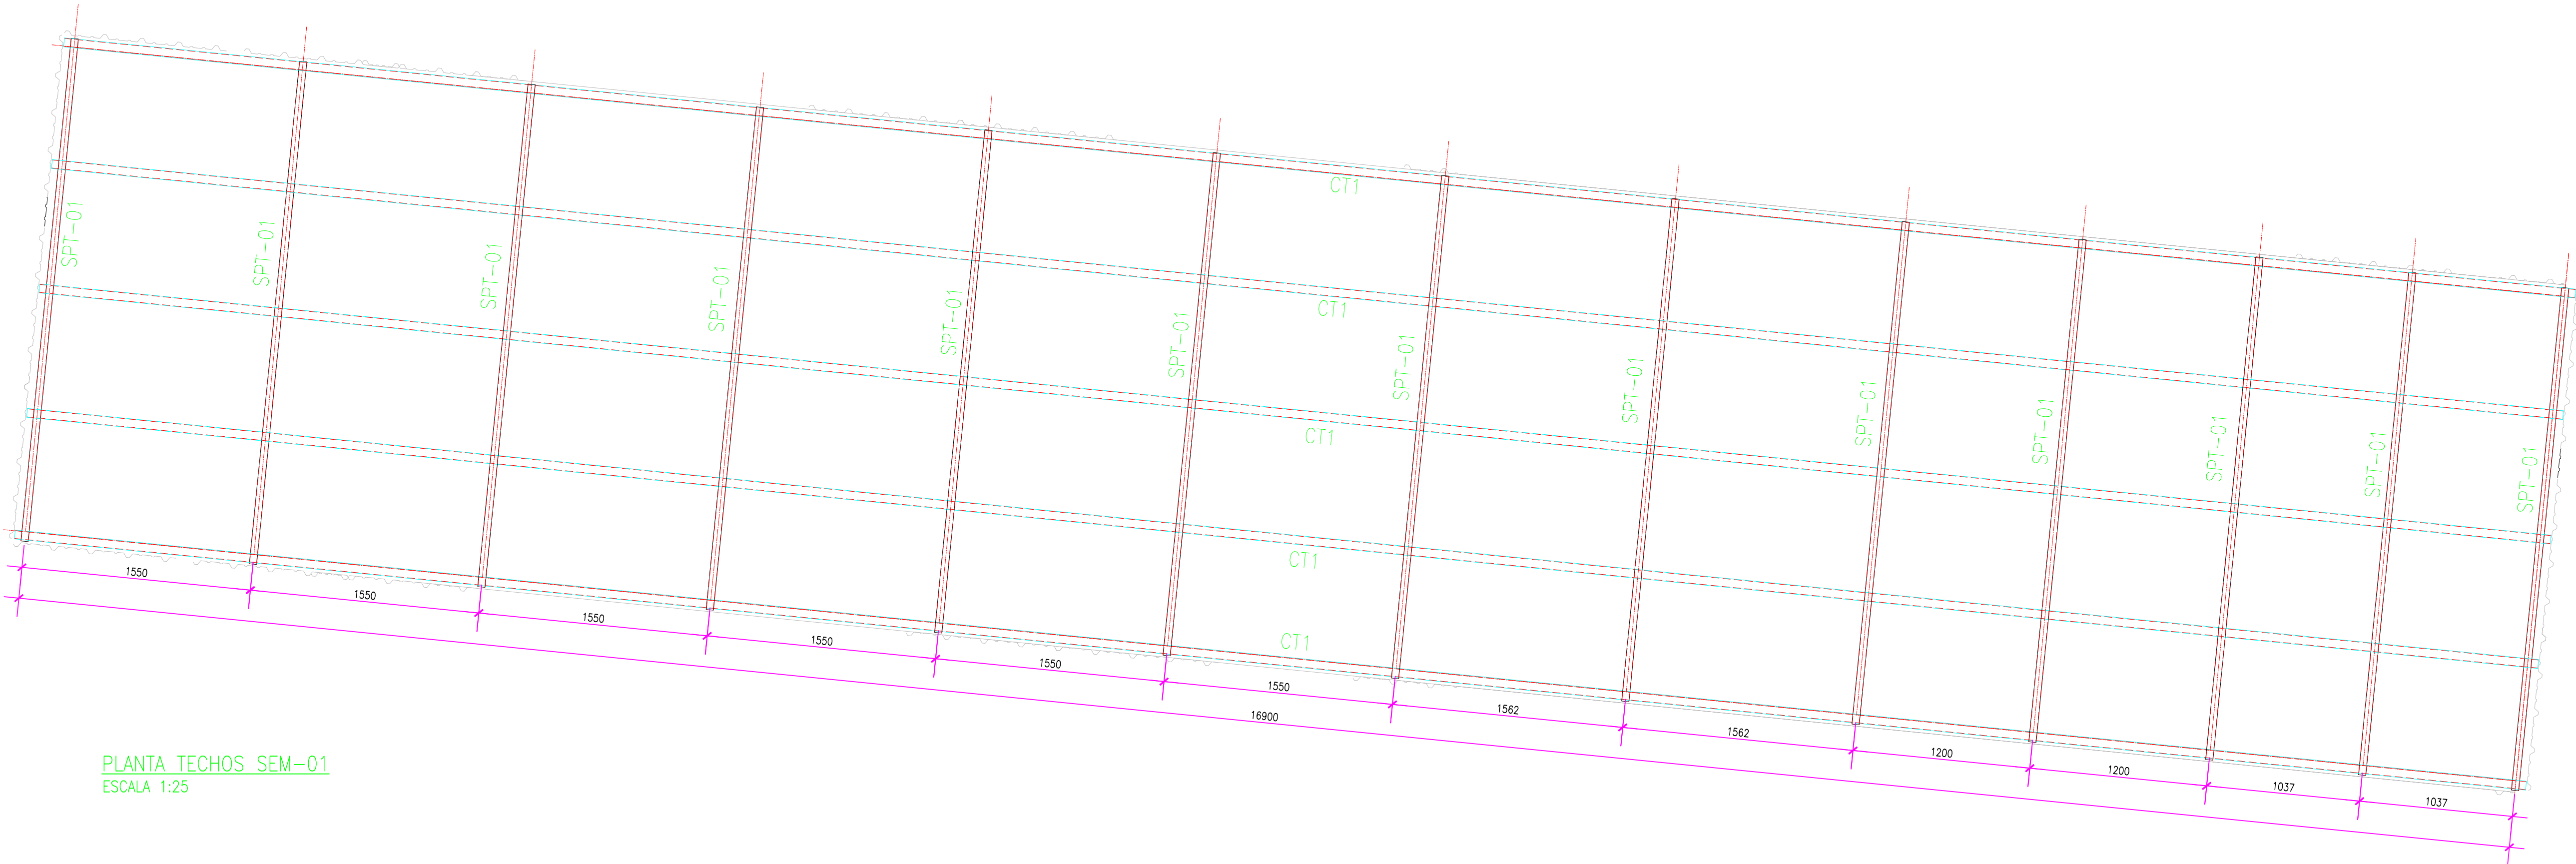

PLANTA TECHOS SEM-01
ESCALA 1:25

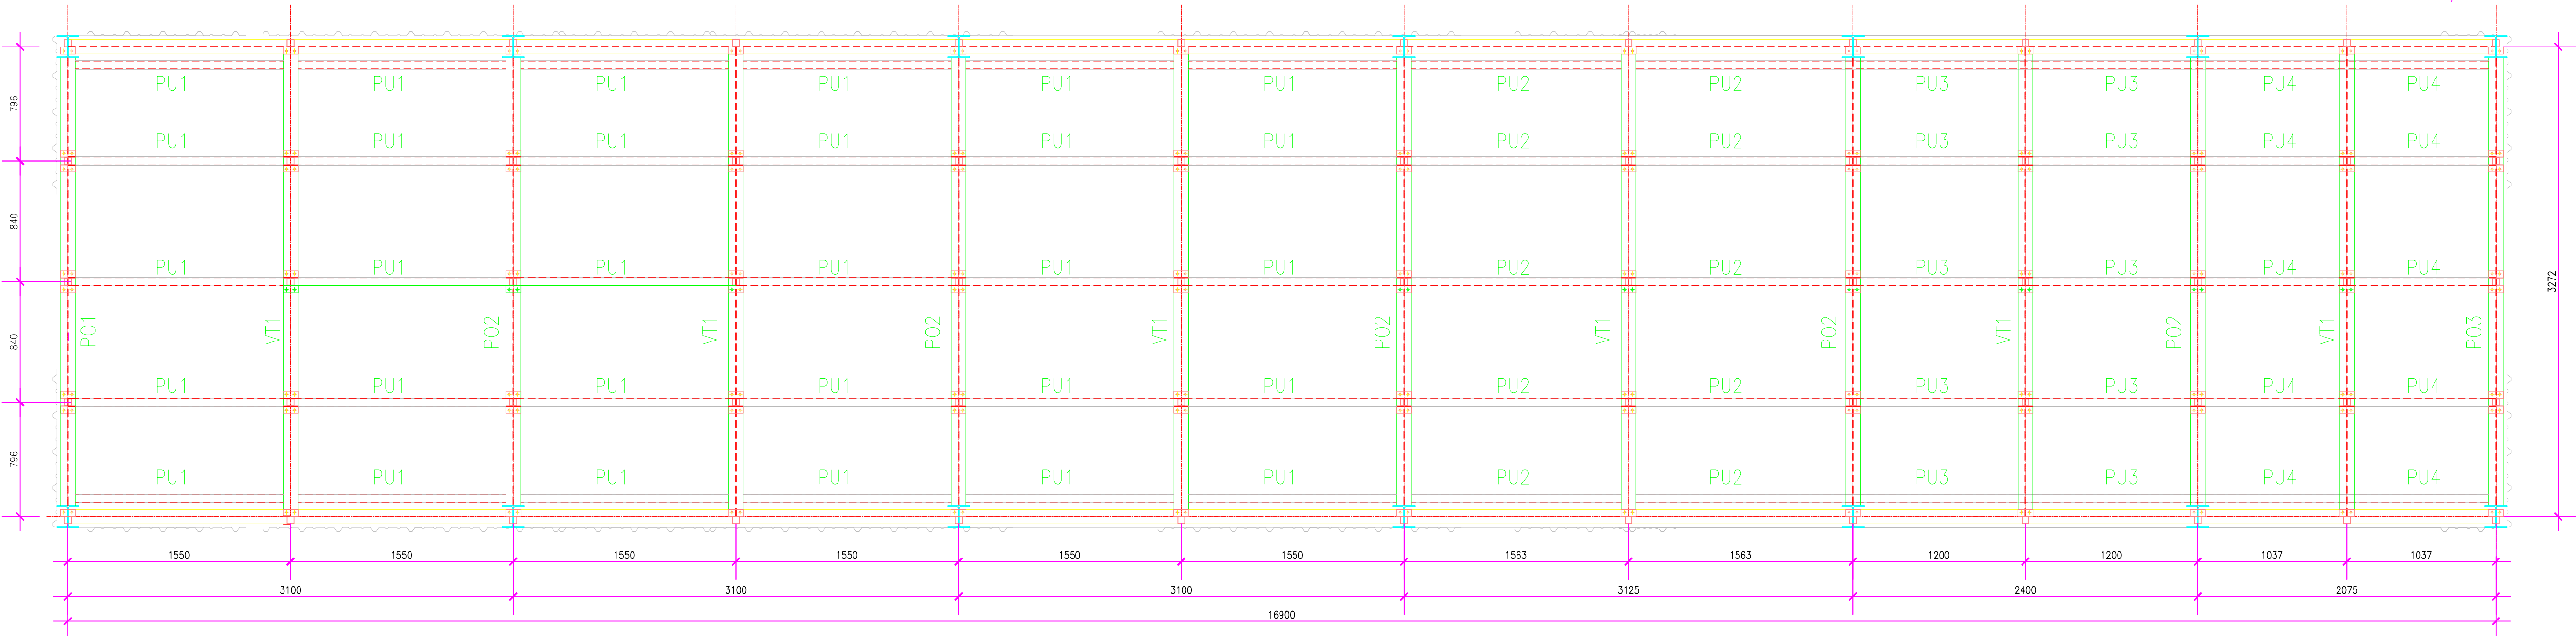

PLANTA PUNTALES SEM-01
ESCALA 1:25

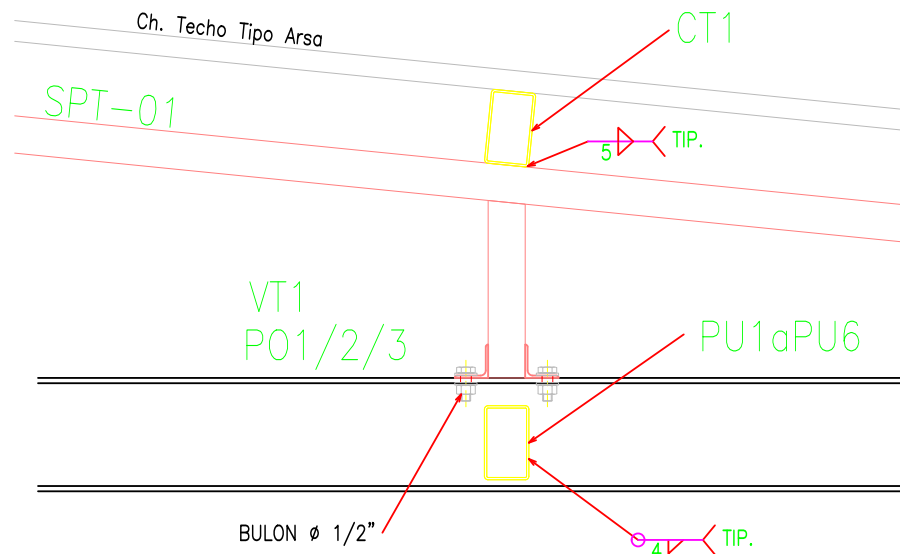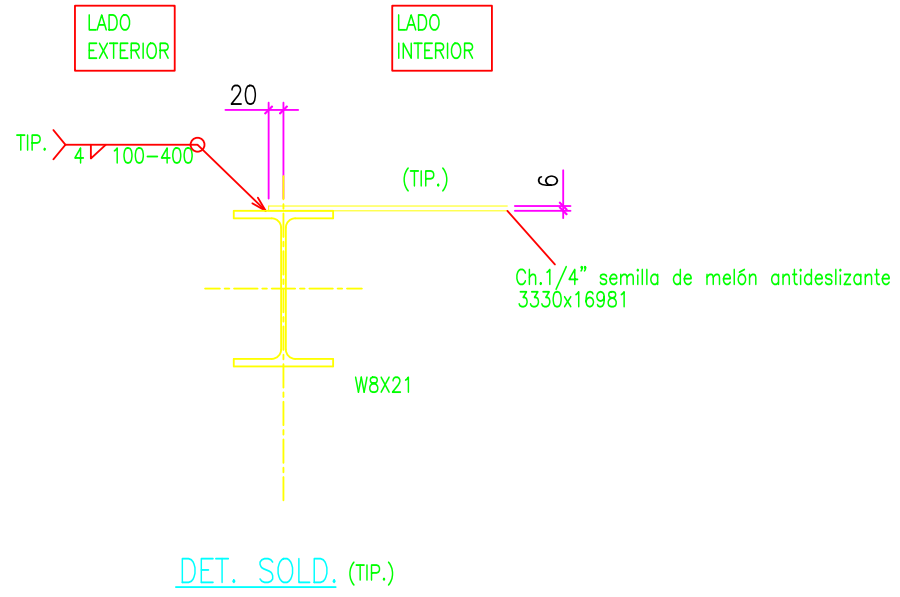

DET. 6
ESCALA 1:10


NOTAS:

- MEDIDAS EN mm
- CALIDAD PERFILES LAMINADOS W: ACERO F-36 o ASTM A-572 Gr50
- CALIDAD PERFILES LAMINADOS, CHAPAS y PLANCHUELAS: ACERO F-24
- CALIDAD BULONES ASTM A-325
- TODAS LAS SOLDADURAS SE REALIZARAN S/NORMA A.W.S. D1.1-96 Y SEGUN LA ESPECIFICACION DE PROCEDIMIENTO.


DOCUMENTOS DE REFERENCIA

- TE-631-104728-LY-C-1701 - LAYOUT GENERAL DE IMPLANTACIÓN SALAS (TAG: SEM-01 / SEM-02 / SEM-03)
- TE-631-104728-MC-C-1701 - MEMORIA DE CÁLCULOS SALAS SEM-01/02/03


0	15/12/2025	EMISIÓN PARA APROBACIÓN	AMB	RMP	JJA
REV.	FECHA	DESCRIPCIÓN	ELABORO	REVISO	APROBO
tgs			DIRECCIÓN DE OPERACIONES GERENCIA		
LUGAR: NEUQUÉN - PLANTA TRATAYÉN			TÍTULO: PLANO DE ESTRUCTURAS METÁLICAS MÓDULO N°1 (TAG: SEM-01)		
OBRA: SALAS ELÉCTRICAS PLANTA ESTABILIZADORA CONDENSADOS SLUG CATCHER - INGL ETAPA TEMPORARIA			FECHA: 15/12/25	OBRA N°: 104.728	ESCALA: 2 de 6
ESPACIO CONTRATISTA:			DOCUMENTO: TE-631-104728-PL-C-1701		
N° Doc. Ingeniería:			Rev:	REVISIÓN	
				0	

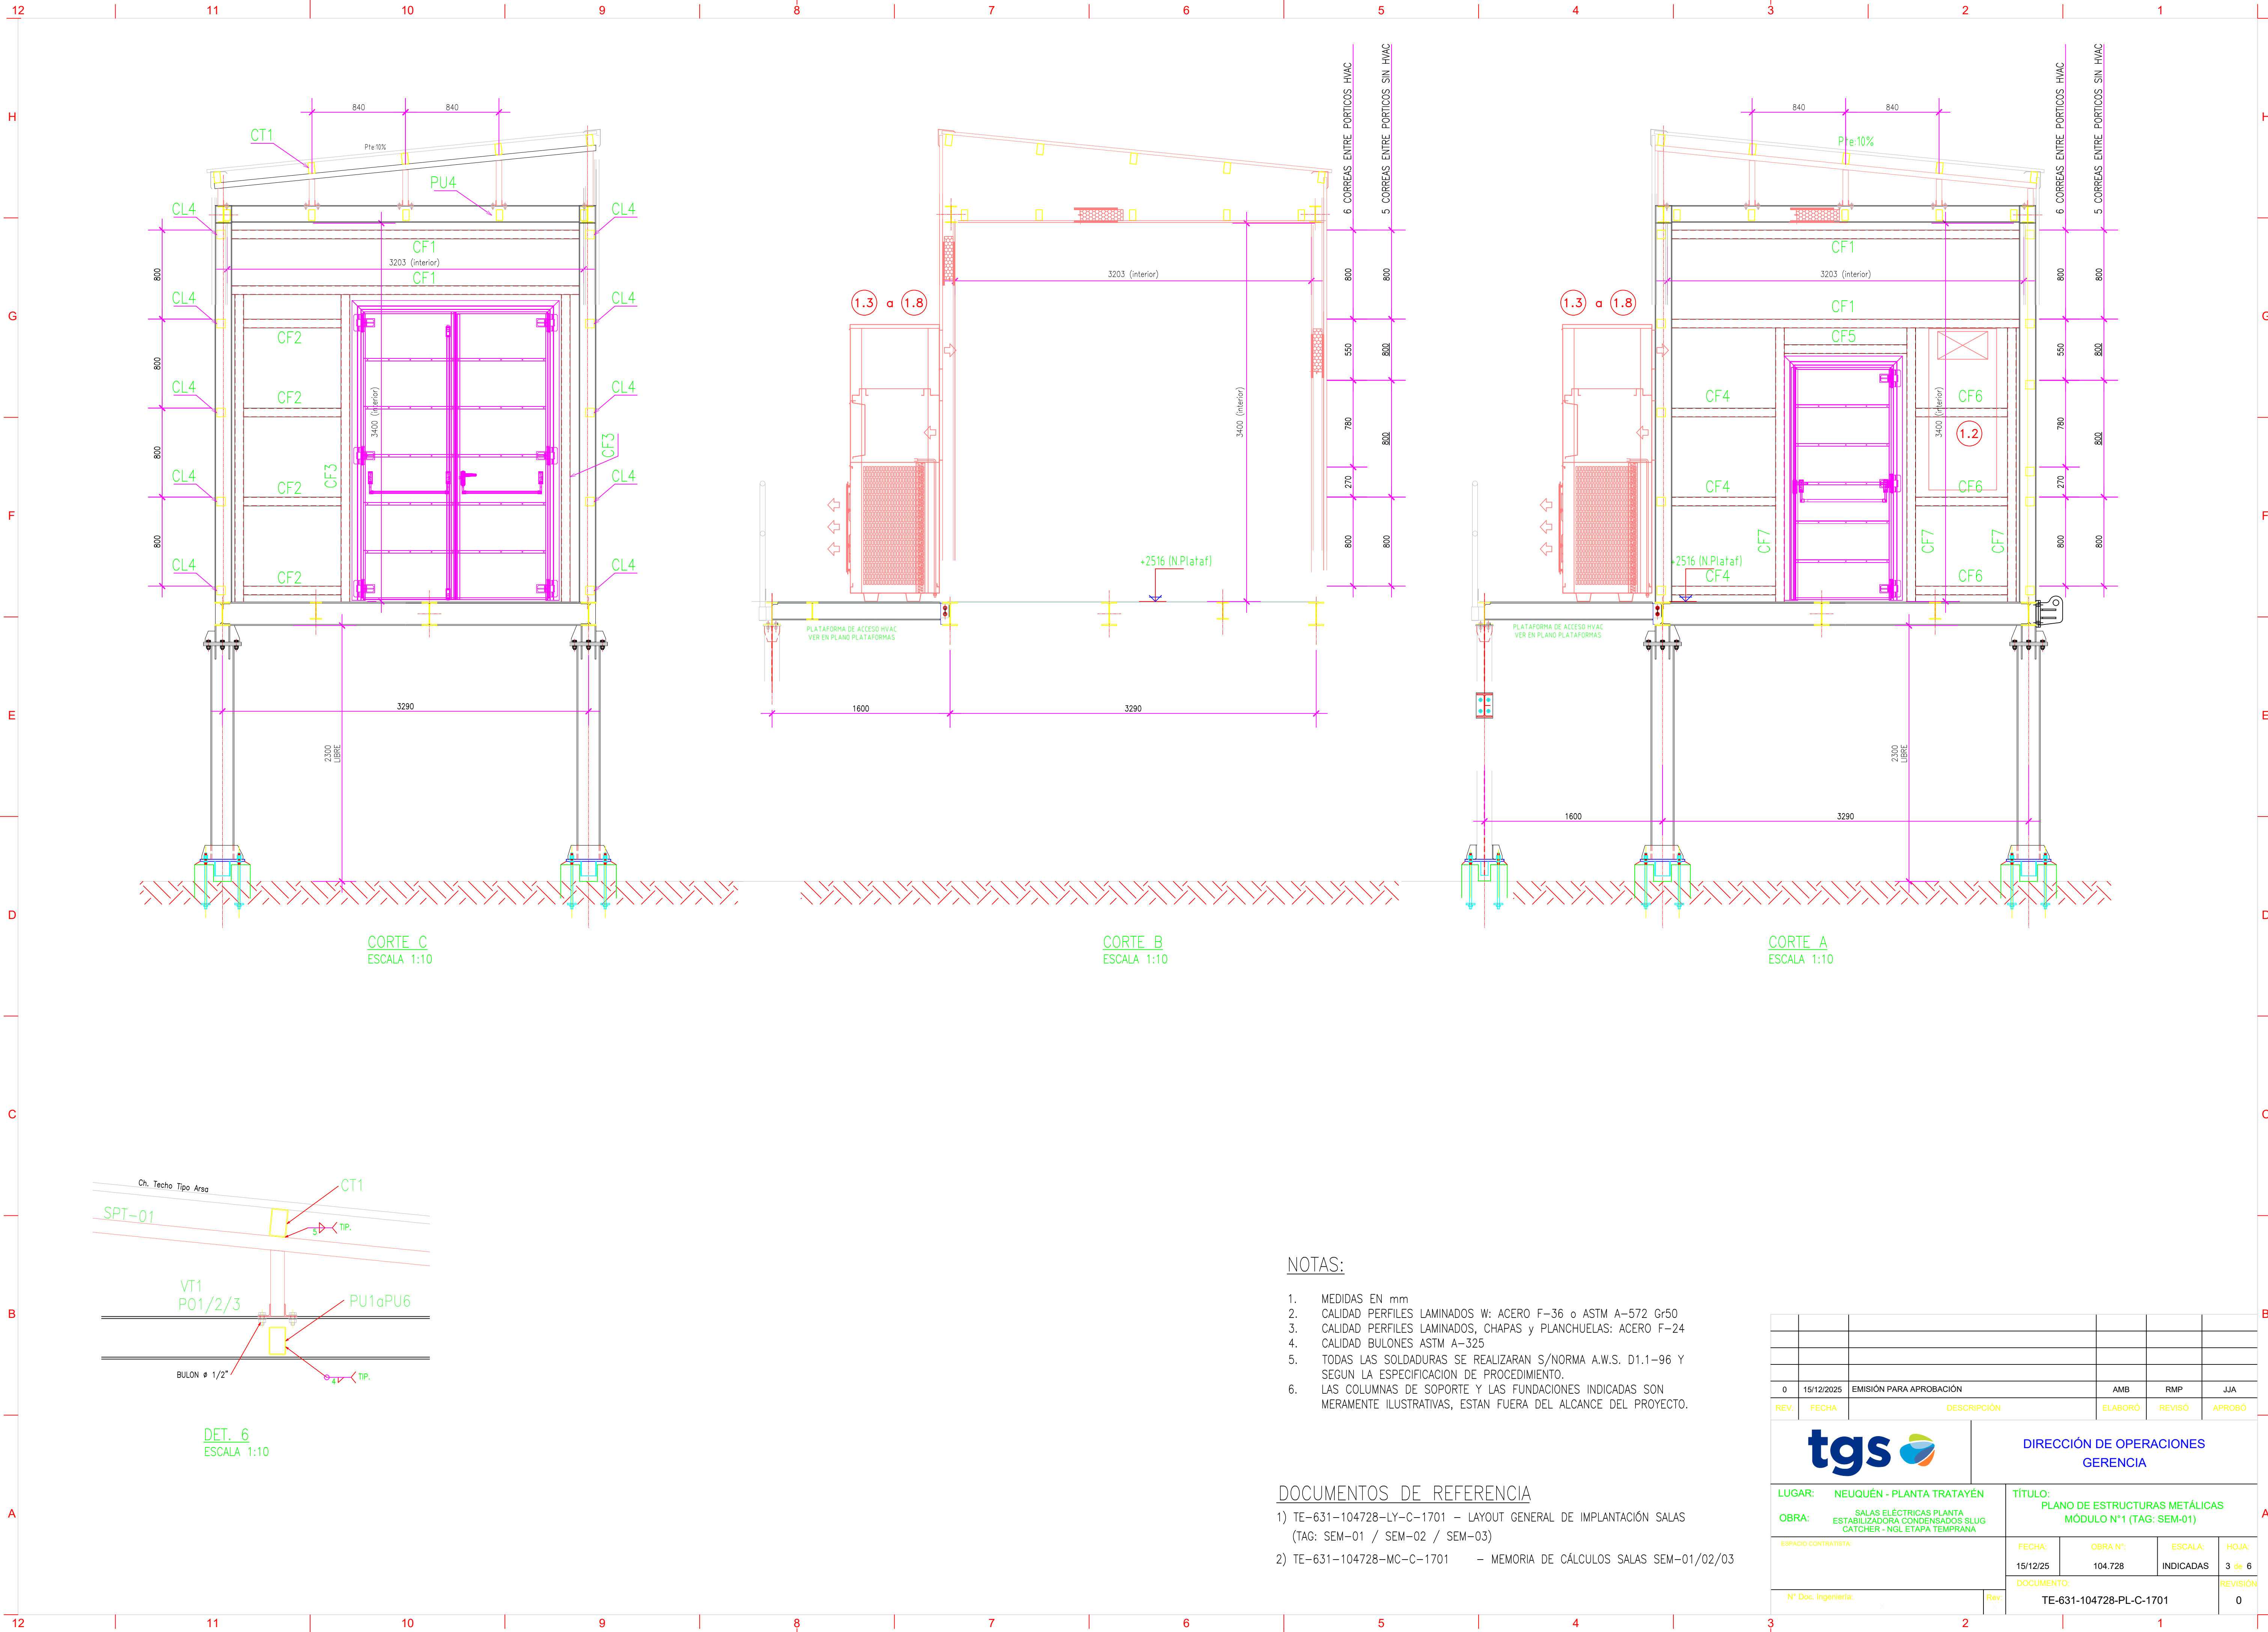


PLANTA PLATAFORMA PLT SEM-01
ESCALA 1:25

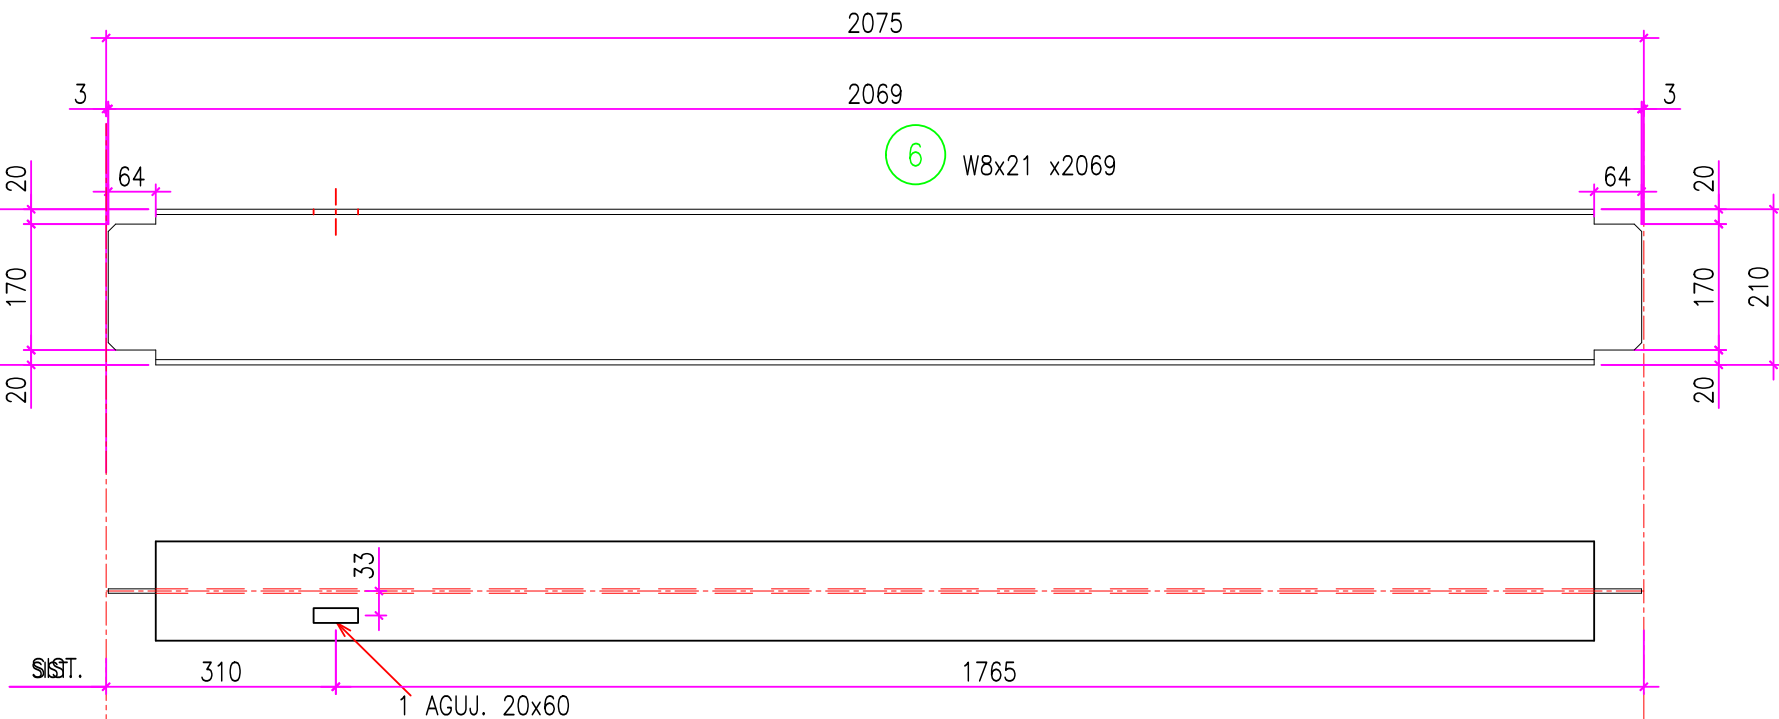


VIGA V8 CANT.: 1
ESC.: 1:10

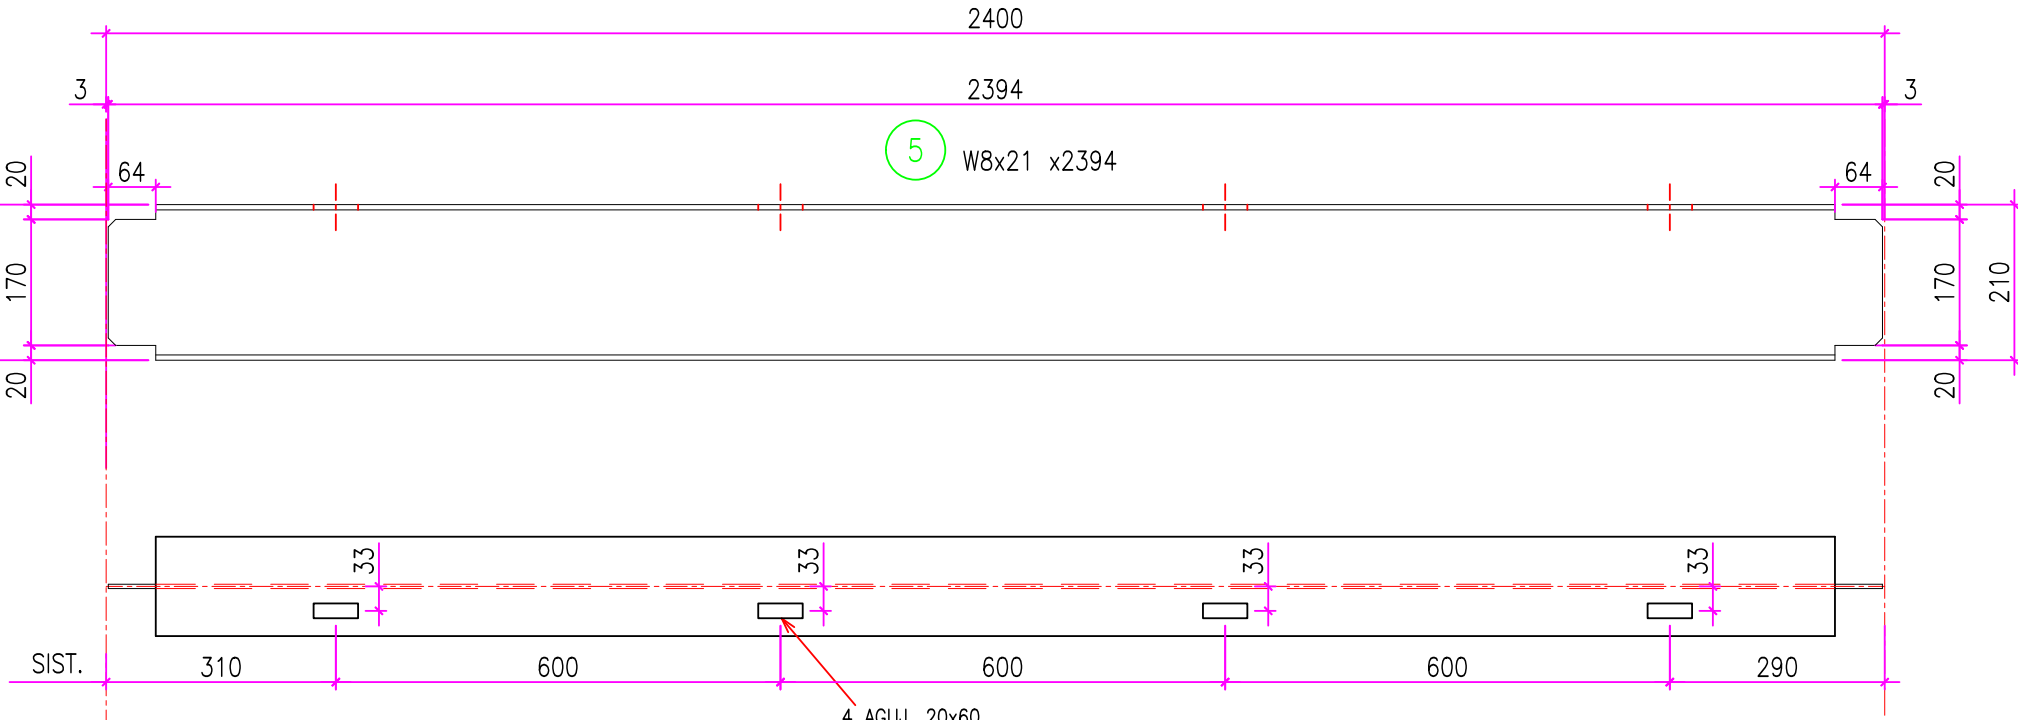


VIGA V7 CANT.: 1
ESC.: 1:10

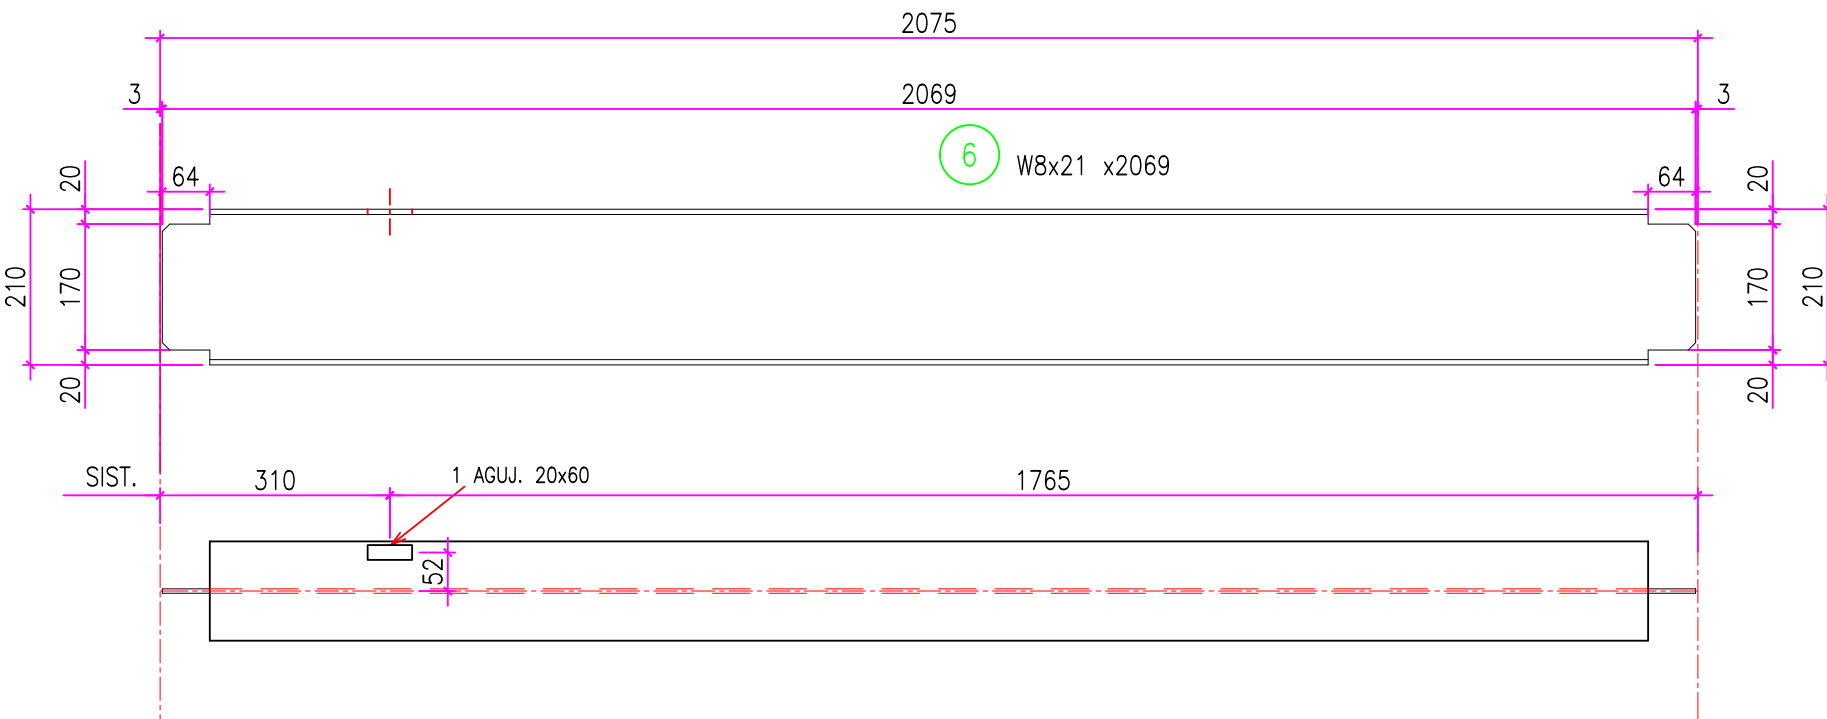

VIGA V11 CANT.: 1
ESC.: 1:10

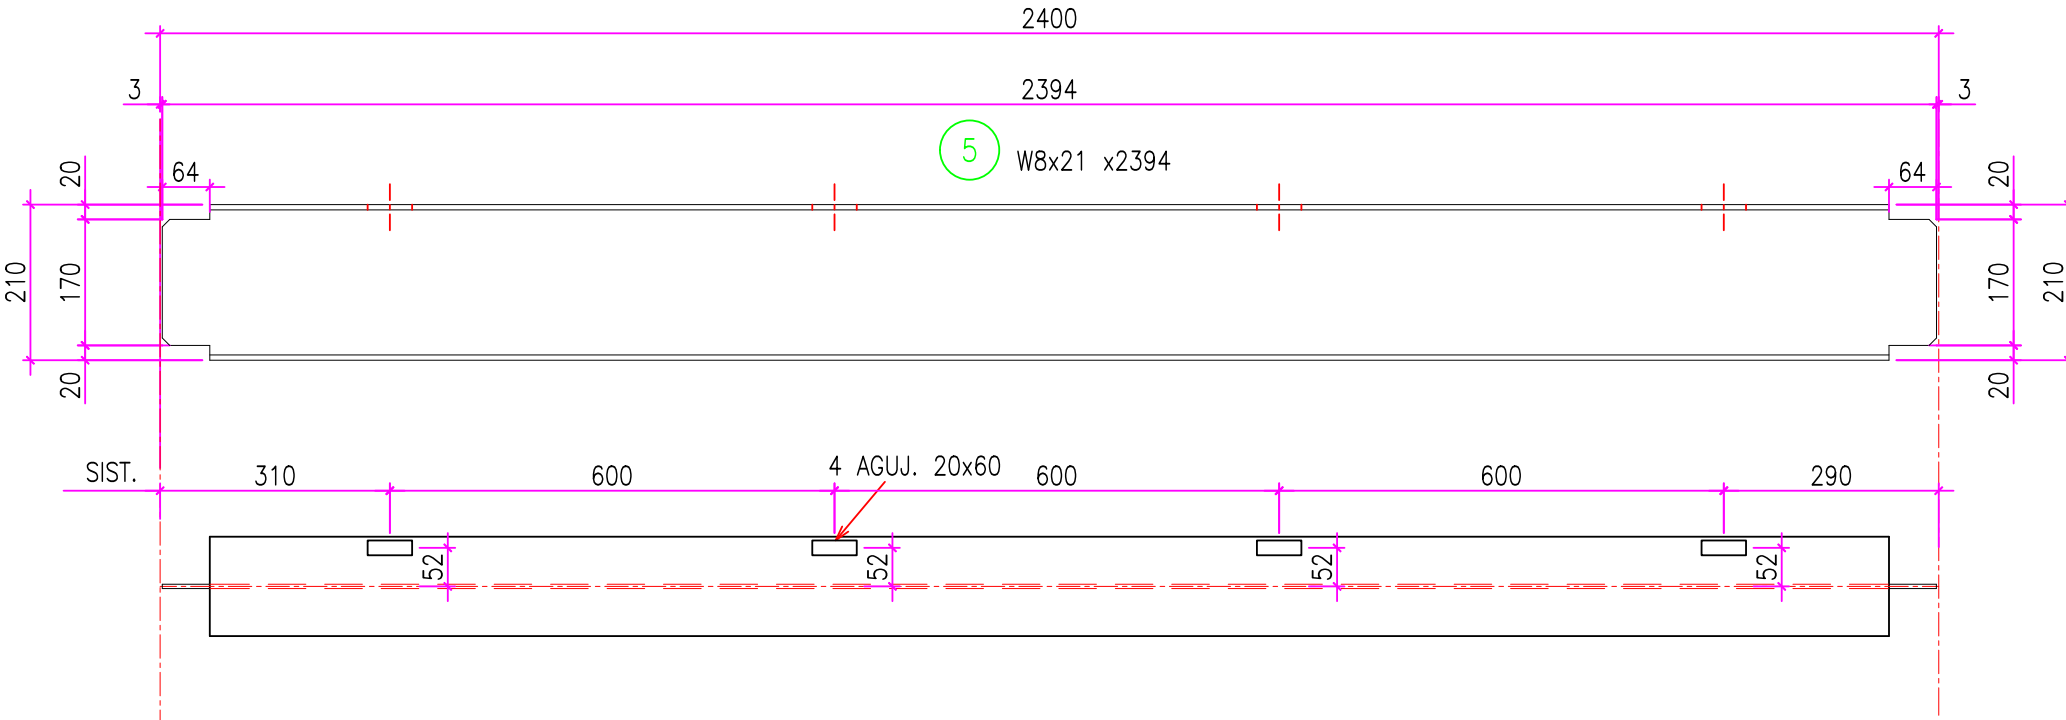

VIGA V10 CANT.: 1
ESC.: 1:10

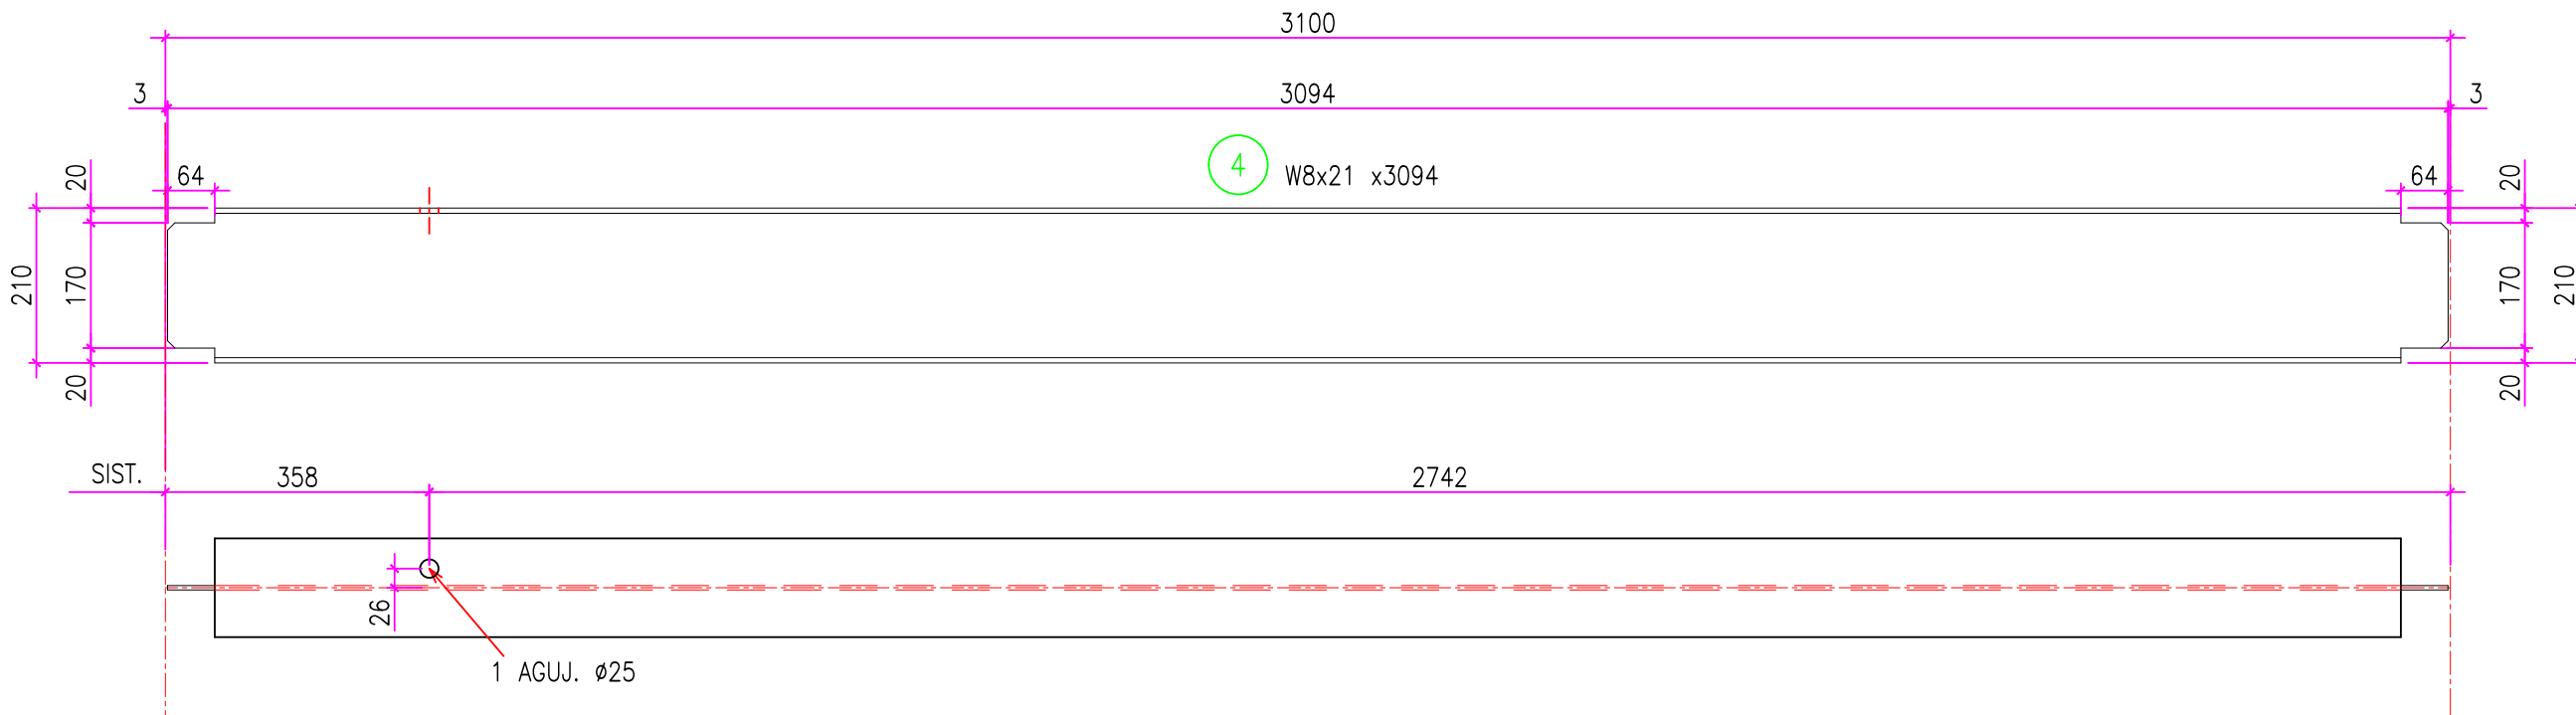


VIGA V5 CANT.: 3
ESC.: 1:10

NOTAS:


1. MEDIDAS EN mm
2. CALIDAD PERFILES LAMINADOS W: ACERO F-36 o ASTM A-572 Gr50
3. CALIDAD PERFILES LAMINADOS, CHAPAS y PLANCHUELAS: ACERO F-24
4. CALIDAD BULONES ASTM A-325
5. TODAS LAS SOLDADURAS SE REALIZARAN S/NORMA A.W.S. D1.1-96 Y SEGUN LA ESPECIFICACION DE PROCEDIMIENTO.

DOCUMENTOS DE REFERENCIA


- 1) TE-631-104728-LY-C-1701 - LAYOUT GENERAL DE IMPLANTACIÓN SALAS
(TAG: SEM-01 / SEM-02 / SEM-03)
- 2) TE-631-104728-MC-C-1701 - MEMORIA DE CÁLCULOS SALAS SEM-01/02/03

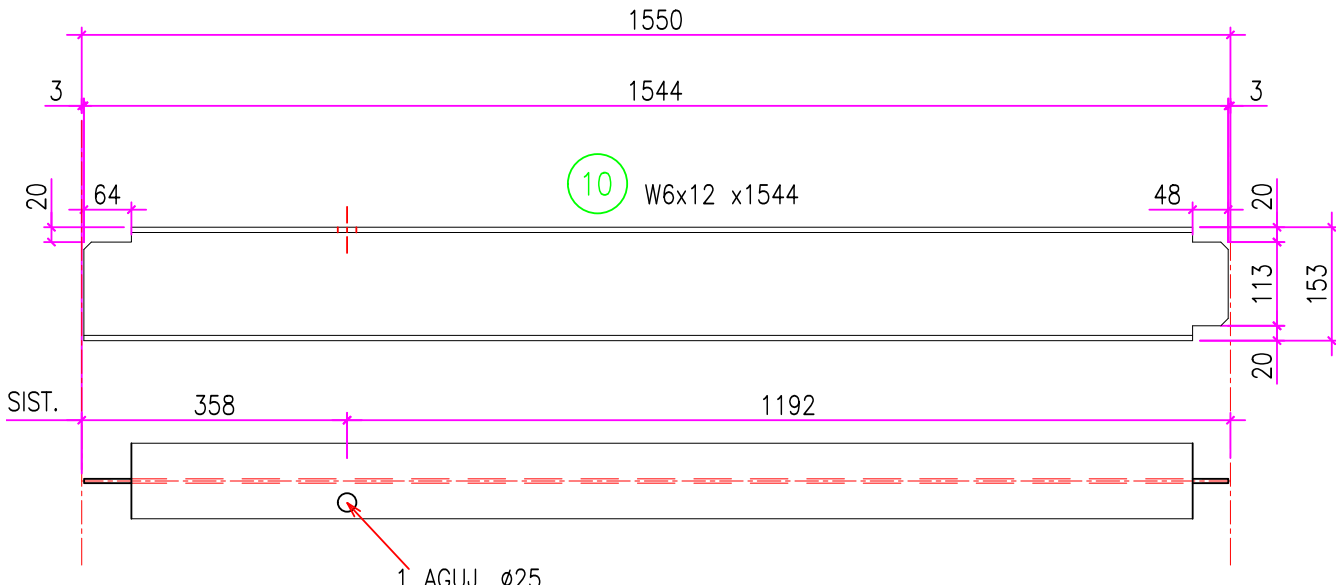


VIGA V3 CANT.: 3
ESC.: 1:10

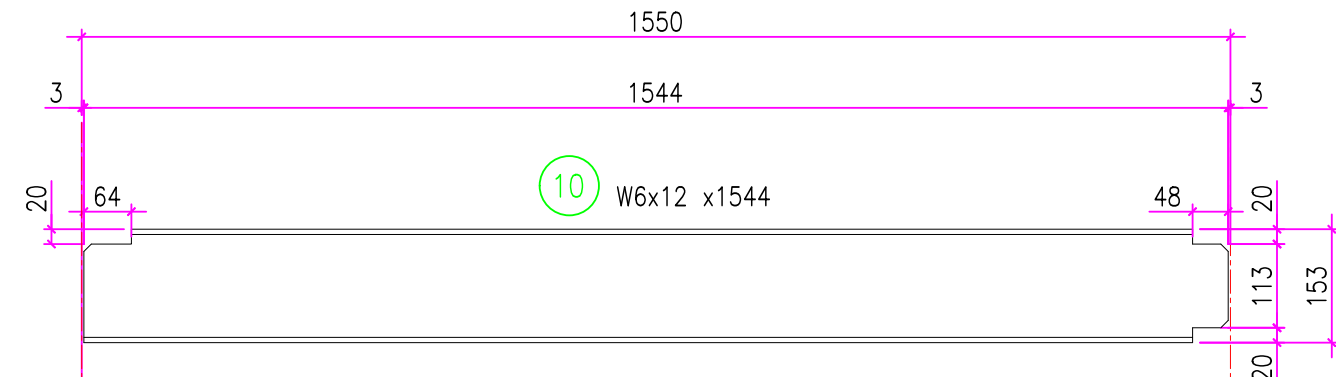


VIGA V4 CANT.: 3
ESC.: 1:10

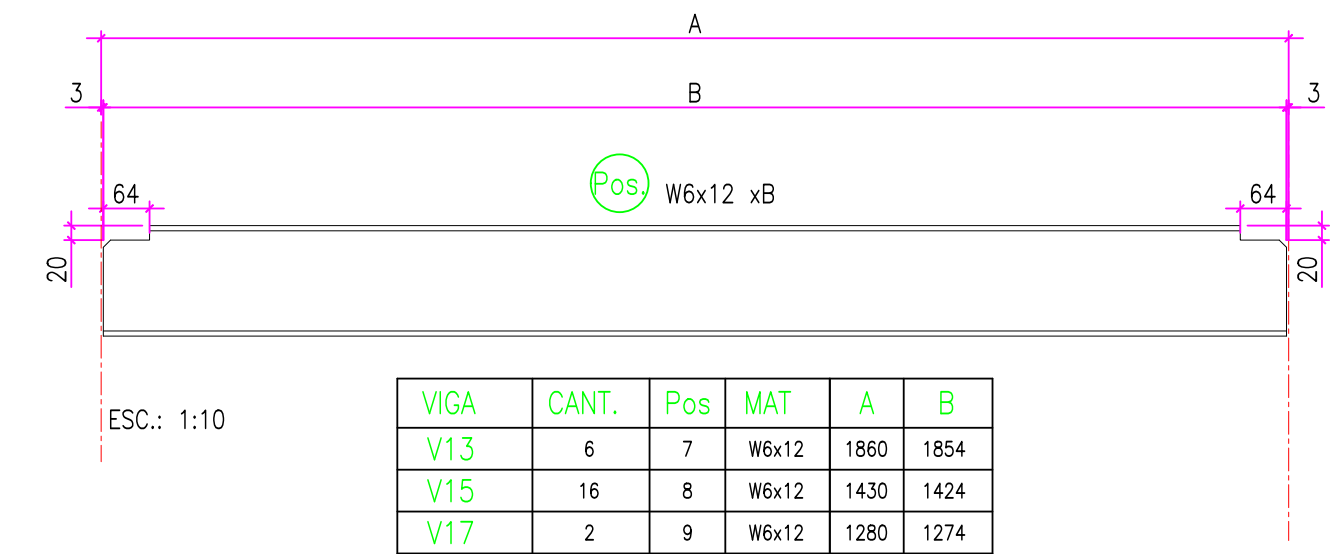


VIGA	CANT.	Pos	MAT	A	B
V13	6	7	W6x12	1960	1854
V15	16	8	W6x12	1430	1424
V17	2	9	W6x12	1280	1274

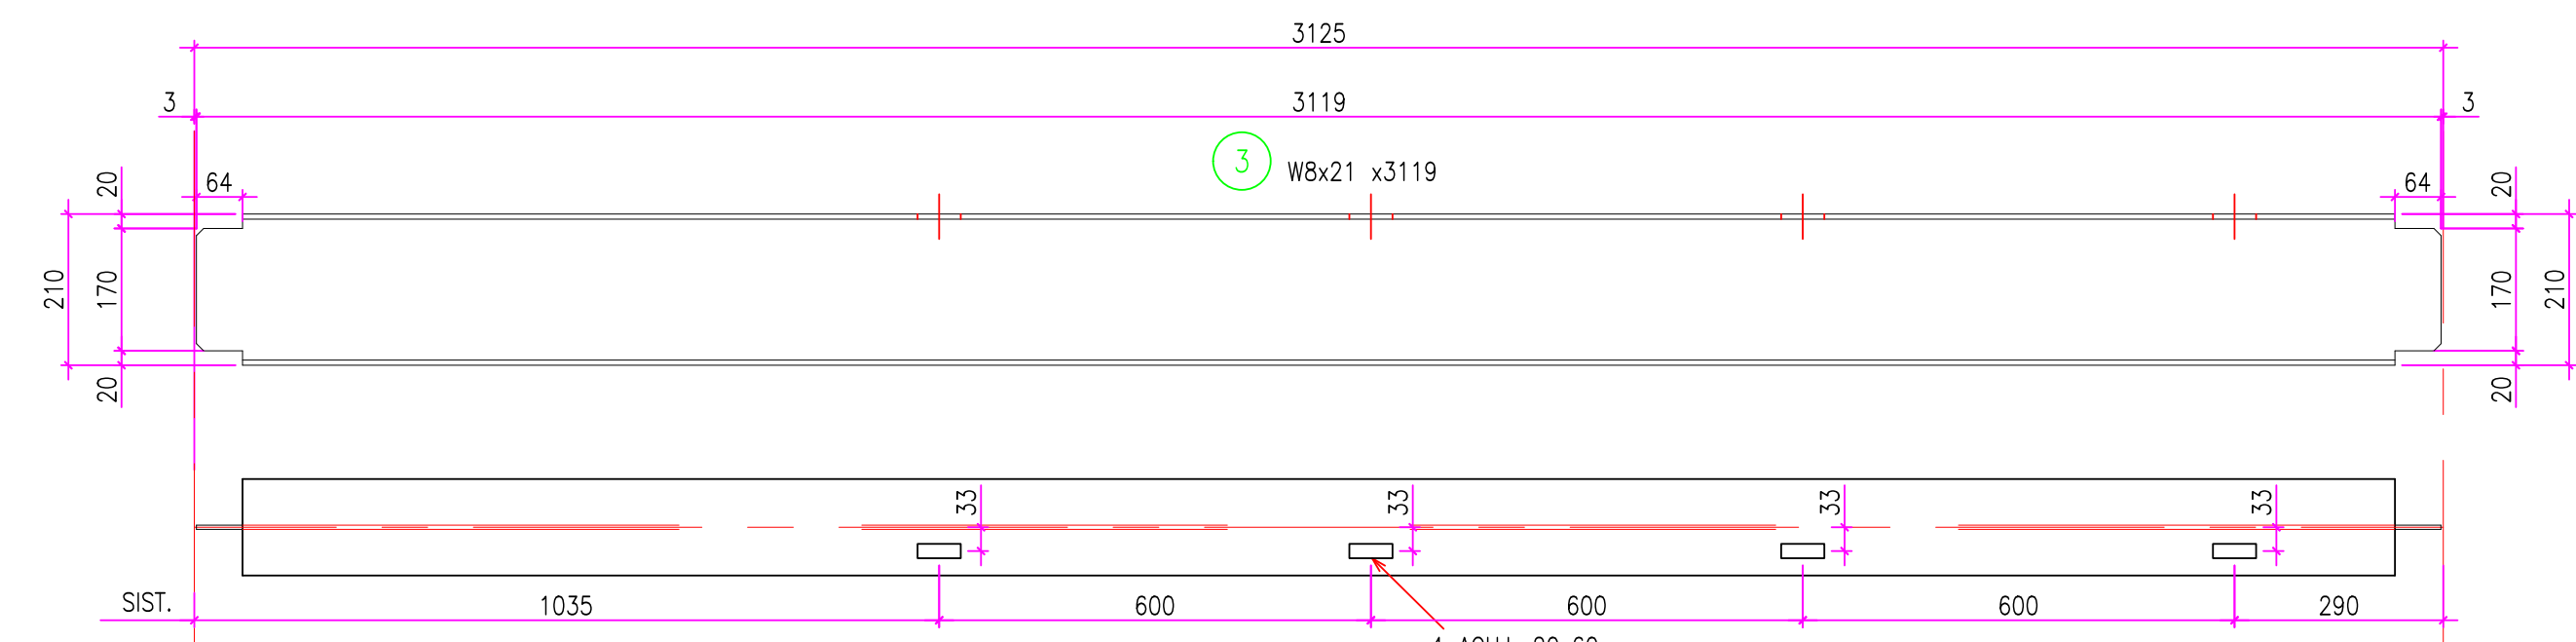


VIGA V6 CANT.: 1
ESC.: 1:10

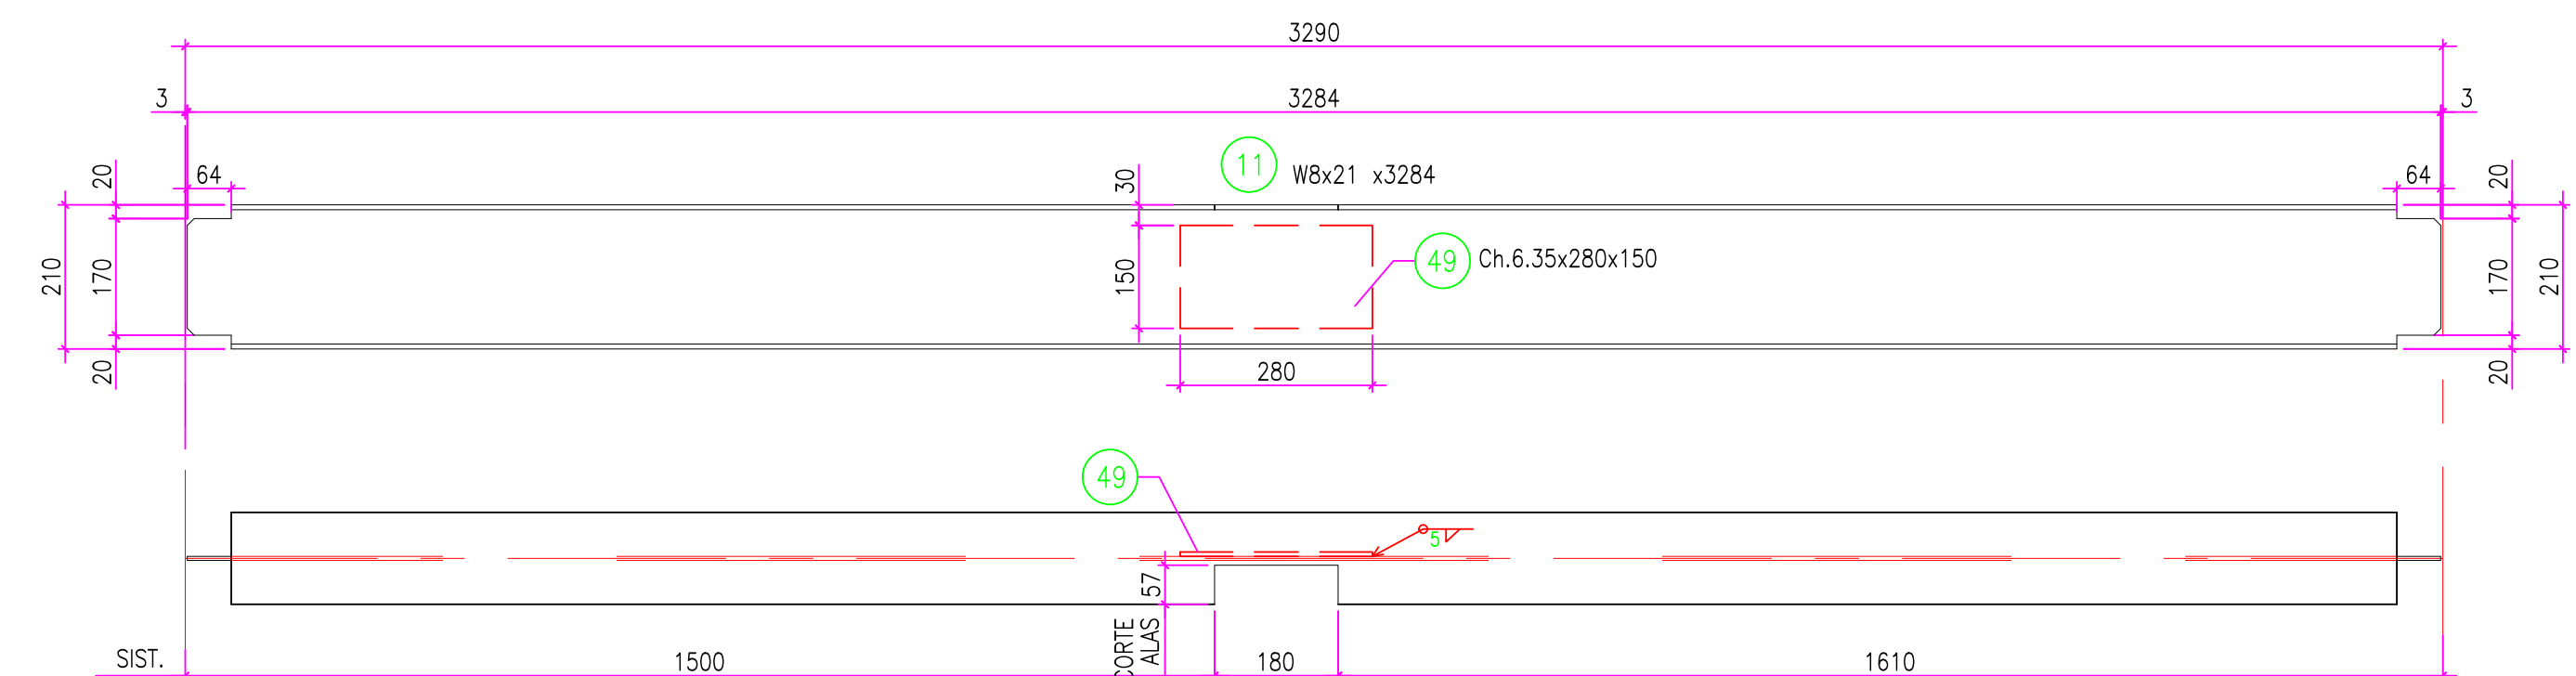

VIGA V16 CANT.: 2
ESC.: 1:10

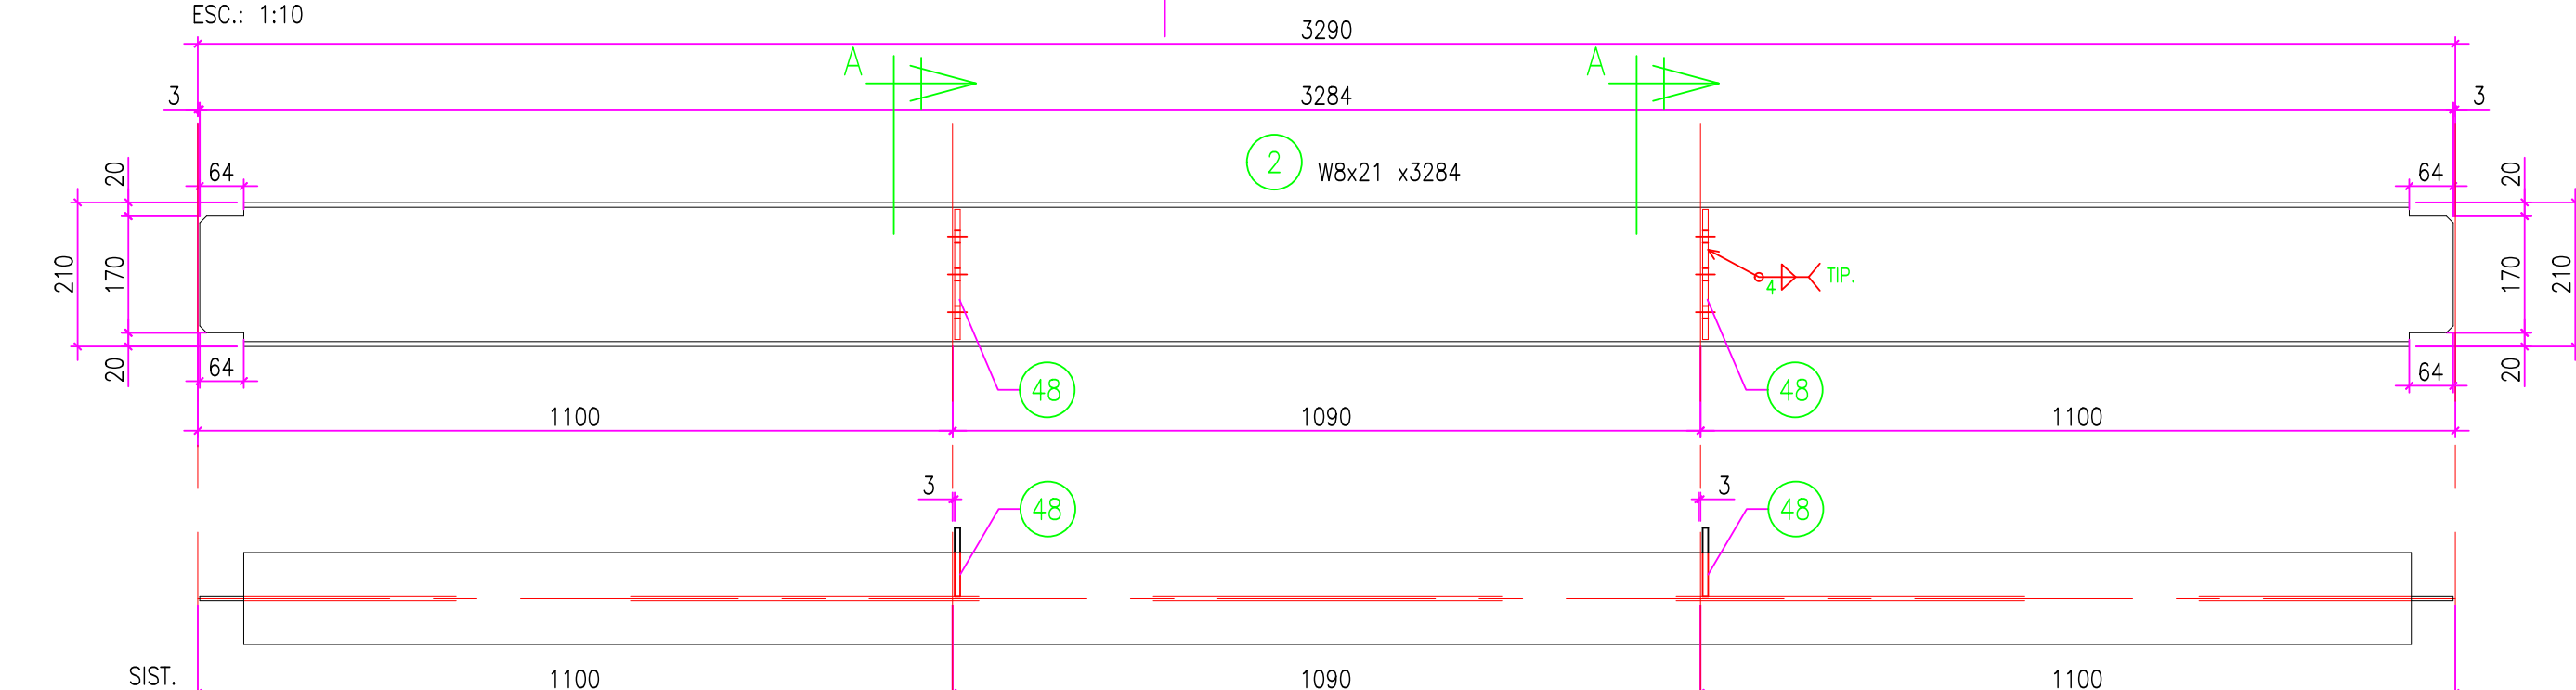


VIGA V12 CANT.: 1 (S/ DIBUJO)
VIGA V18 CANT.: 1 (MANO OPUESTA)
ESC.: 1:10

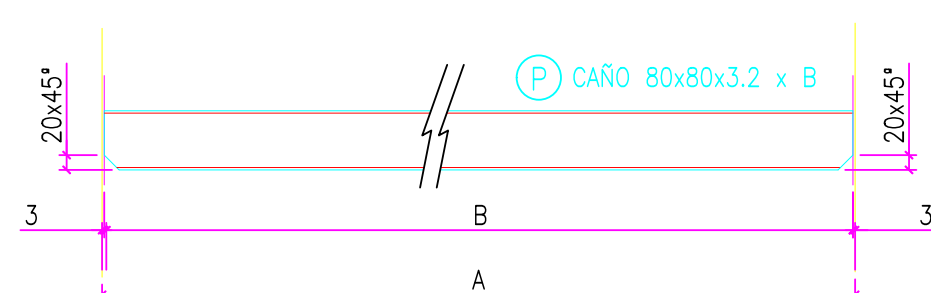


CORREA	CANT.	Pos	MAT	A	B
CL1	36	21	CAÑO 80x80x3.2	3100	3094
CL2	10	22	CAÑO 80x80x3.2	3125	3119
CL3	10	23	CAÑO 80x80x3.2	2400	2394
CL4	10	24	CAÑO 80x80x3.2	2075	2069

CORREAS LATERALES
ESCALA 1:10

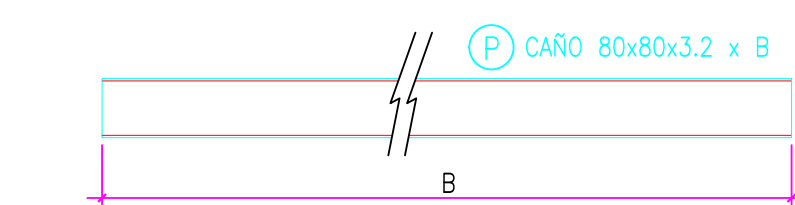


CORREA	CANT.	Pos	MAT.	B
CF1	4	25	CAÑO 80x80x3,2	3120
CF2	4	26	CAÑO 80x80x3,2	874
CF3	2	27	CAÑO 80x80x3,2	2760
CF4	3	28	CAÑO 80x80x3,2	930
CF5	1	29	CAÑO 80x80x3,2	1100
CF6	3	30	CAÑO 80x80x3,2	824
CF7	3	31	CAÑO 80x80x3,2	260

CORREAS FRONTIS
ESCALA 1:10

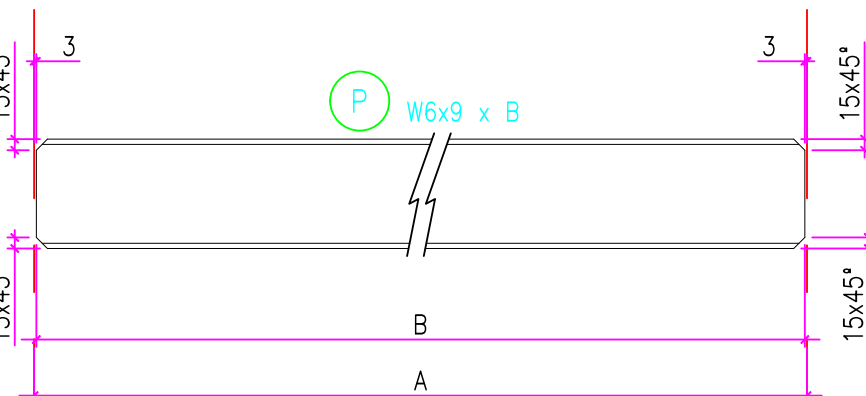


VIGA	CANT.	Pos	MAT	A	B
VL1	2	12	W6x9	3100	3094
VL2	2	13	W6x9	3125	3119
VL3	2	14	W6x9	2400	2394
VL4	2	15	W6x9	2075	2069

VIGAS LONGITUDINALES VL

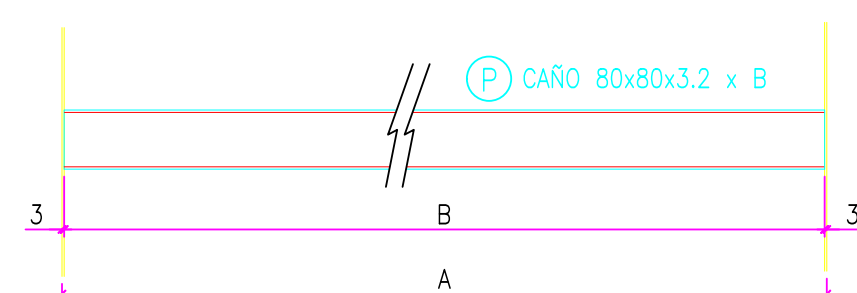


PUNTA	CANT.	Pos	MAT.	A	B
PU1	30	16	CAÑO 100x60x3.2	1550	1544
PU2	10	17	CAÑO 100x60x3.2	1563	1557
PU3	10	18	CAÑO 100x60x3.2	1200	1194
PU4	10	19	CAÑO 100x60x3.2	1037	1031

PUNTALES PU
ESCALA 1:10

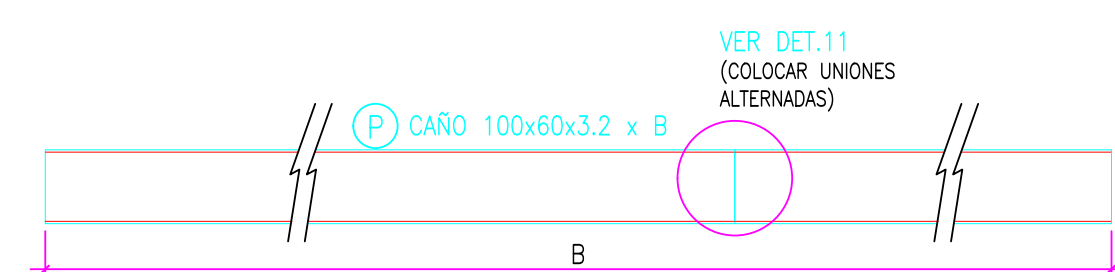


CORREA	CANT.	Pos	MAT.	B
CT1	5	20	CAÑO 100x60x3.2	17040


CORREAS TECHO
ESCALA 1:10

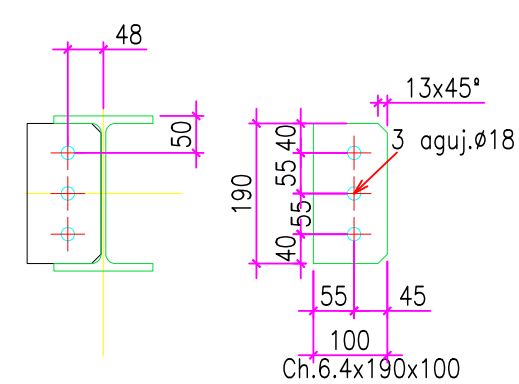


CORTE A

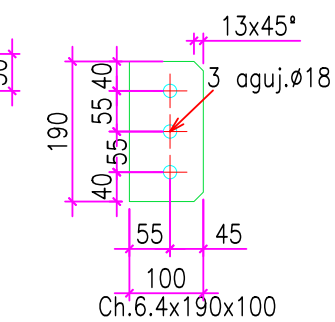


DET.POS 48 CANT.:13
ESC.1:10

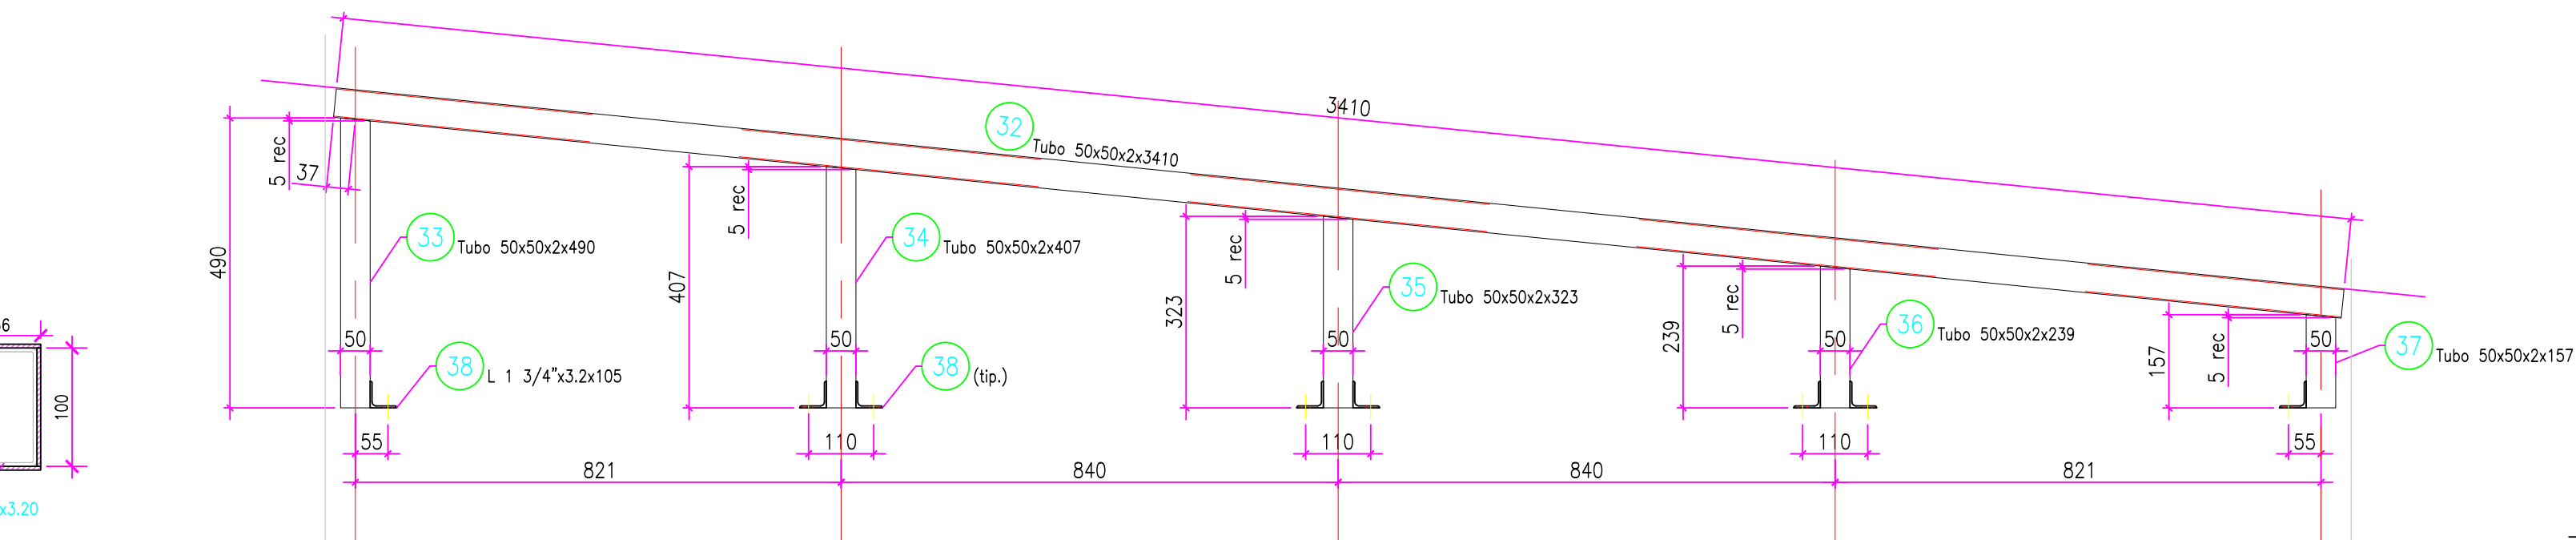

DET. SOPORTE TECHO SPT-01 (CANT.13)
ESC. 1:10

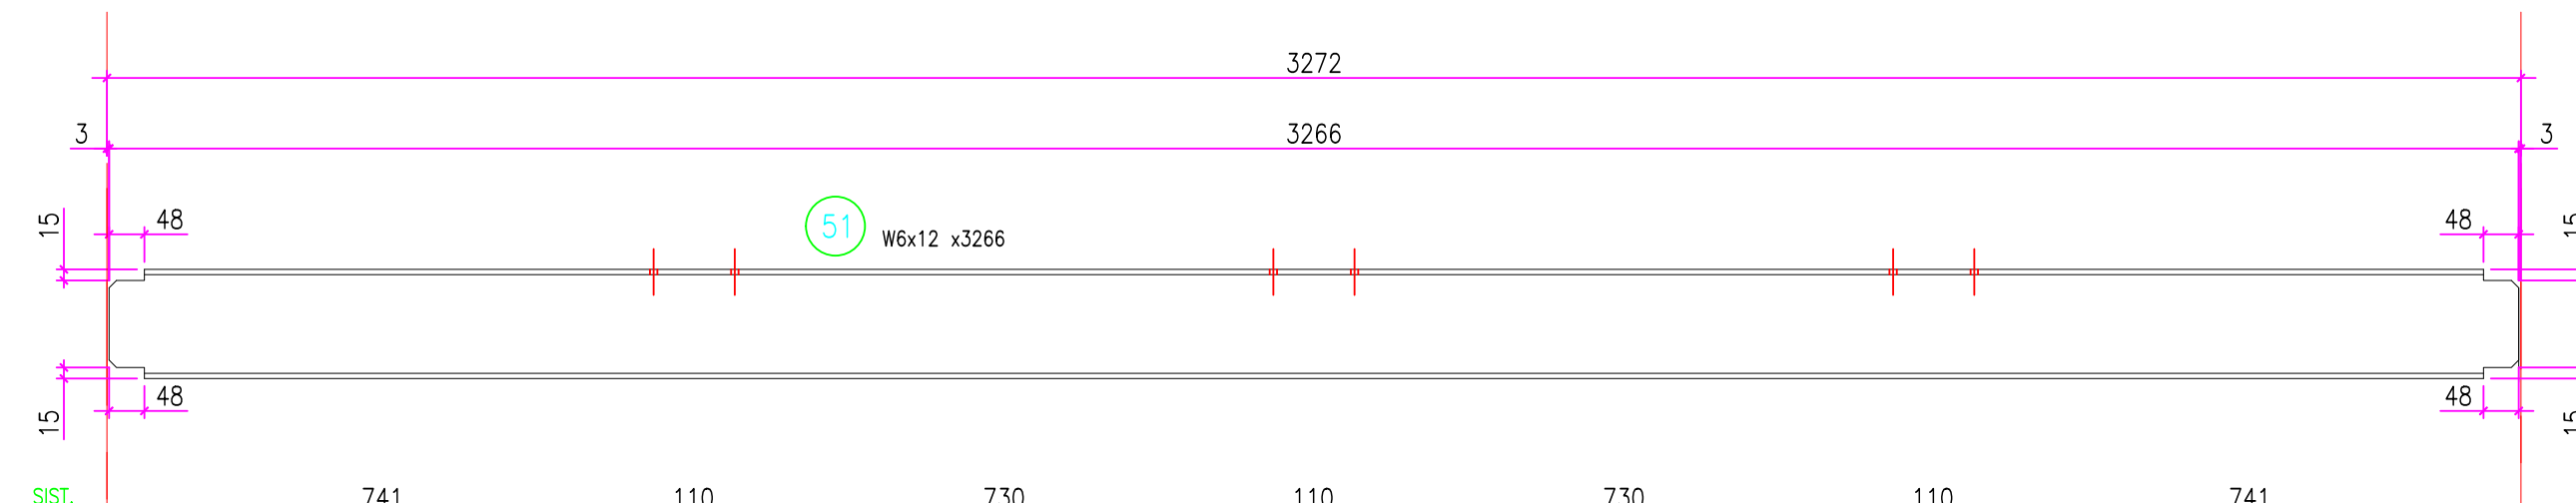

VIGA VT1 CANT.: 6
ESC.: 1:10

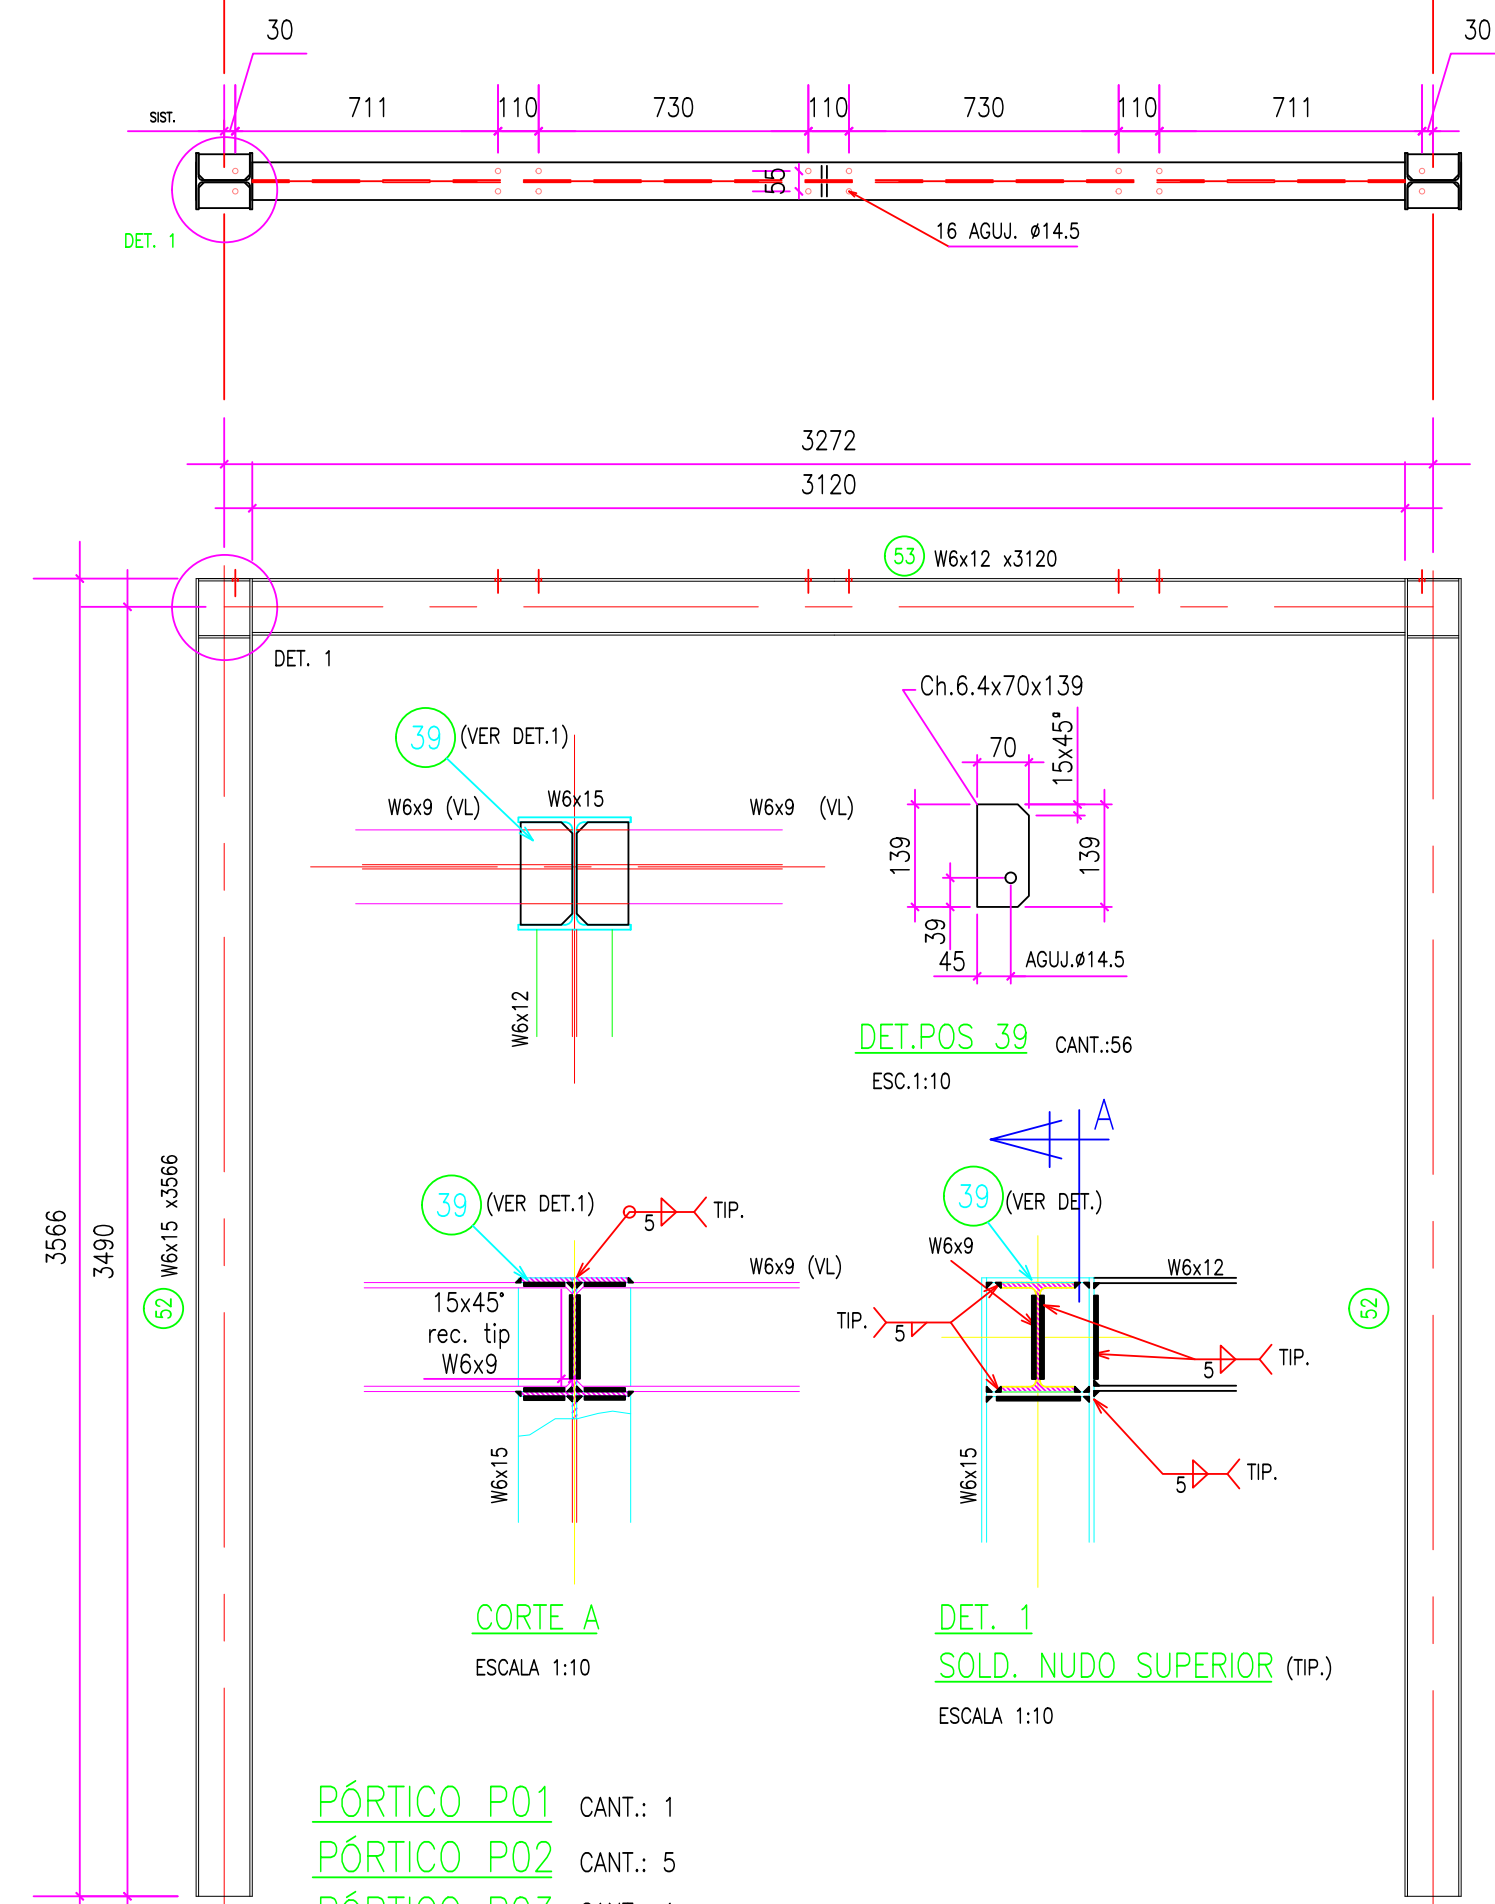

PÓRTICO P01 CANT.: 1
PÓRTICO P02 CANT.: 5
PÓRTICO P03 CANT.: 1
ESC.1:20

NOTAS:

1. MEDIDAS EN mm
2. CALIDAD PERFILES LAMINADOS W: ACERO F-36 o ASTM A-572 Gr50
3. CALIDAD PERFILES LAMINADOS, CHAPAS y PLANCHUELAS: ACERO F-24
4. CALIDAD BULONES ASTM A-325
5. TODAS LAS SOLDADURAS SE REALIZARAN S/NORMA A.W.S. D1.1-96 Y SEGUN LA ESPECIFICACION DE PROCEDIMIENTO.

DOCUMENTOS DE REFERENCIA

- 1) TE-631-104728-LY-C-1701 - LAYOUT GENERAL DE IMPLANTACIÓN SALAS
(TAG: SEM-01 / SEM-02 / SEM-03)
- 2) TE-631-104728-MC-C-1701 - MEMORIA DE CÁLCULOS SALAS SEM-01/02/03

0	15/12/2025	EMISIÓN PARA APROBACIÓN		AMB	RMP	JJA
REV.	FECHA	DESCRIPCIÓN		ELABORO	REVISO	APROBO
tgs			DIRECCIÓN DE OPERACIONES GERENCIA			
LUGAR: NEQUÉN - PLANTA TRATAYÉN			TÍTULO: PLANO DE ESTRUCTURAS METÁLICAS MÓDULO N°1 (TAG- SEM-01)			
OBRA: SALAS ELÉCTRICAS PLANTA ESTABILIZADORA CONDENSADOS SLUG CATCHER - NGL ETAPA TEMPORANA						
ESPACIO CONTRATISTA			FECHA: 15/12/25	OBRA N°: 104.728	ESCALA: INDICADAS	HOJA: 6 de 6
N° Doc. Ingeniería:			Rev:	DOCUMENTO: TE-631-104728-PL-C-1701		REVISIÓN: 0