




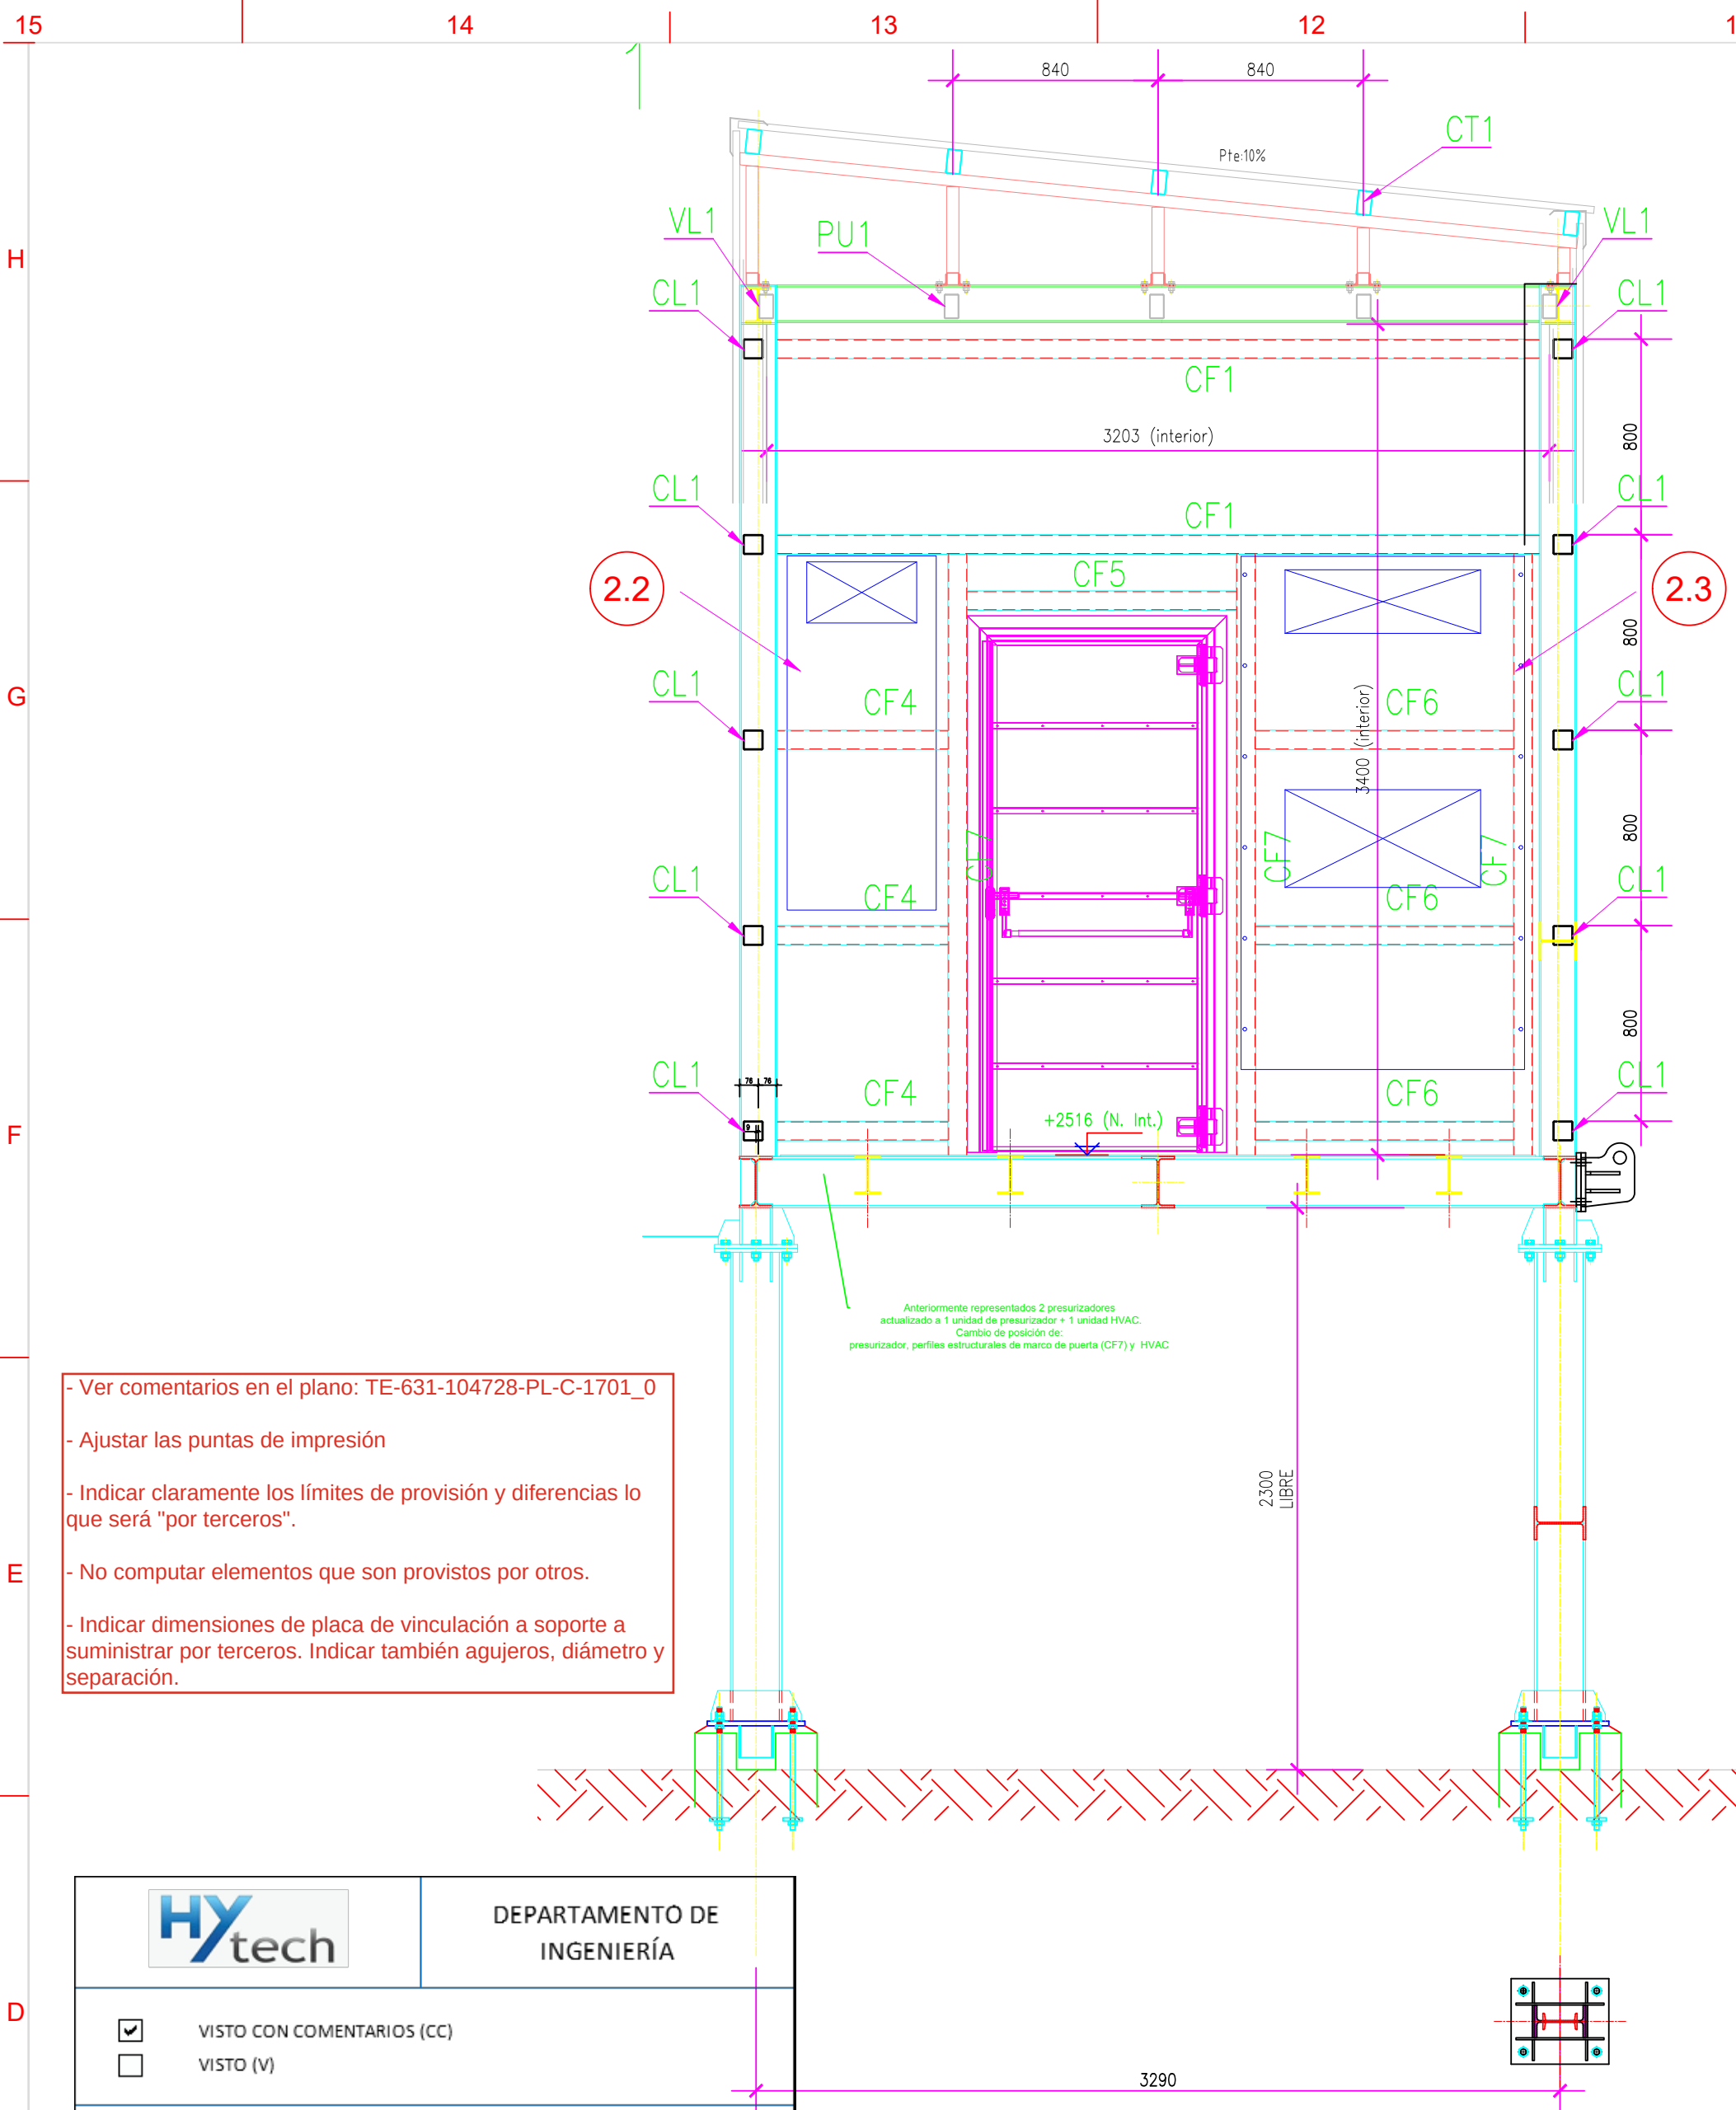


HYtech		DEPARTAMENTO DE INGENIERÍA	
☒	VISTO CON COMENTARIOS (CC)		
☐	VISTO (V)		
JUD	HYTECH INGENIERÍA S.A.	20/01/2026	
FIRMA/INICIALES	ACLARACIÓN	FECHA	


CORTE A-A SEM-02
ESCALA 1:25

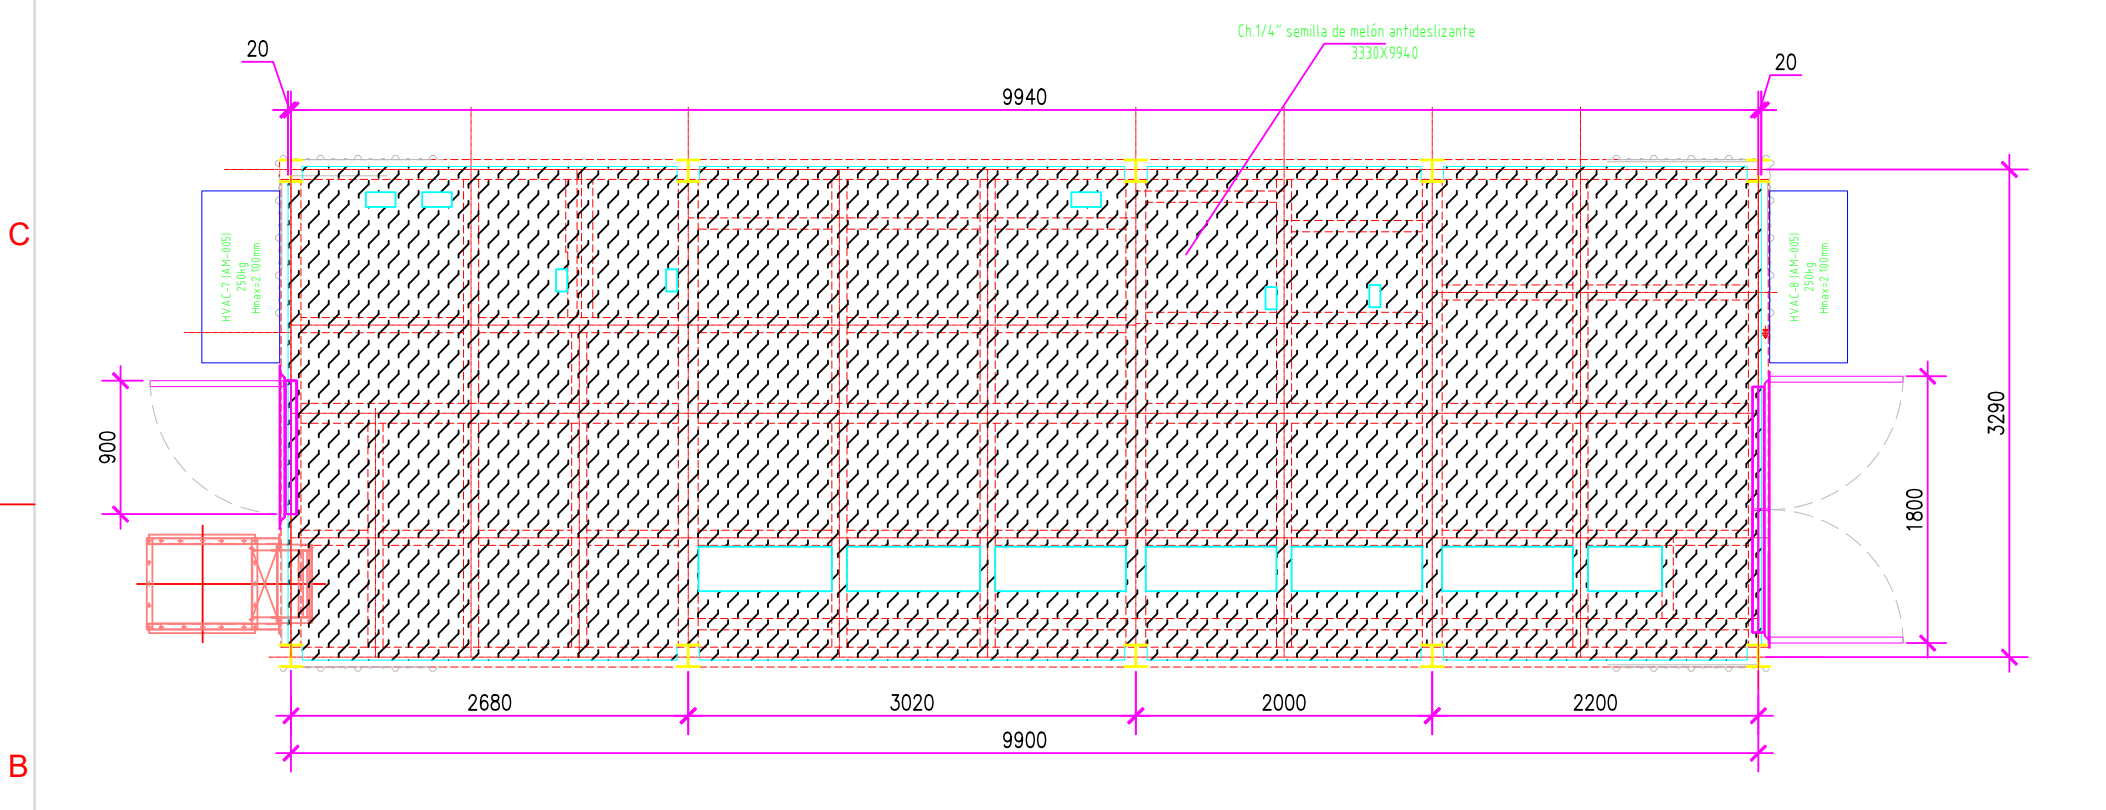


PLANTA CHAPA DE PISO PLATAFORMA PLT SEM-02
ESCALA 1:50

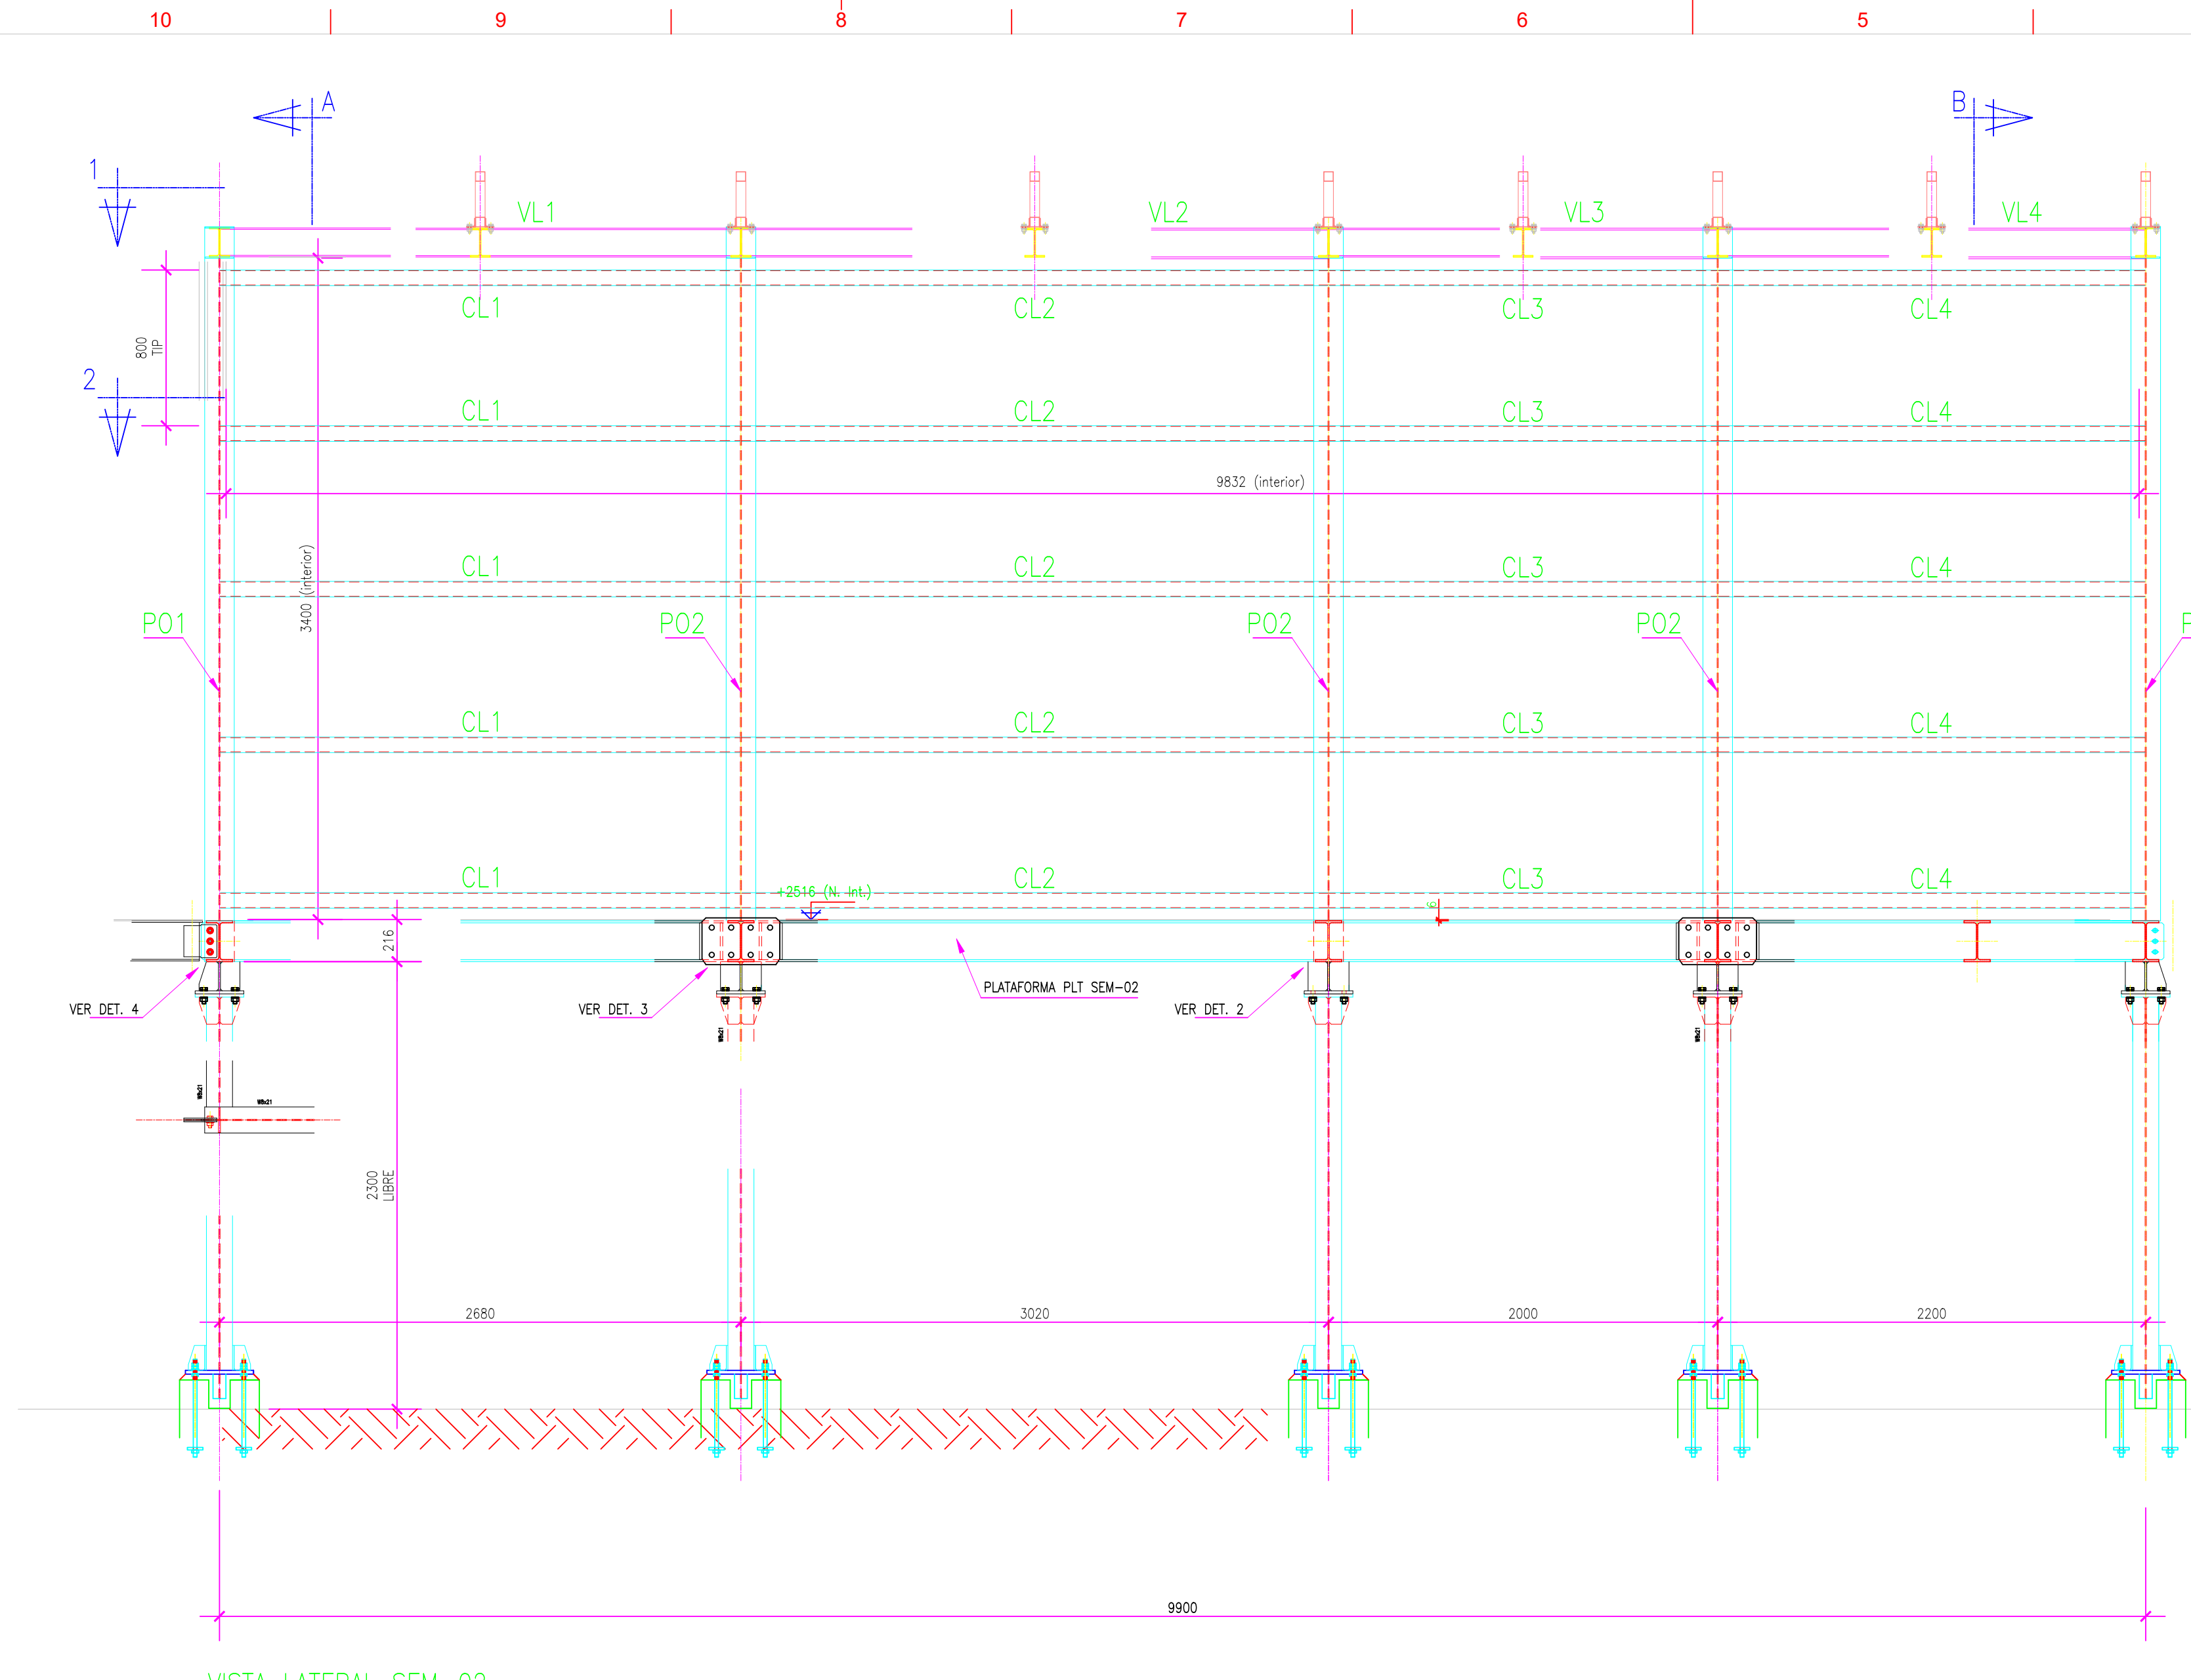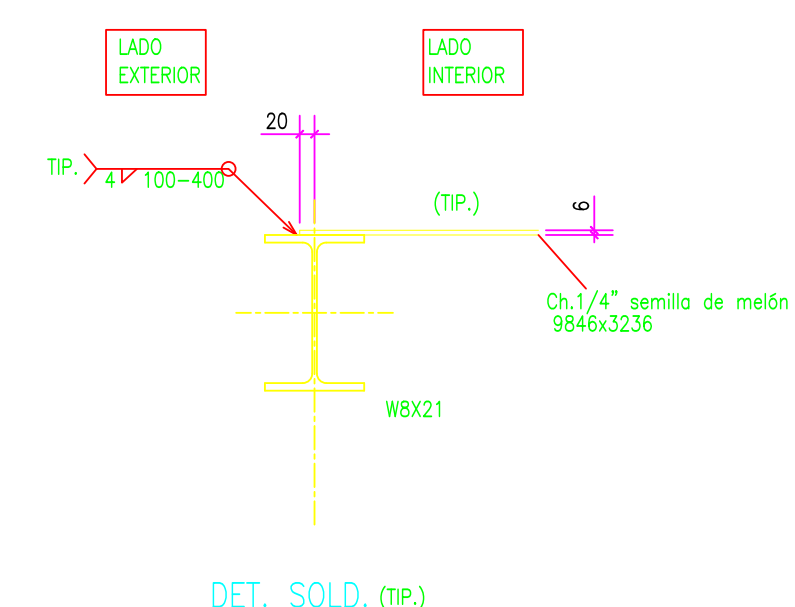

VISTA LATERAL SEM-02
ESCALA 1:25

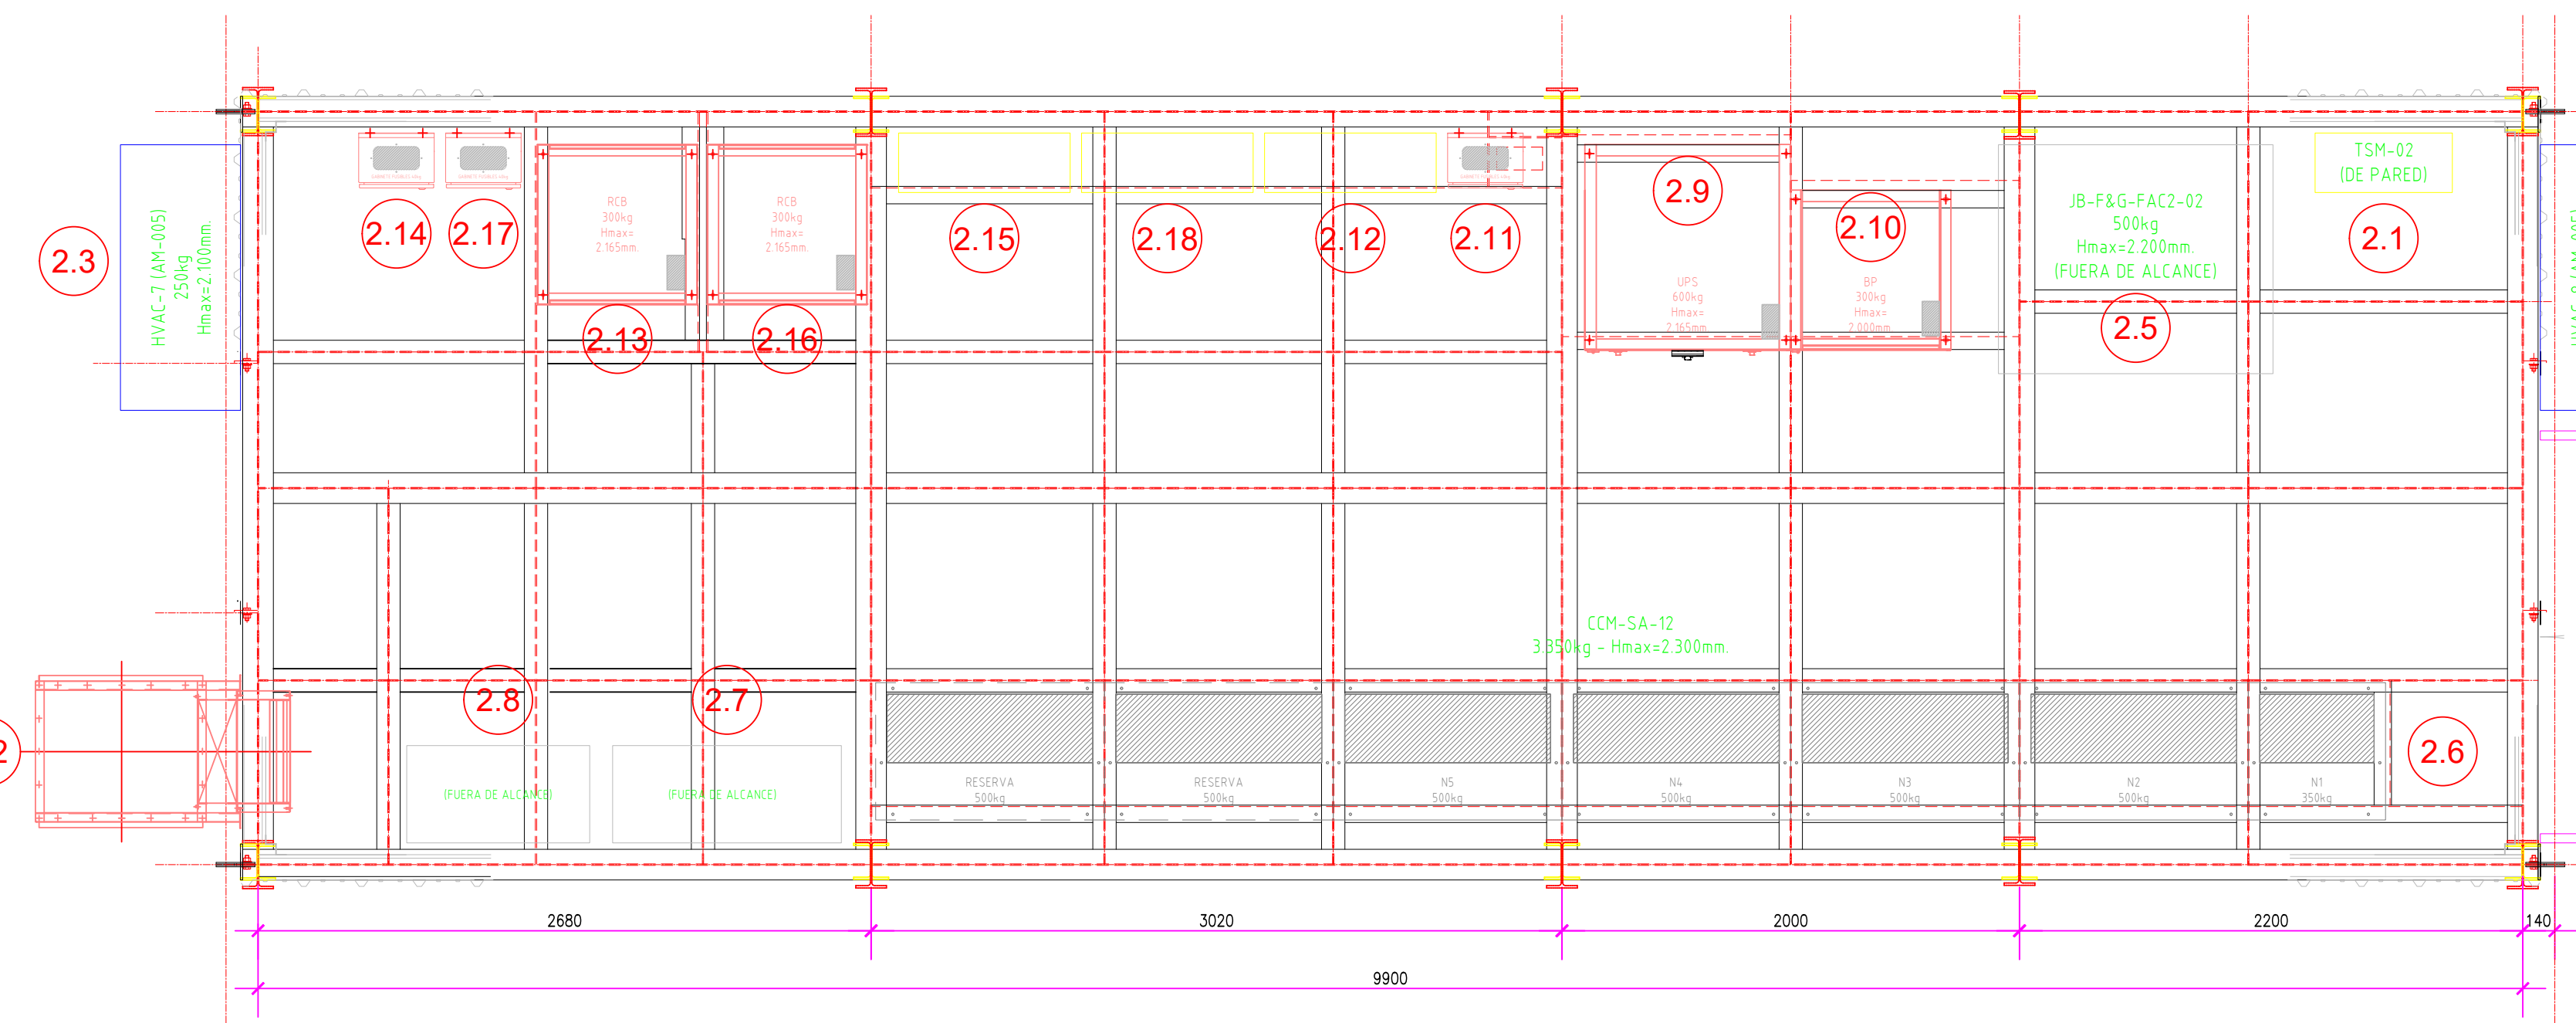

PLANTA PLATAFORMA PLT SEM-02
ESCALA 1:25

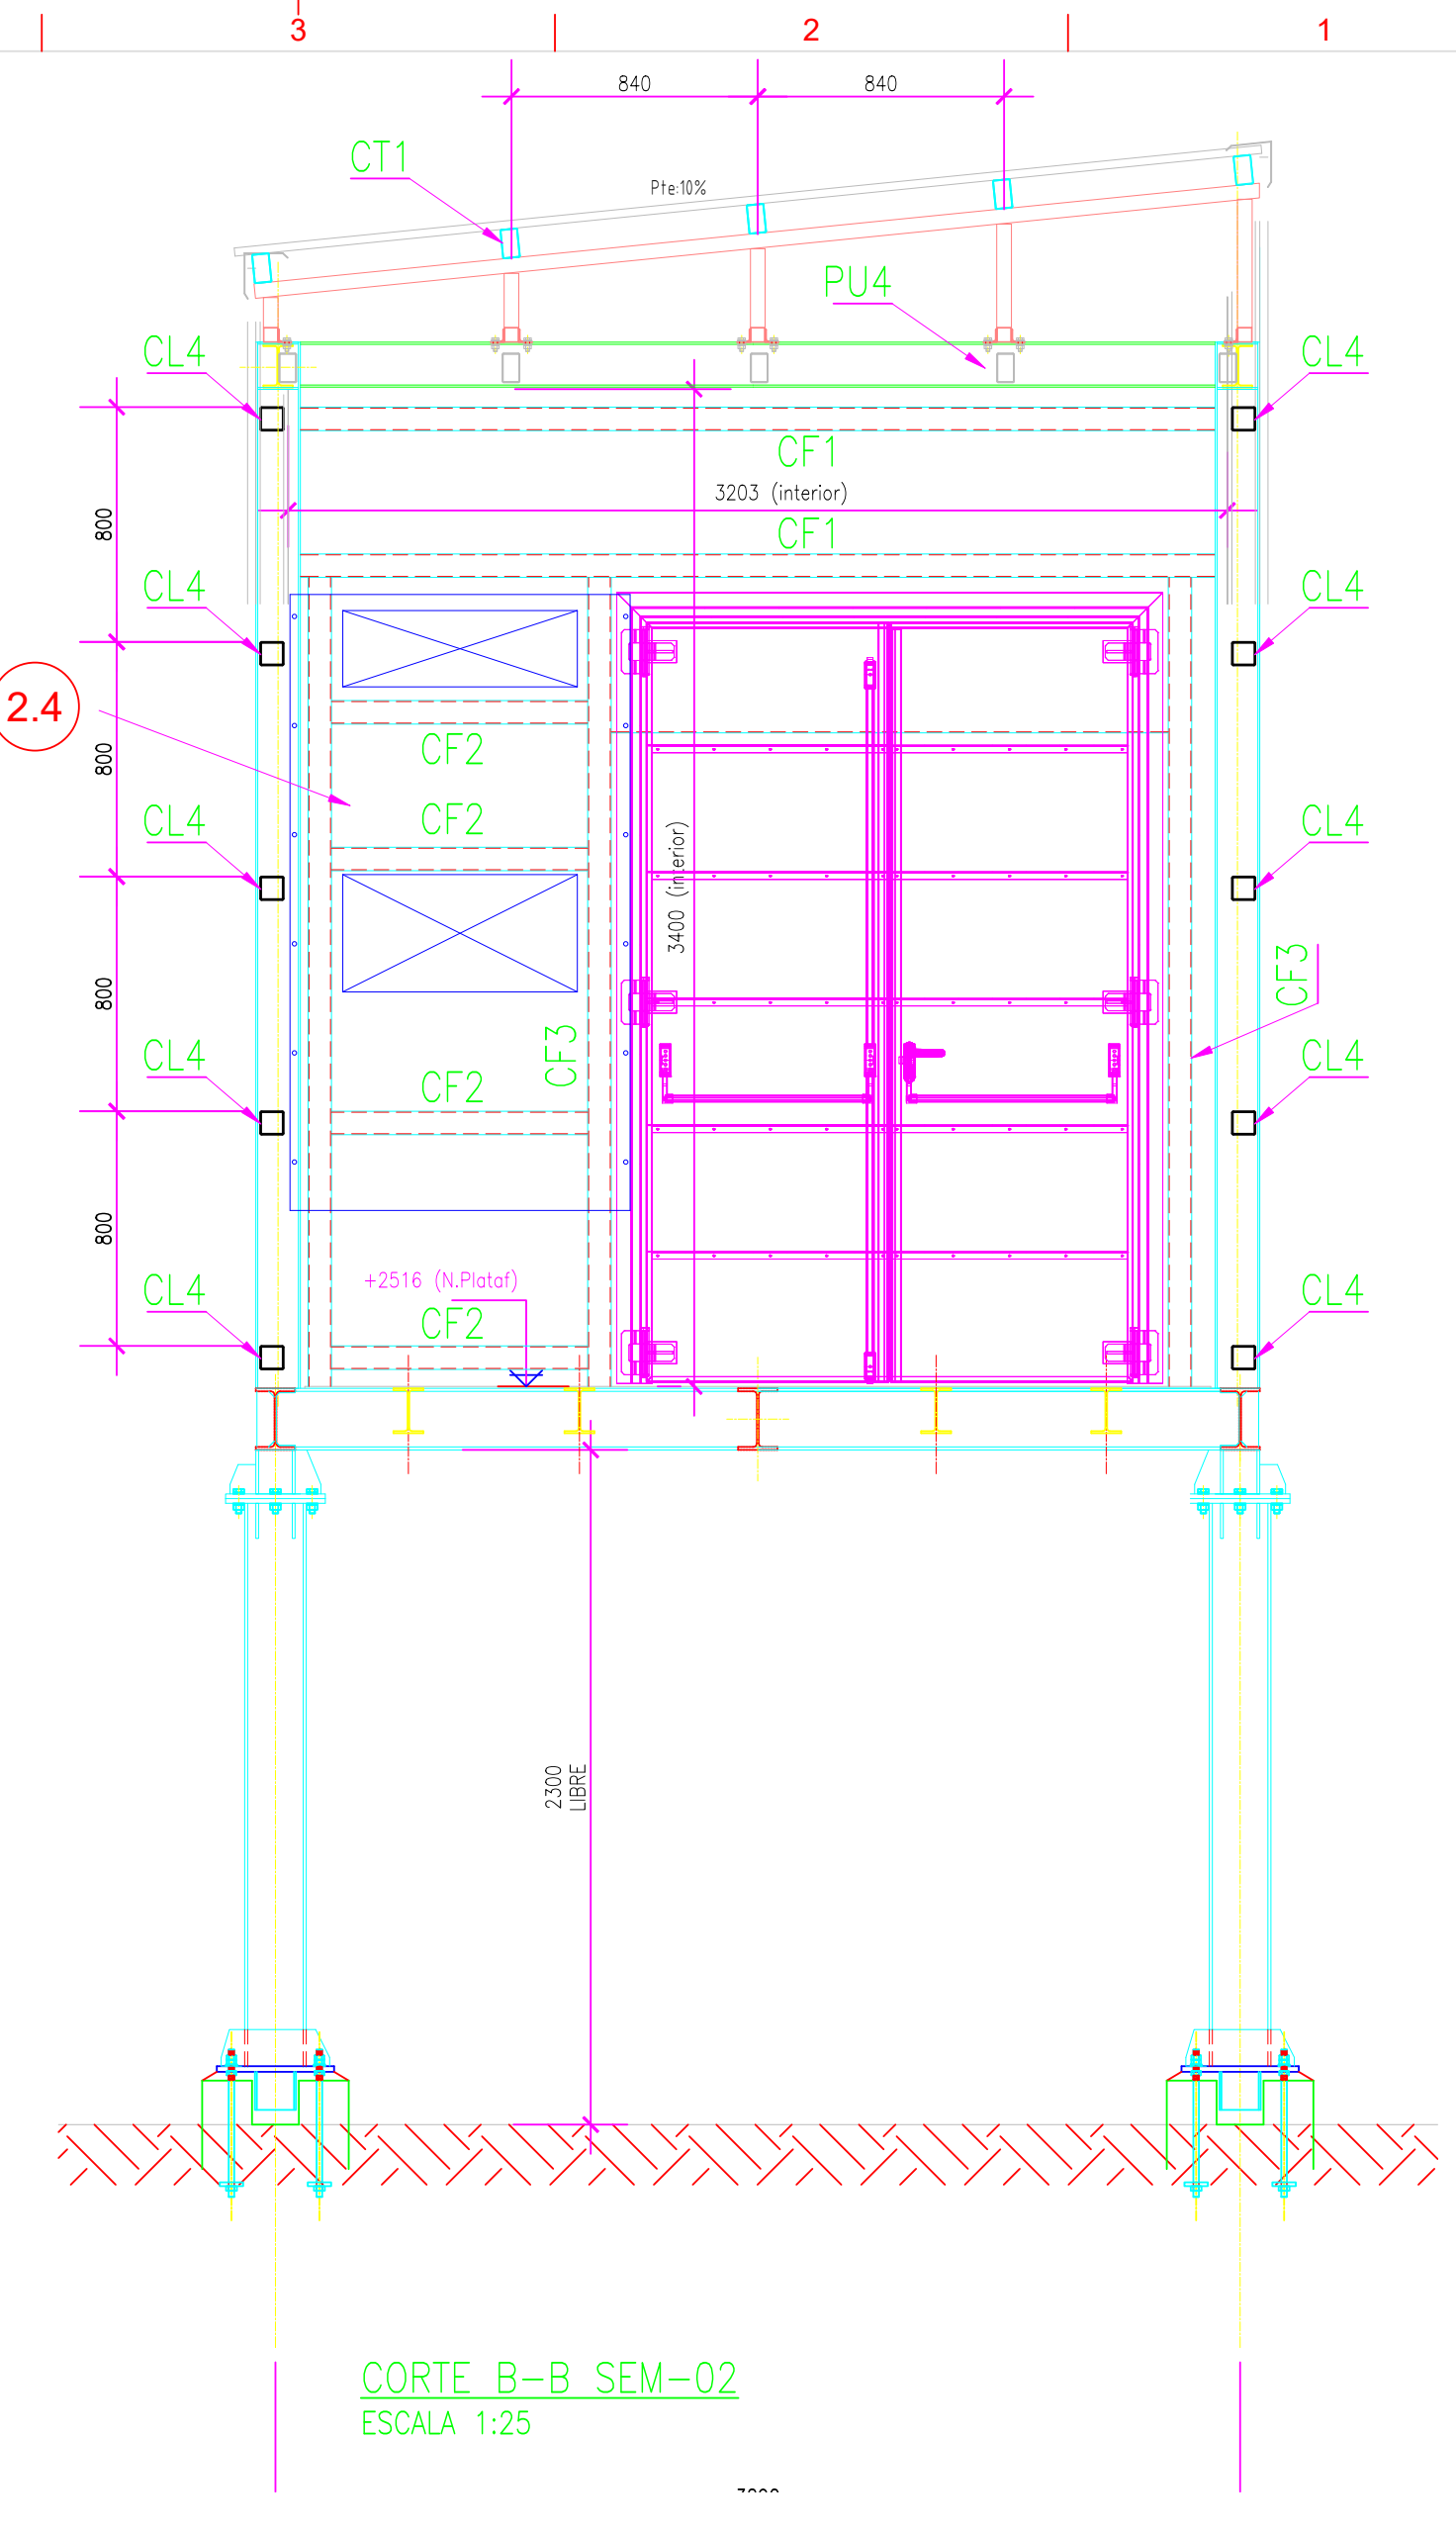

CORTE B-B SEM-02
ESCALA 1:25


NOTAS:

- MEDIDAS EN mm
- CALIDAD PERFILES LAMINADOS W: ACERO F-36 o ASTM A-572 Gr50
- CALIDAD PERFILES LAMINADOS, CHAPAS y PLANCHUELAS: ACERO F-24
- CALIDAD BULONES ASTM A-325
- TODAS LAS SOLDADURAS SE REALIZARAN S/NORMA A.W.S. D1.1-96 Y SEGUN LA ESPECIFICACION DE PROCEDIMIENTO.
- LAS COLUMNAS DE SOPORTE Y LAS FUNDACIONES INDICADAS SON MERAMENTE ILUSTRATIVAS, ESTAN FUERA DEL ALCANCE DEL PROYECTO.


DOCUMENTOS DE REFERENCIA

- TE-631-104728-LY-C-1701 - LAYOUT GENERAL DE IMPLANTACIÓN SALAS (TAG: SEM-01 / SEM-02 / SEM-03)
- TE-631-104728-MC-C-1701 - MEMORIA DE CÁLCULOS SALAS SEM-01/02/03


0	15/12/2025	EMISIÓN PARA APROBACIÓN		AMB	RMP	JJA	
REV.	FECHA	DESCRIPCIÓN		ELABORO	REVISO	APROBO	
tgs				DIRECCIÓN DE OPERACIONES GERENCIA			
LUGAR: NEUQUÉN - PLANTA TRATAYÉN				TÍTULO: SALAS ELÉCTRICAS PLANTA ESTABILIZADORA CONDENSADOS SLUG CATCHER - INGL ETAPA TEMPORARIA			
OBRA: SALAS ELÉCTRICAS PLANTA ESTABILIZADORA CONDENSADOS SLUG CATCHER - INGL ETAPA TEMPORARIA				MÓDULO N°2 (TAG: SEM-02)			
ESPACIO CONTRATISTA				INFYA			
N° Doc. Ingeniería:				FECHA: 15/12/25	OBRA N°: 104.728	ESCALA: INDICADAS	HOJA: 1 de 5
Rev:				DOCUMENTO: TE-631-104728-PL-C-1702			
				REVISIÓN			
				0			

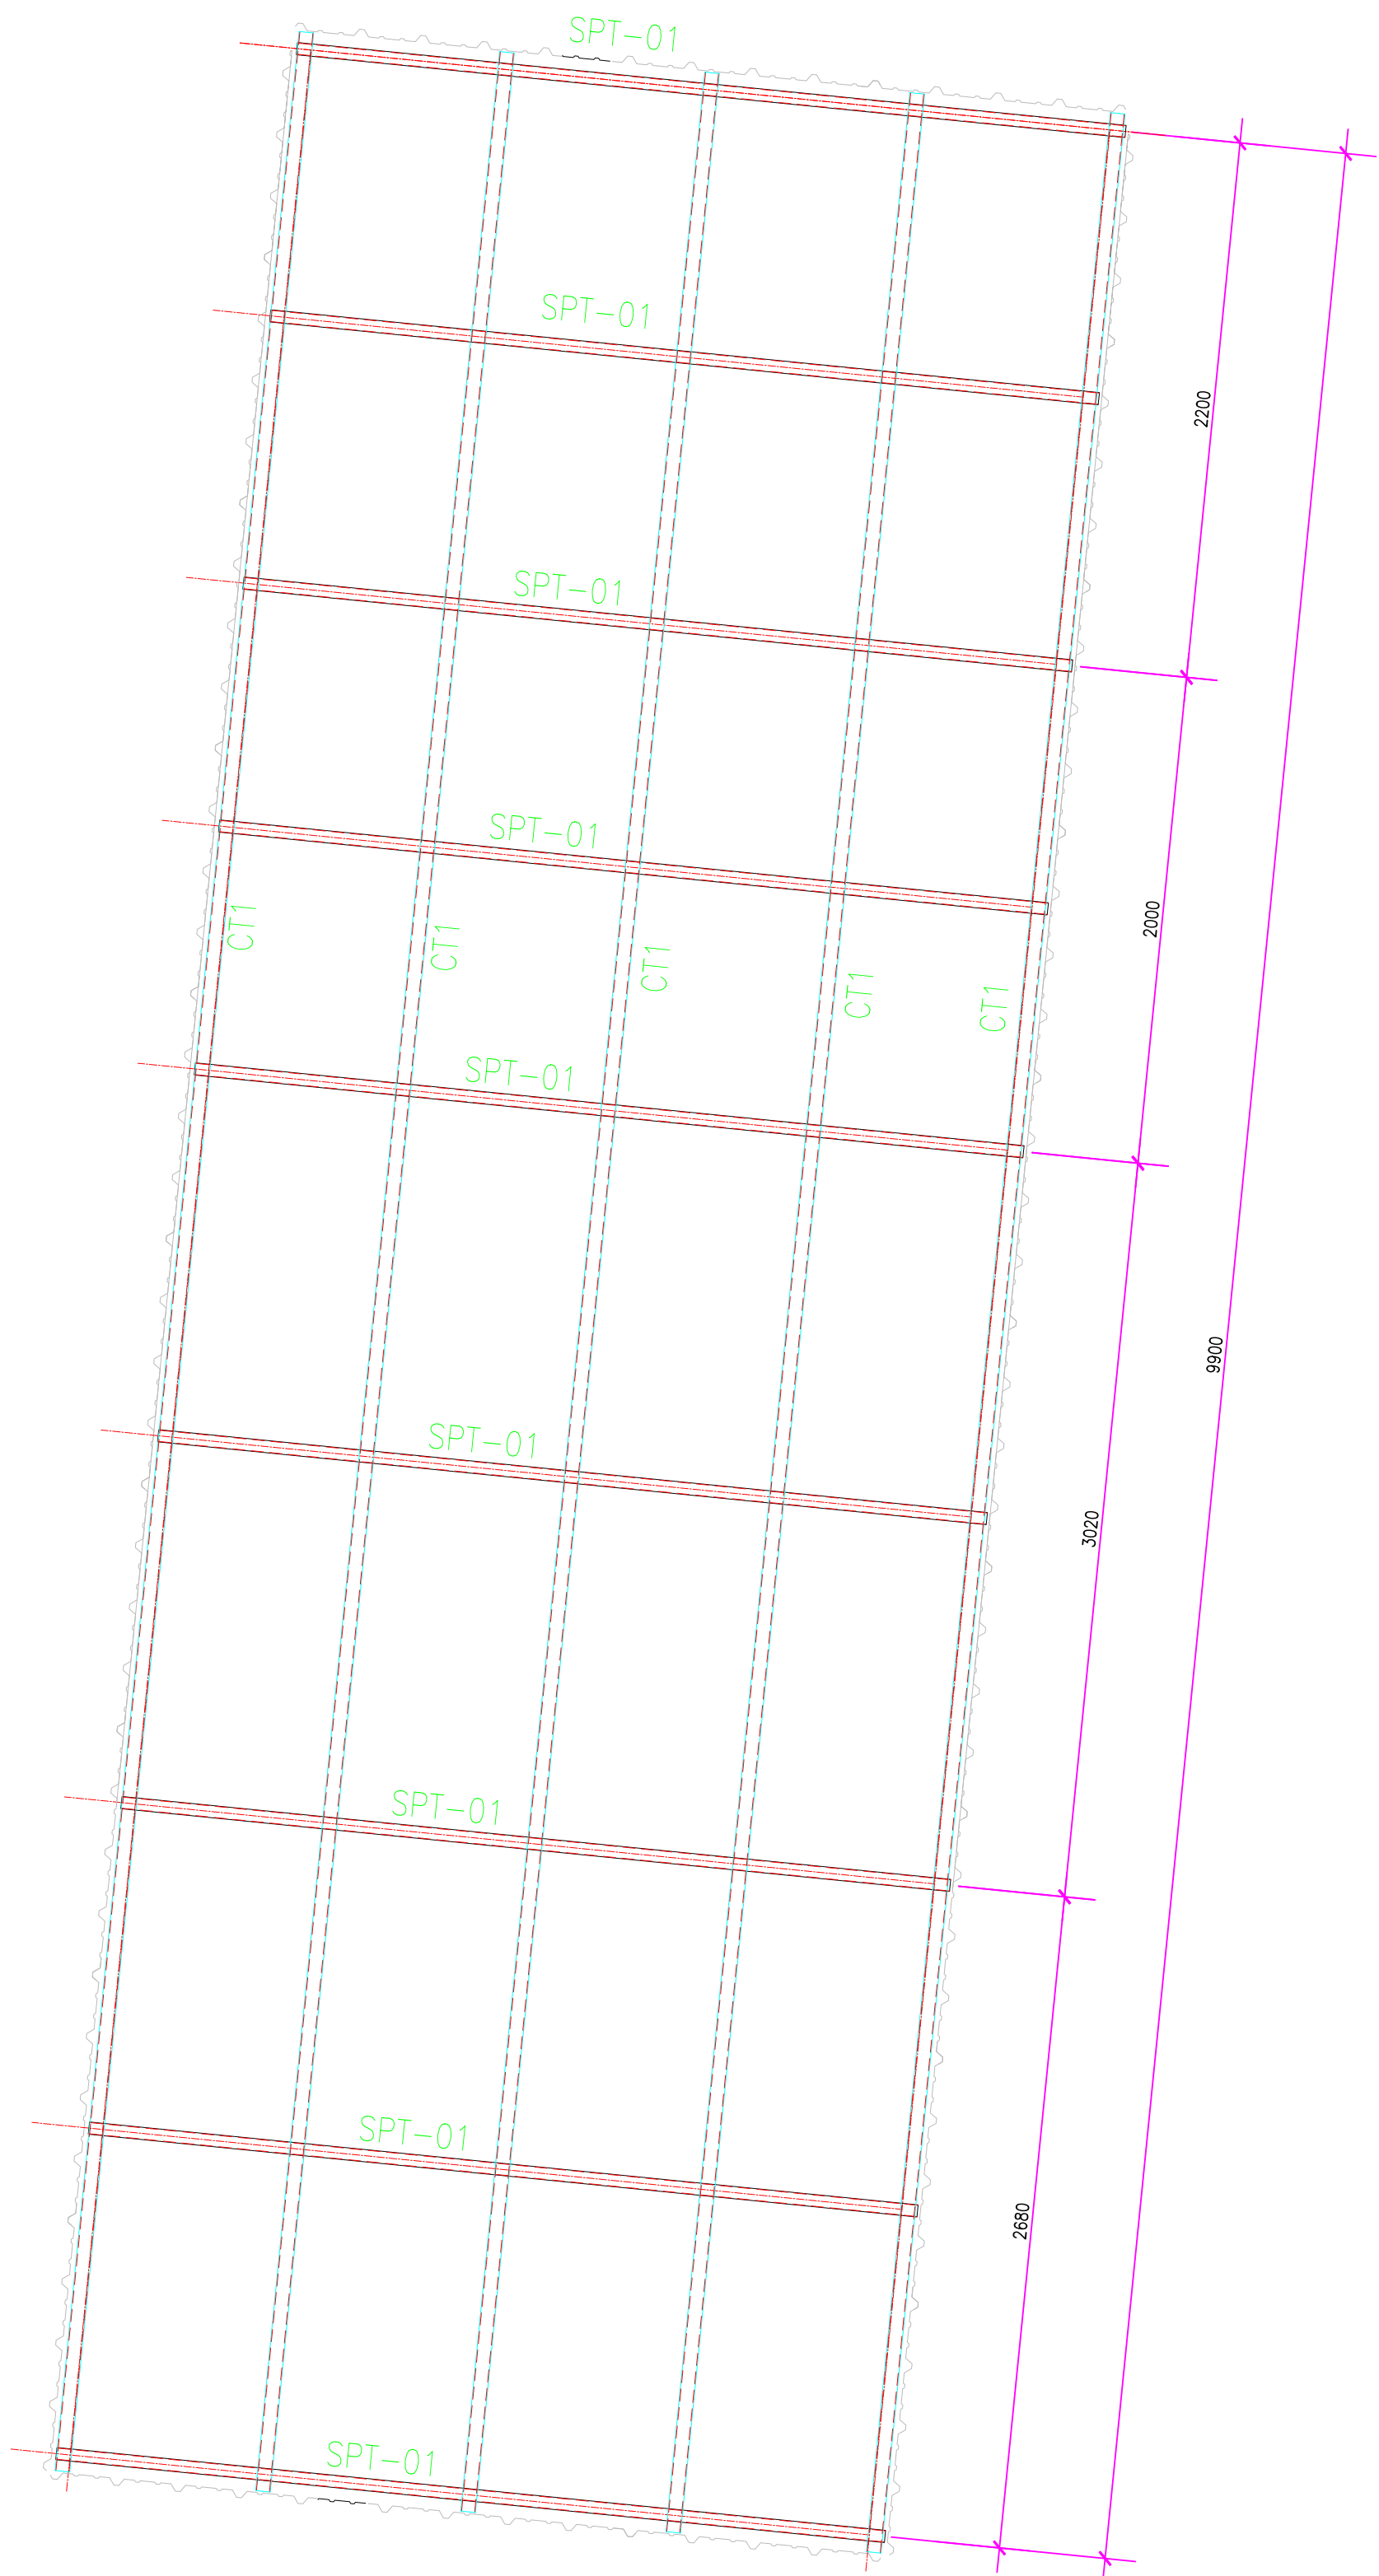


PLANTA TECHOS SEM-02
ESCALA 1:25

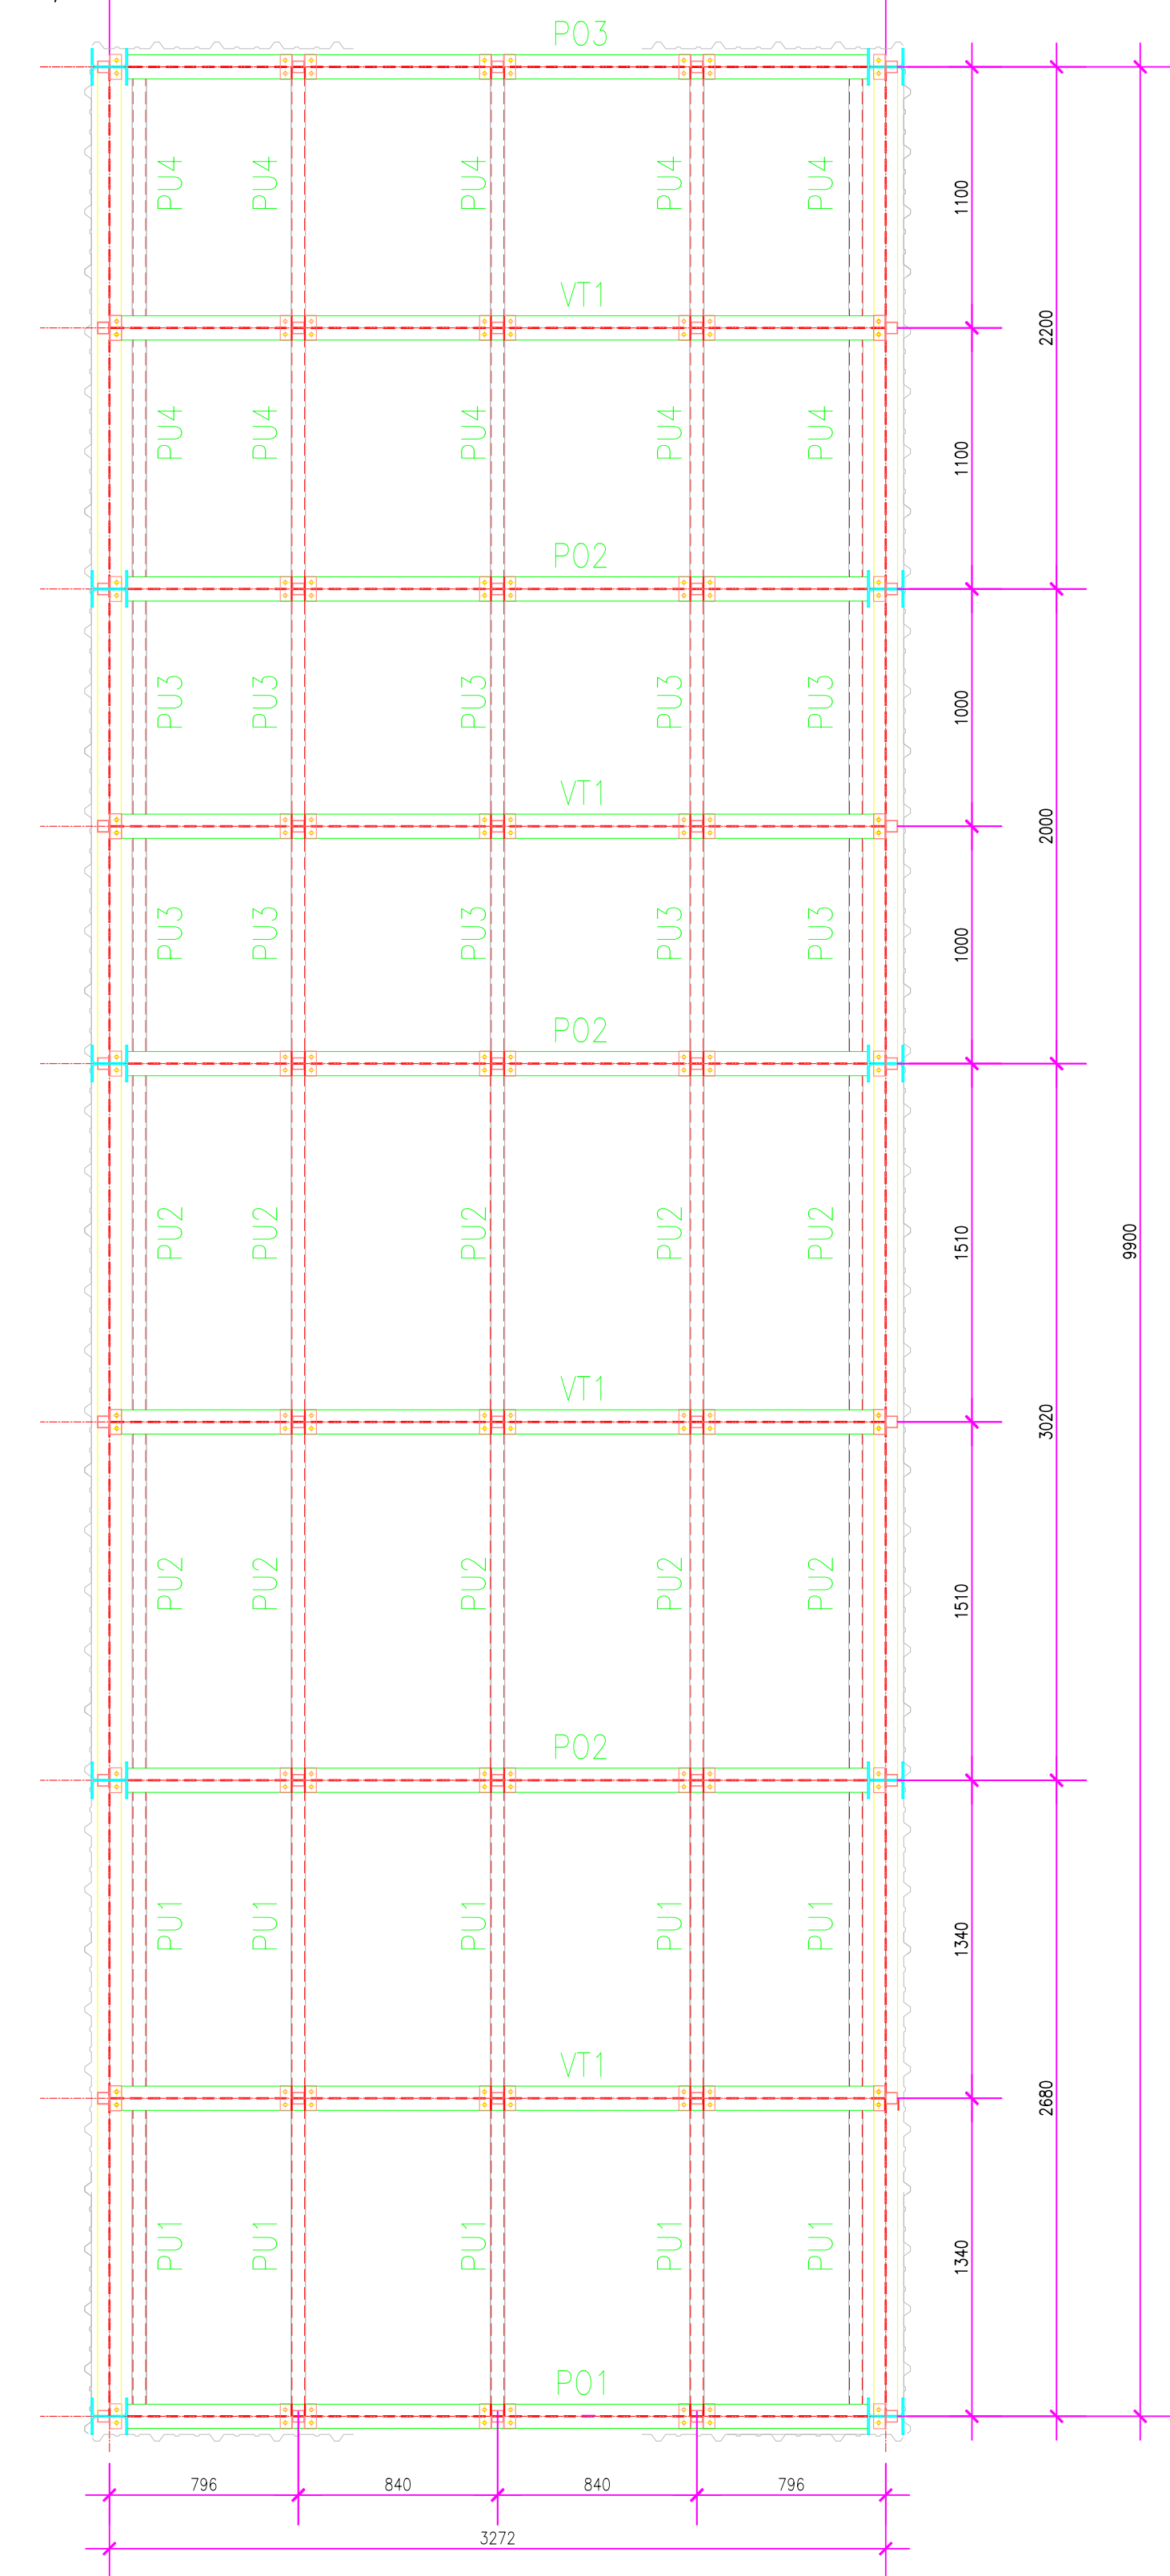


PLANTA PUNTALES
ESCALA 1:25

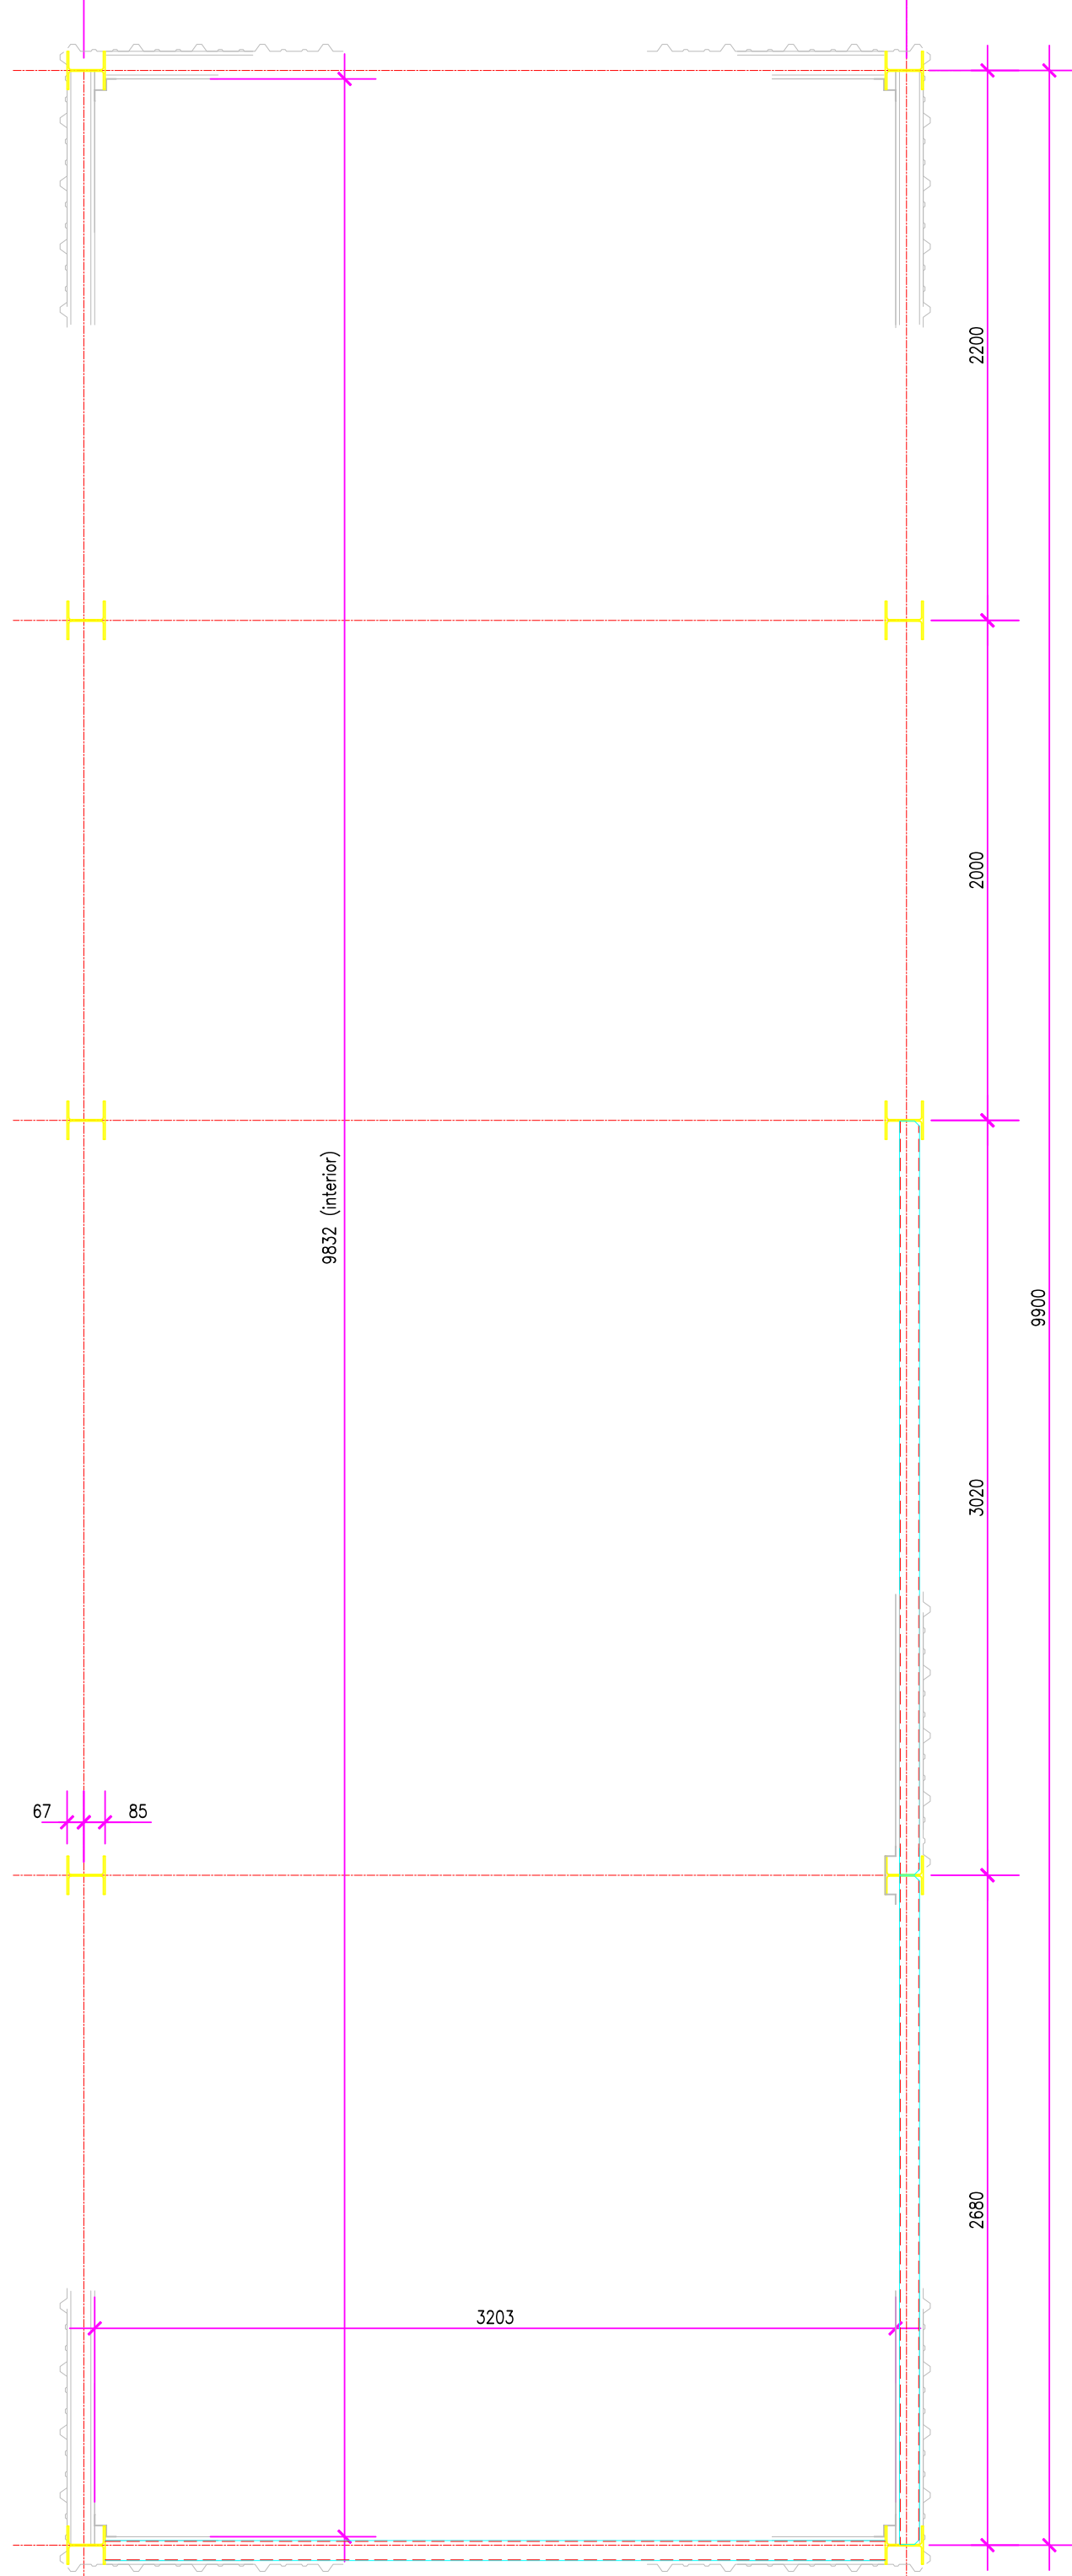


CORTE 2-2
ESCALA 1:25

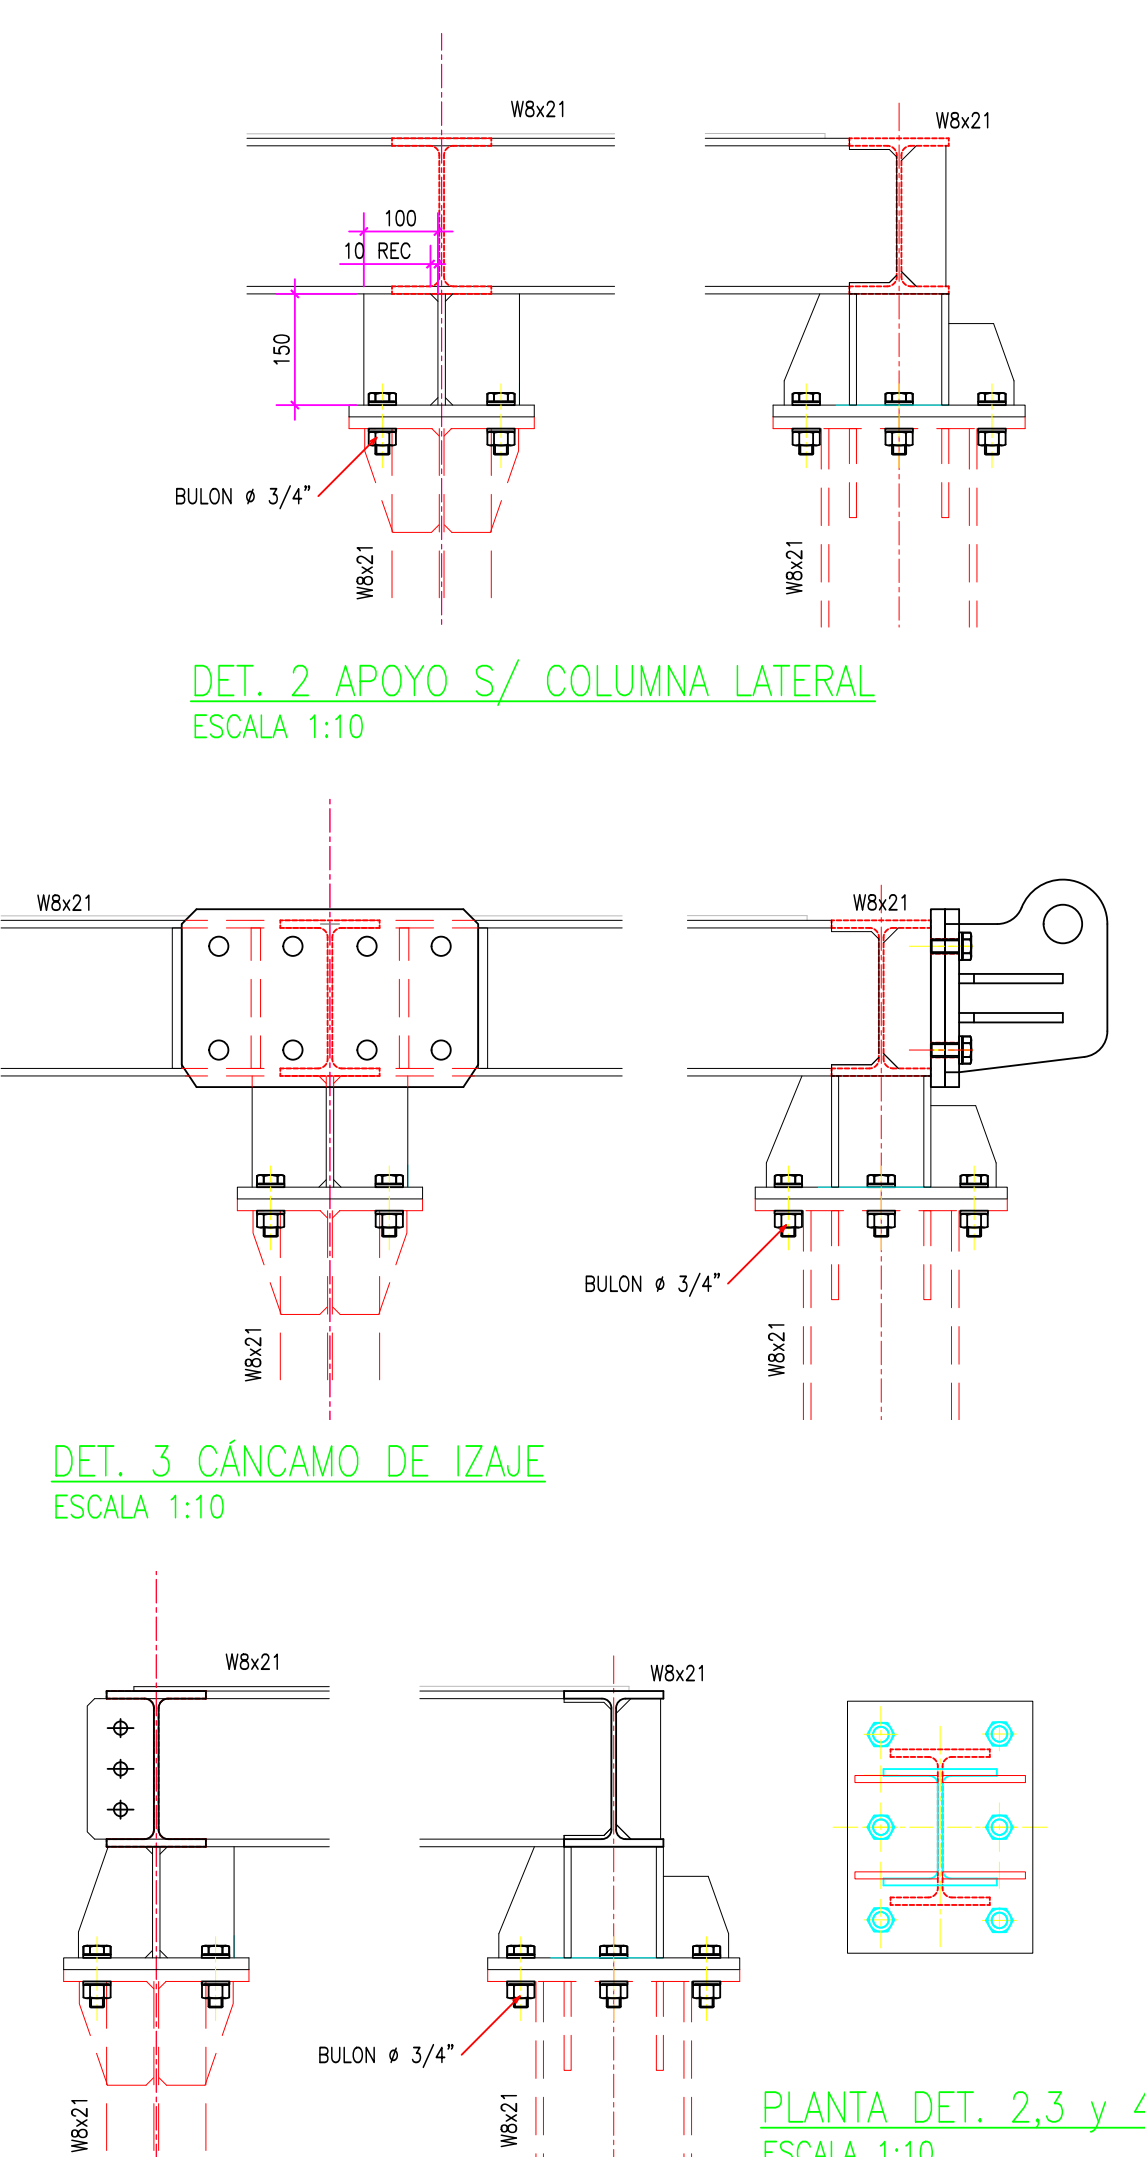

PLANTA DET. 2,3 y 4
ESCALA 1:10

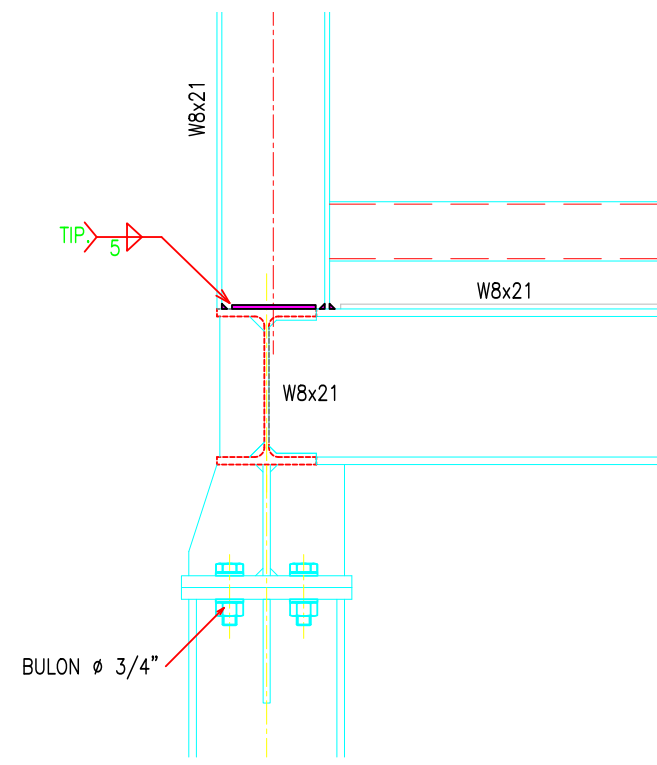

DET. 5 SOLD. NUDO INFERIOR
ESCALA 1:10

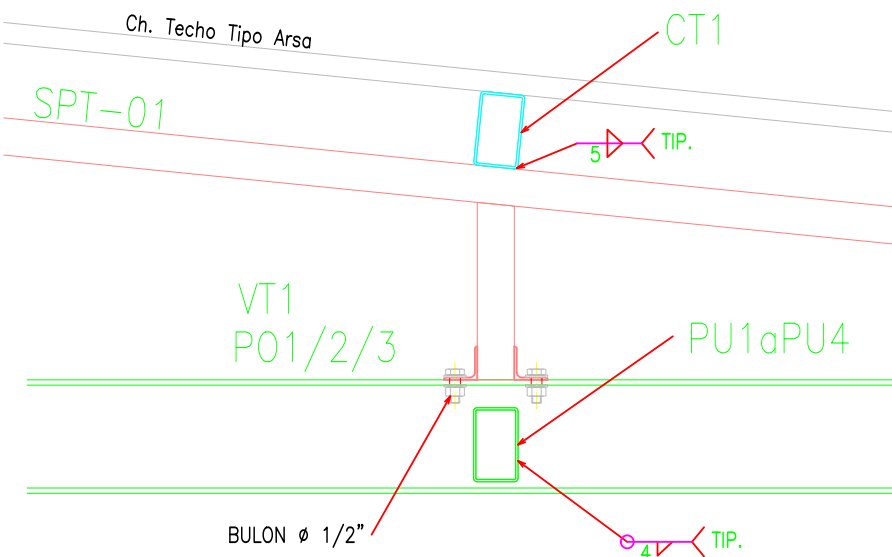

DET. 6
ESCALA 1:10

- NOTAS:
- MEDIDAS EN mm.
 - CALIDAD PERFILES LAMINADOS W: ACERO F-36 o ASTM A-572 Gr50
 - CALIDAD PERFILES LAMINADOS, CHAPAS y PLANCHUELAS: ACERO F-24
 - CALIDAD BULONES ASTM A-325
 - TODAS LAS SOLDADURAS SE REALIZARAN S/NORMA A.W.S. D1.1-96 Y SEGUN LA ESPECIFICACION DE PROCEDIMIENTO.

DOCUMENTOS DE REFERENCIA

- TE-631-104728-LY-C-1701 - LAYOUT GENERAL DE IMPLANTACIÓN SALAS (TAG: SEM-01 / SEM-02 / SEM-03)
- TE-631-104728-MC-C-1701 - MEMORIA DE CÁLCULOS SALAS SEM-01/02/03

0	15/12/2025	EMISIÓN PARA APROBACIÓN	AMB	RMP	JJA
REV.	FECHA	DESCRIPCIÓN	ELABORÓ	REVISÓ	APROBO
tgs			DIRECCIÓN DE OPERACIONES GERENCIA		
LUGAR: NEUQUÉN - PLANTA TRATAYÉN			TÍTULO: PLANO DE ESTRUCTURAS METÁLICAS MÓDULO N°2 (TAG: SEM-02)		
OBRA: SALAS ELÉCTRICAS PLANTA ESTABILIZADORA CONDENSADOS SLUG CATCHER - NGL ETAPA TEMPORARIA					
ESPACIO CONTRASTO			FECHA: 15/12/25	OBRA N°: 104.728	ESCALA: INDICADAS
INFYA			DOCUMENTO: TE-631-104728-PL-C-1702	HOJA: 2 de 5	REVISIÓN: 0
N° Doc. Ingeniería:			Rev:		

