


15
H
G
F
E
D
C
B
A
15


14
13
12
11
10
9
8
7
6
5
4
3
2
1

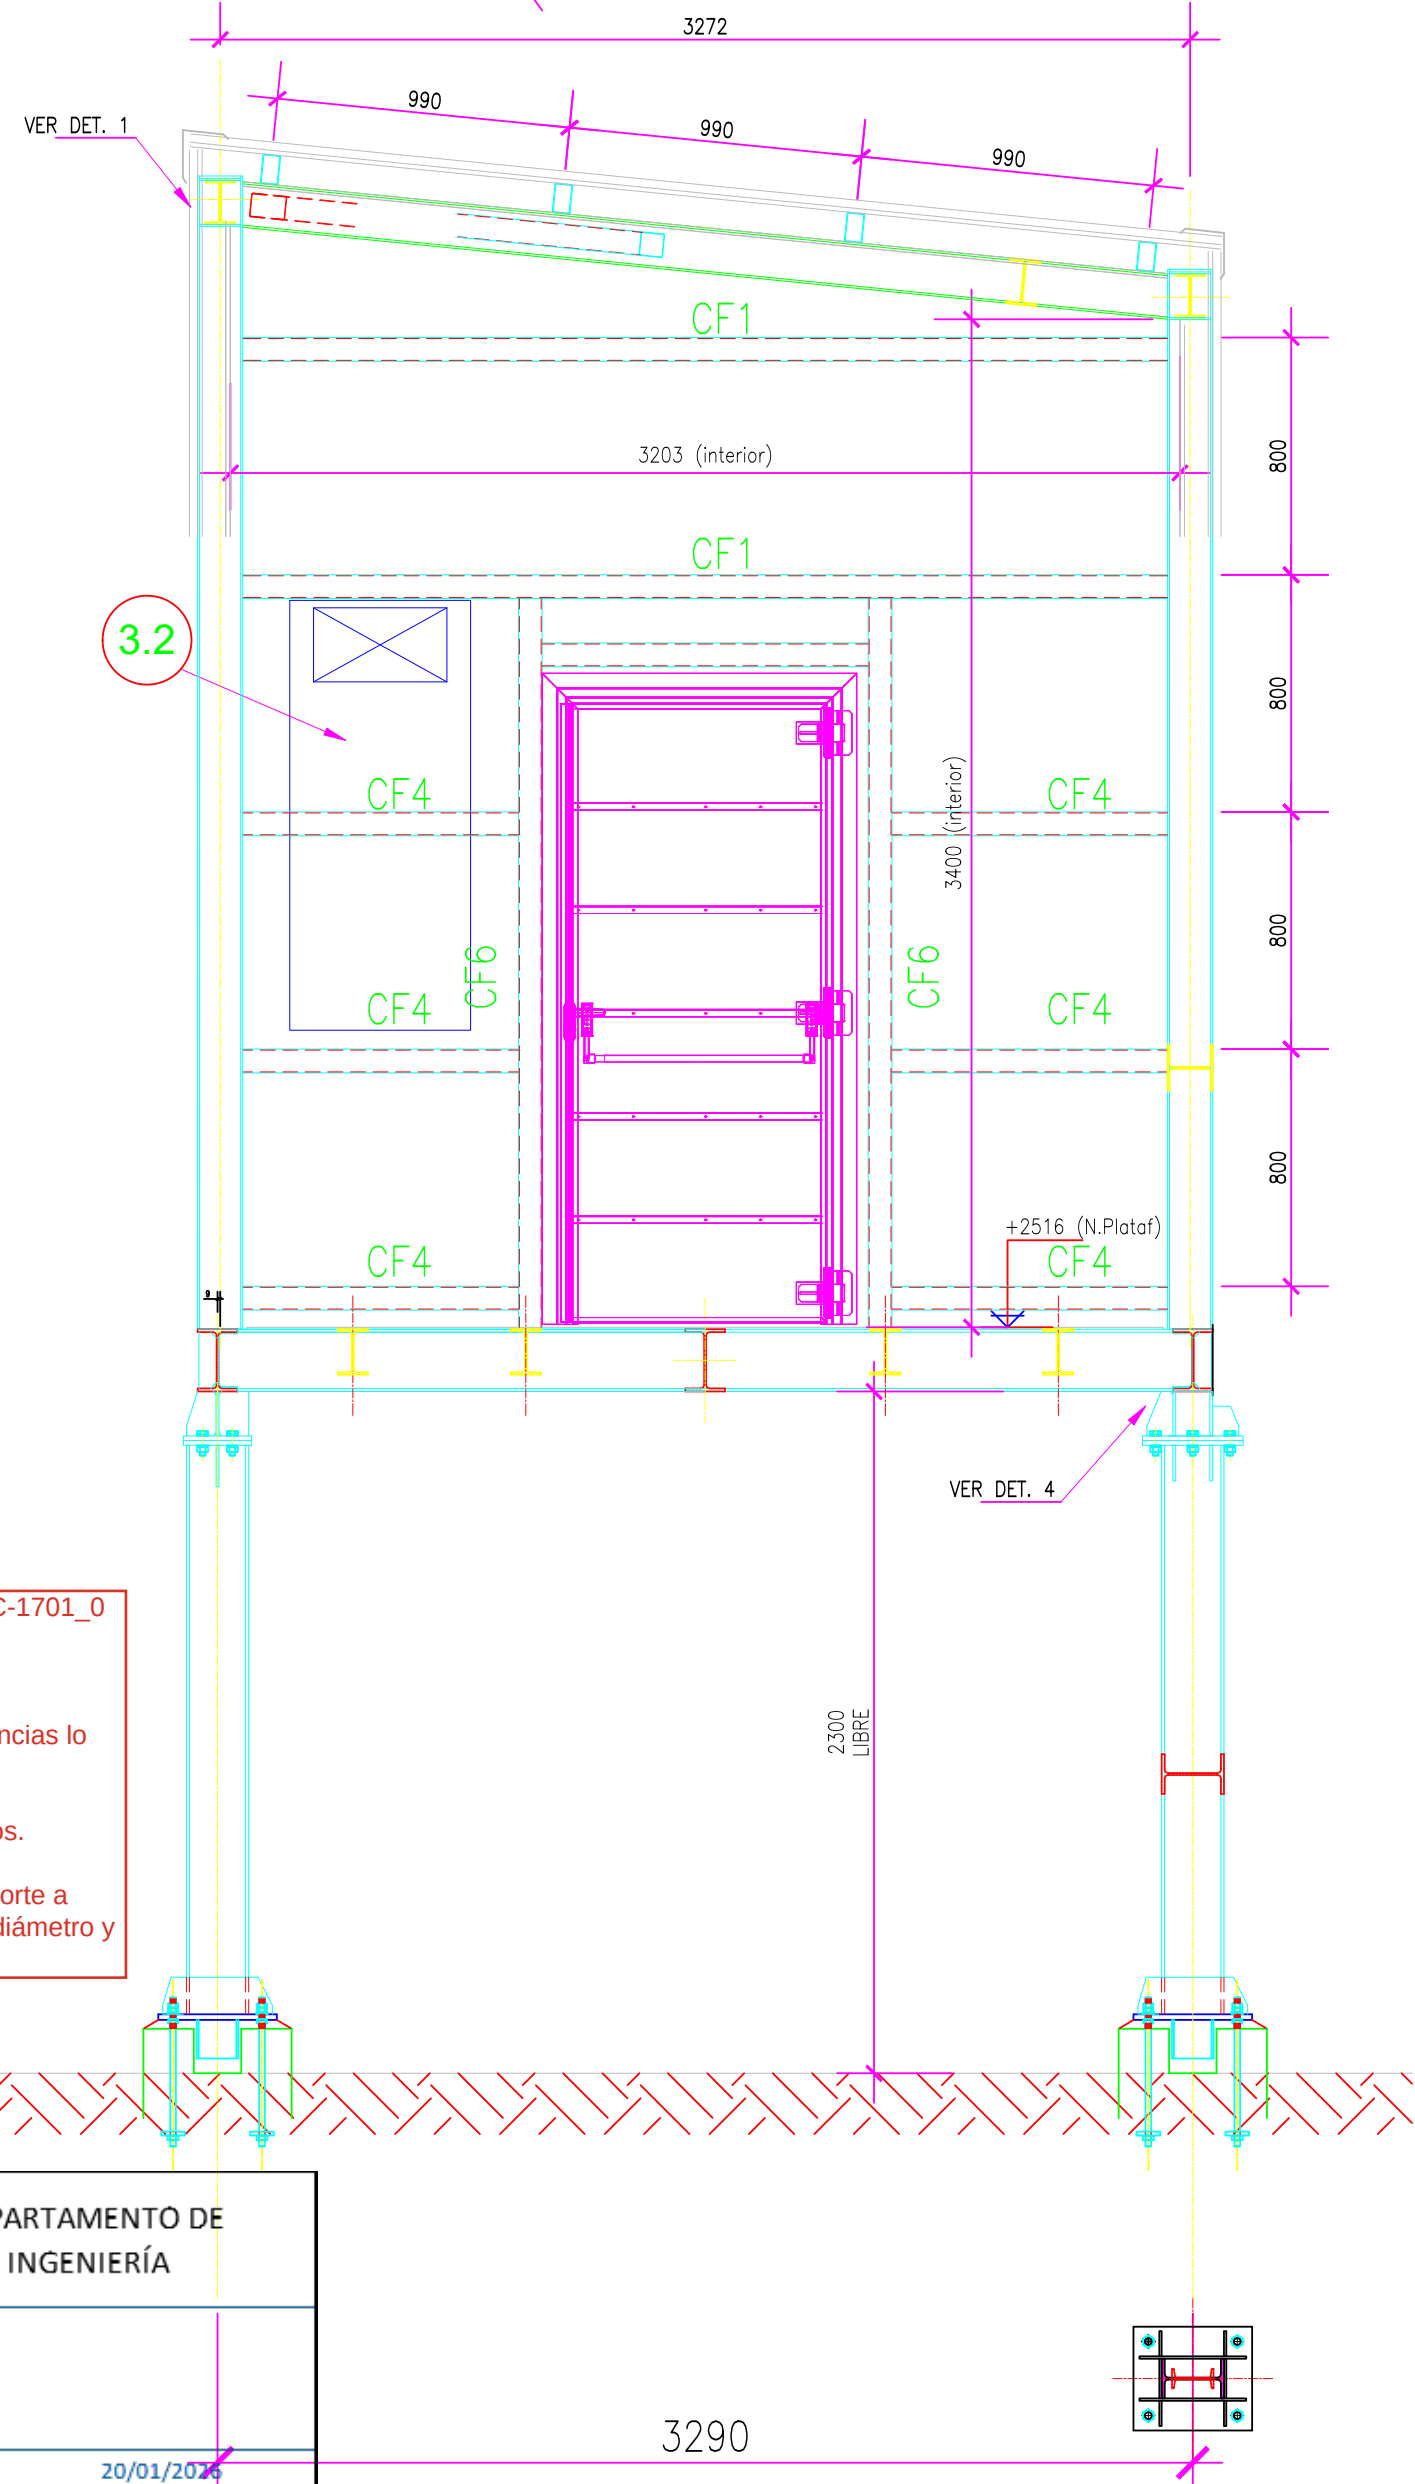


- Ver comentarios en el plano: TE-631-104728-PL-C-1701_0
- Ajustar las puntas de impresión
- Indicar claramente los límites de provisión y diferencias lo que será "por terceros".
- No computar elementos que son provistos por otros.
- Indicar dimensiones de placa de vinculación a soporte a suministrar por terceros. Indicar también agujeros, diámetro y separación.

HYtech		DEPARTAMENTO DE INGENIERÍA	
☒	VISTO CON COMENTARIOS (CC)		
☐	VISTO (V)		
JUD	HYTECH INGENIERÍA S.A.	FECHA	20/01/2025
FIRMA/INICIALES	ACLARACIÓN		


CORTE A-A SEM-03
ESCALA 1:25

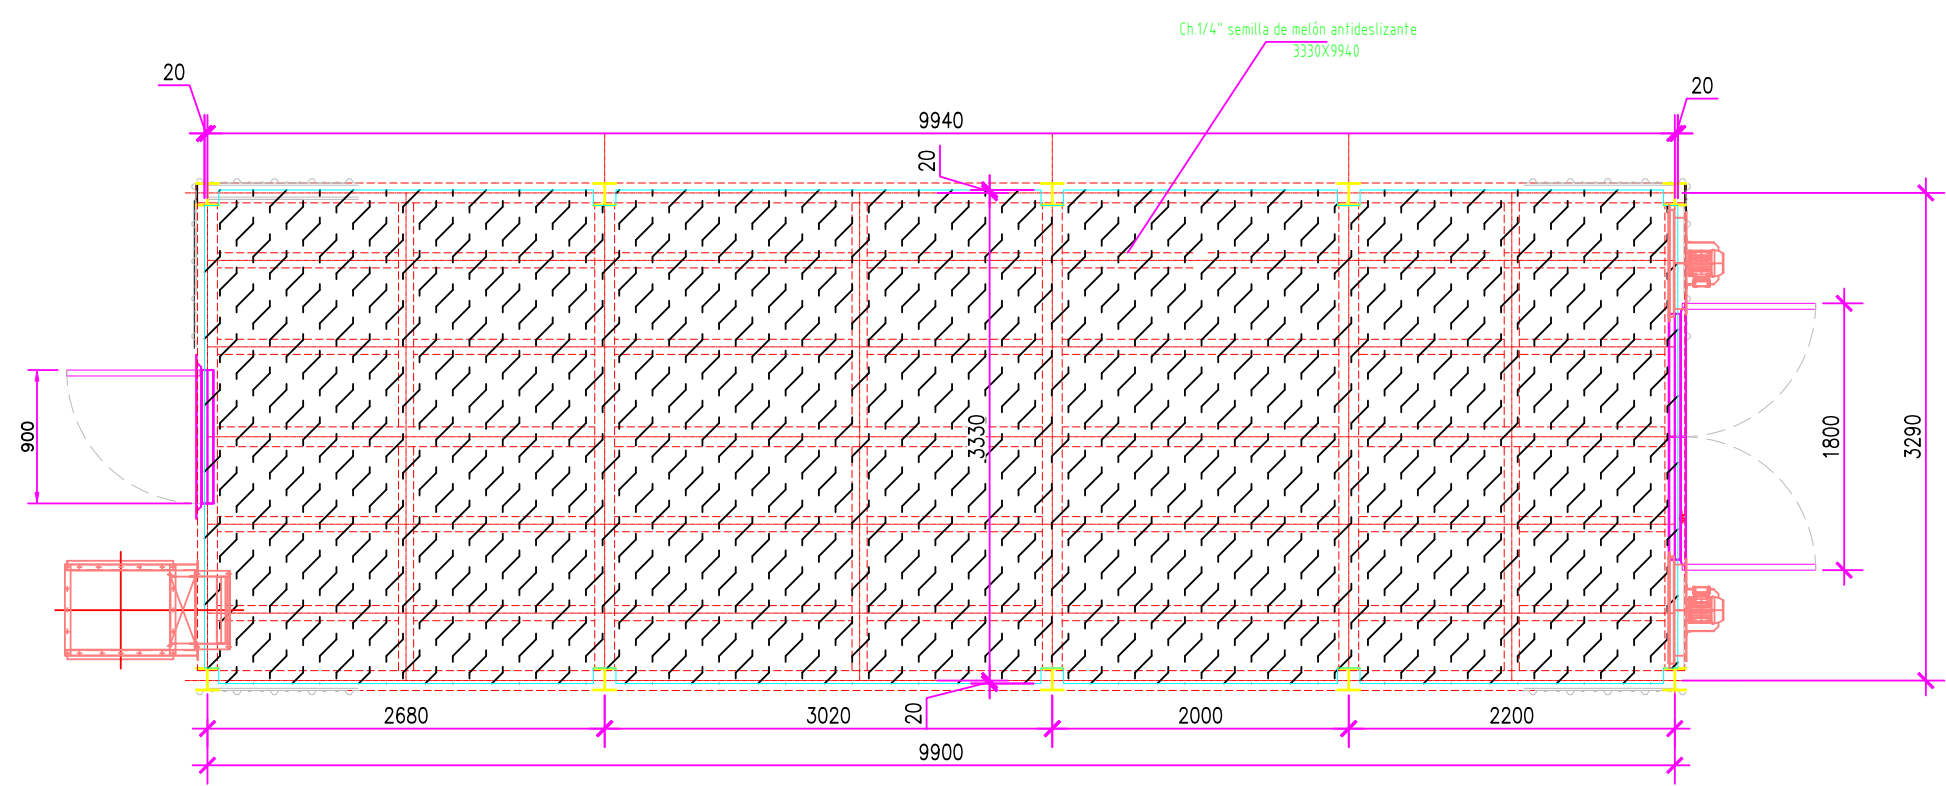


PLANTA CHAPA DE PISO PLATAFORMA PLT SEM-03
ESCALA 1:50

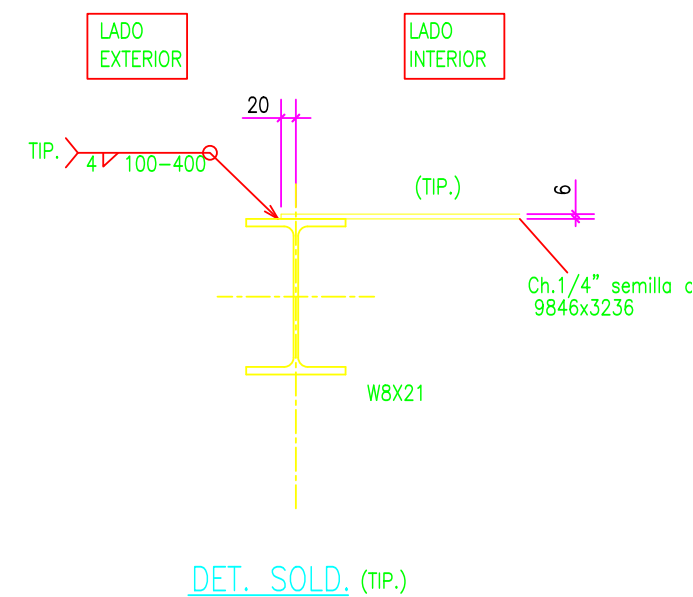


DET. SOLD. (TP.)

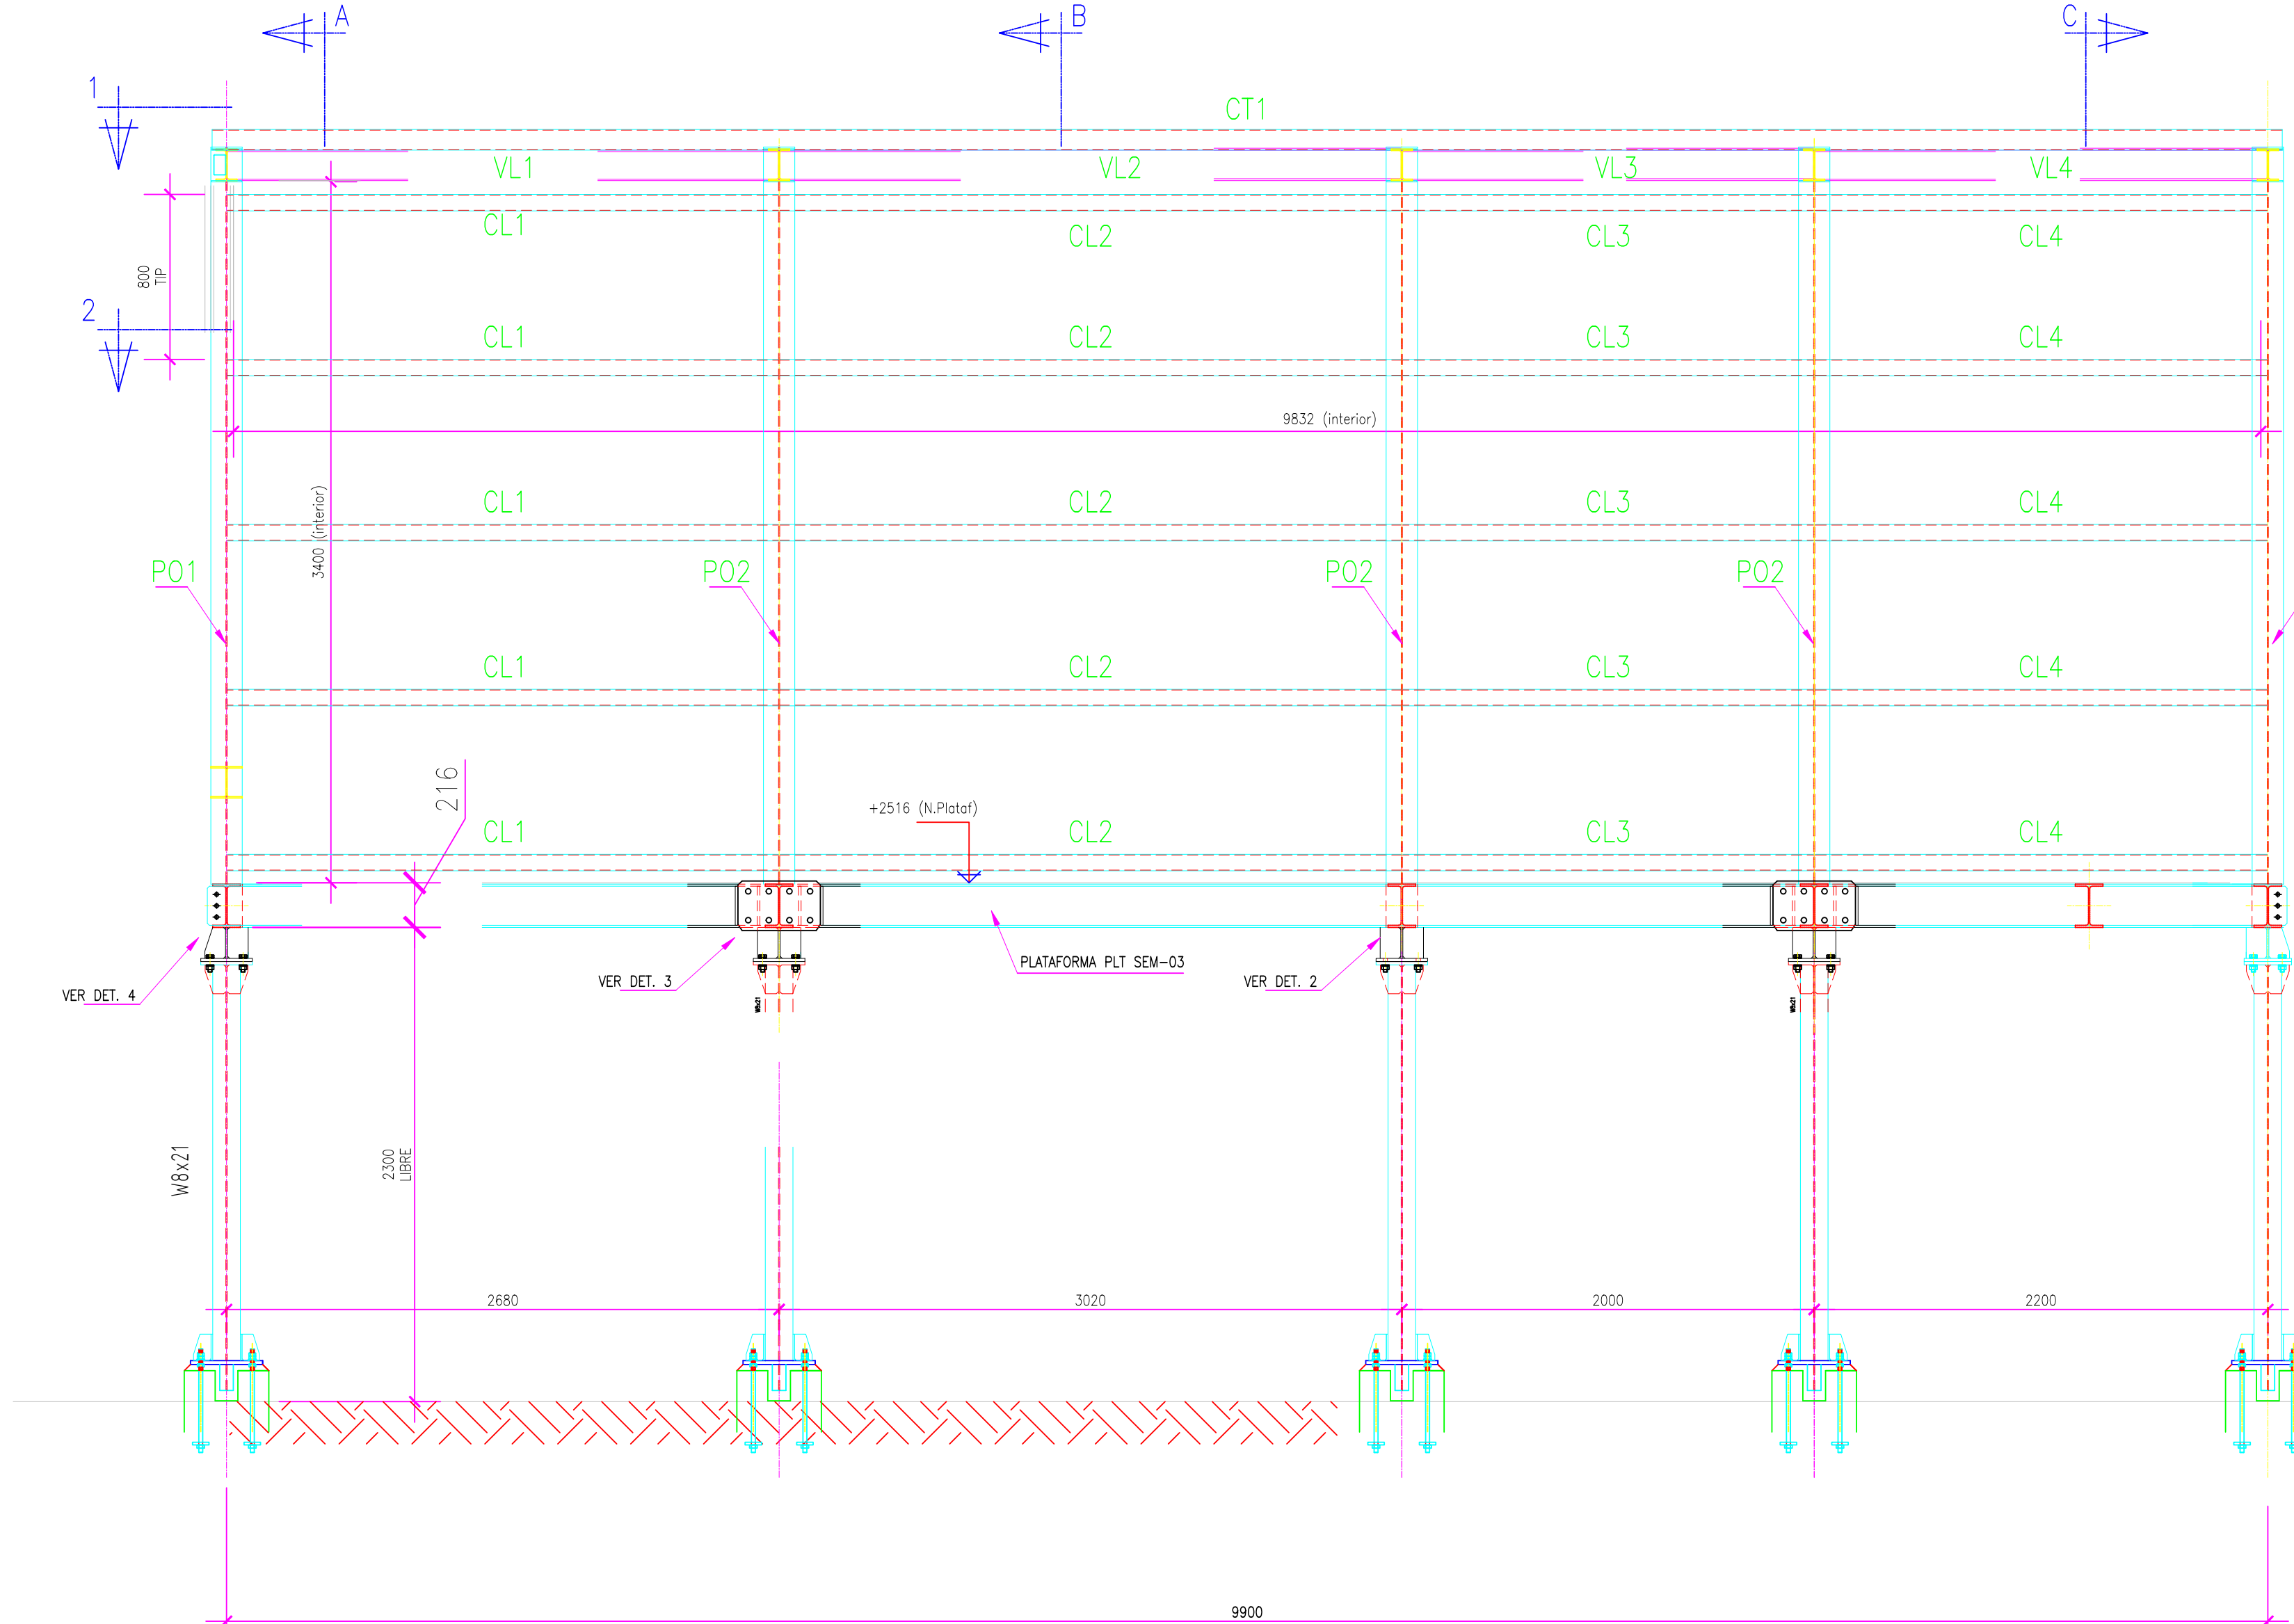

VISTA LATERAL SEM-03
ESCALA 1:25

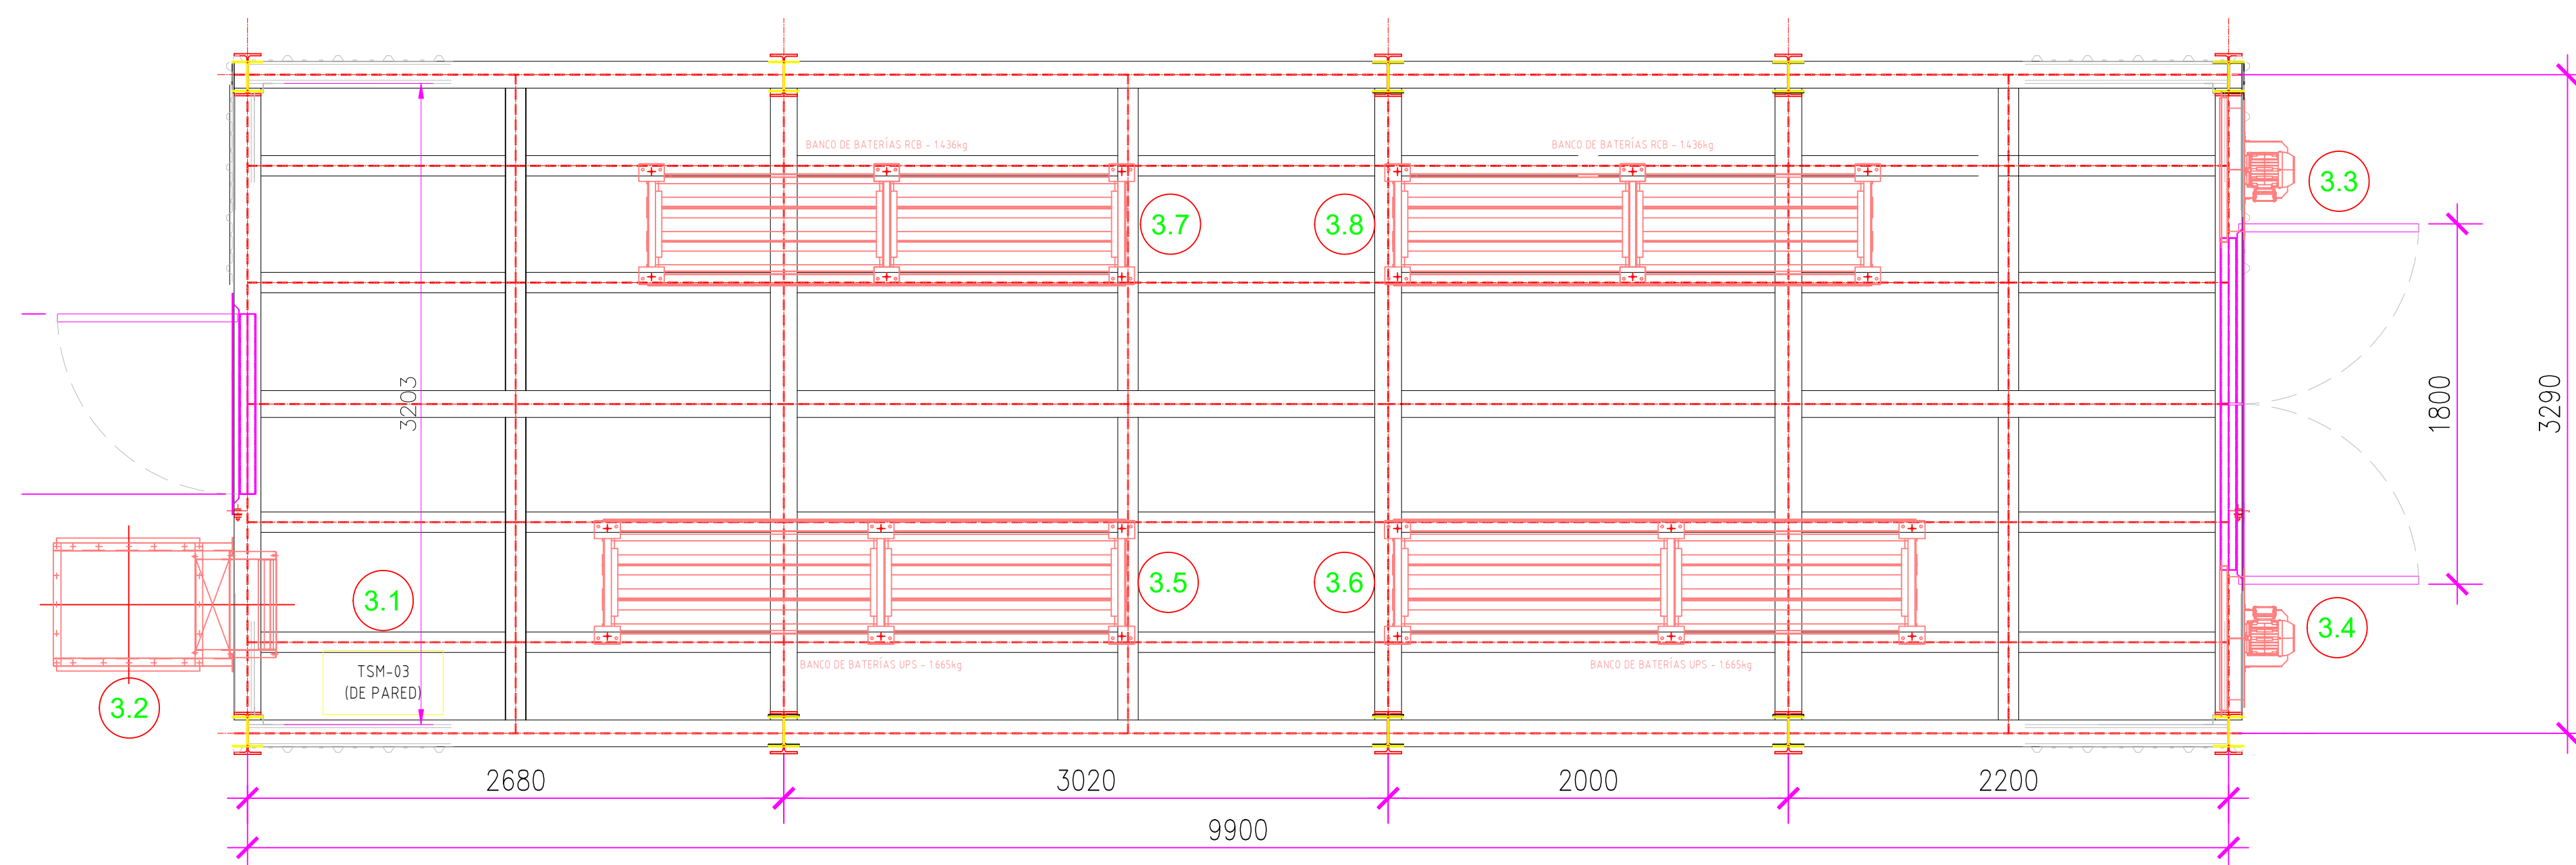

PLANTA PLATAFORMA PLT SEM-03
ESCALA 1:25

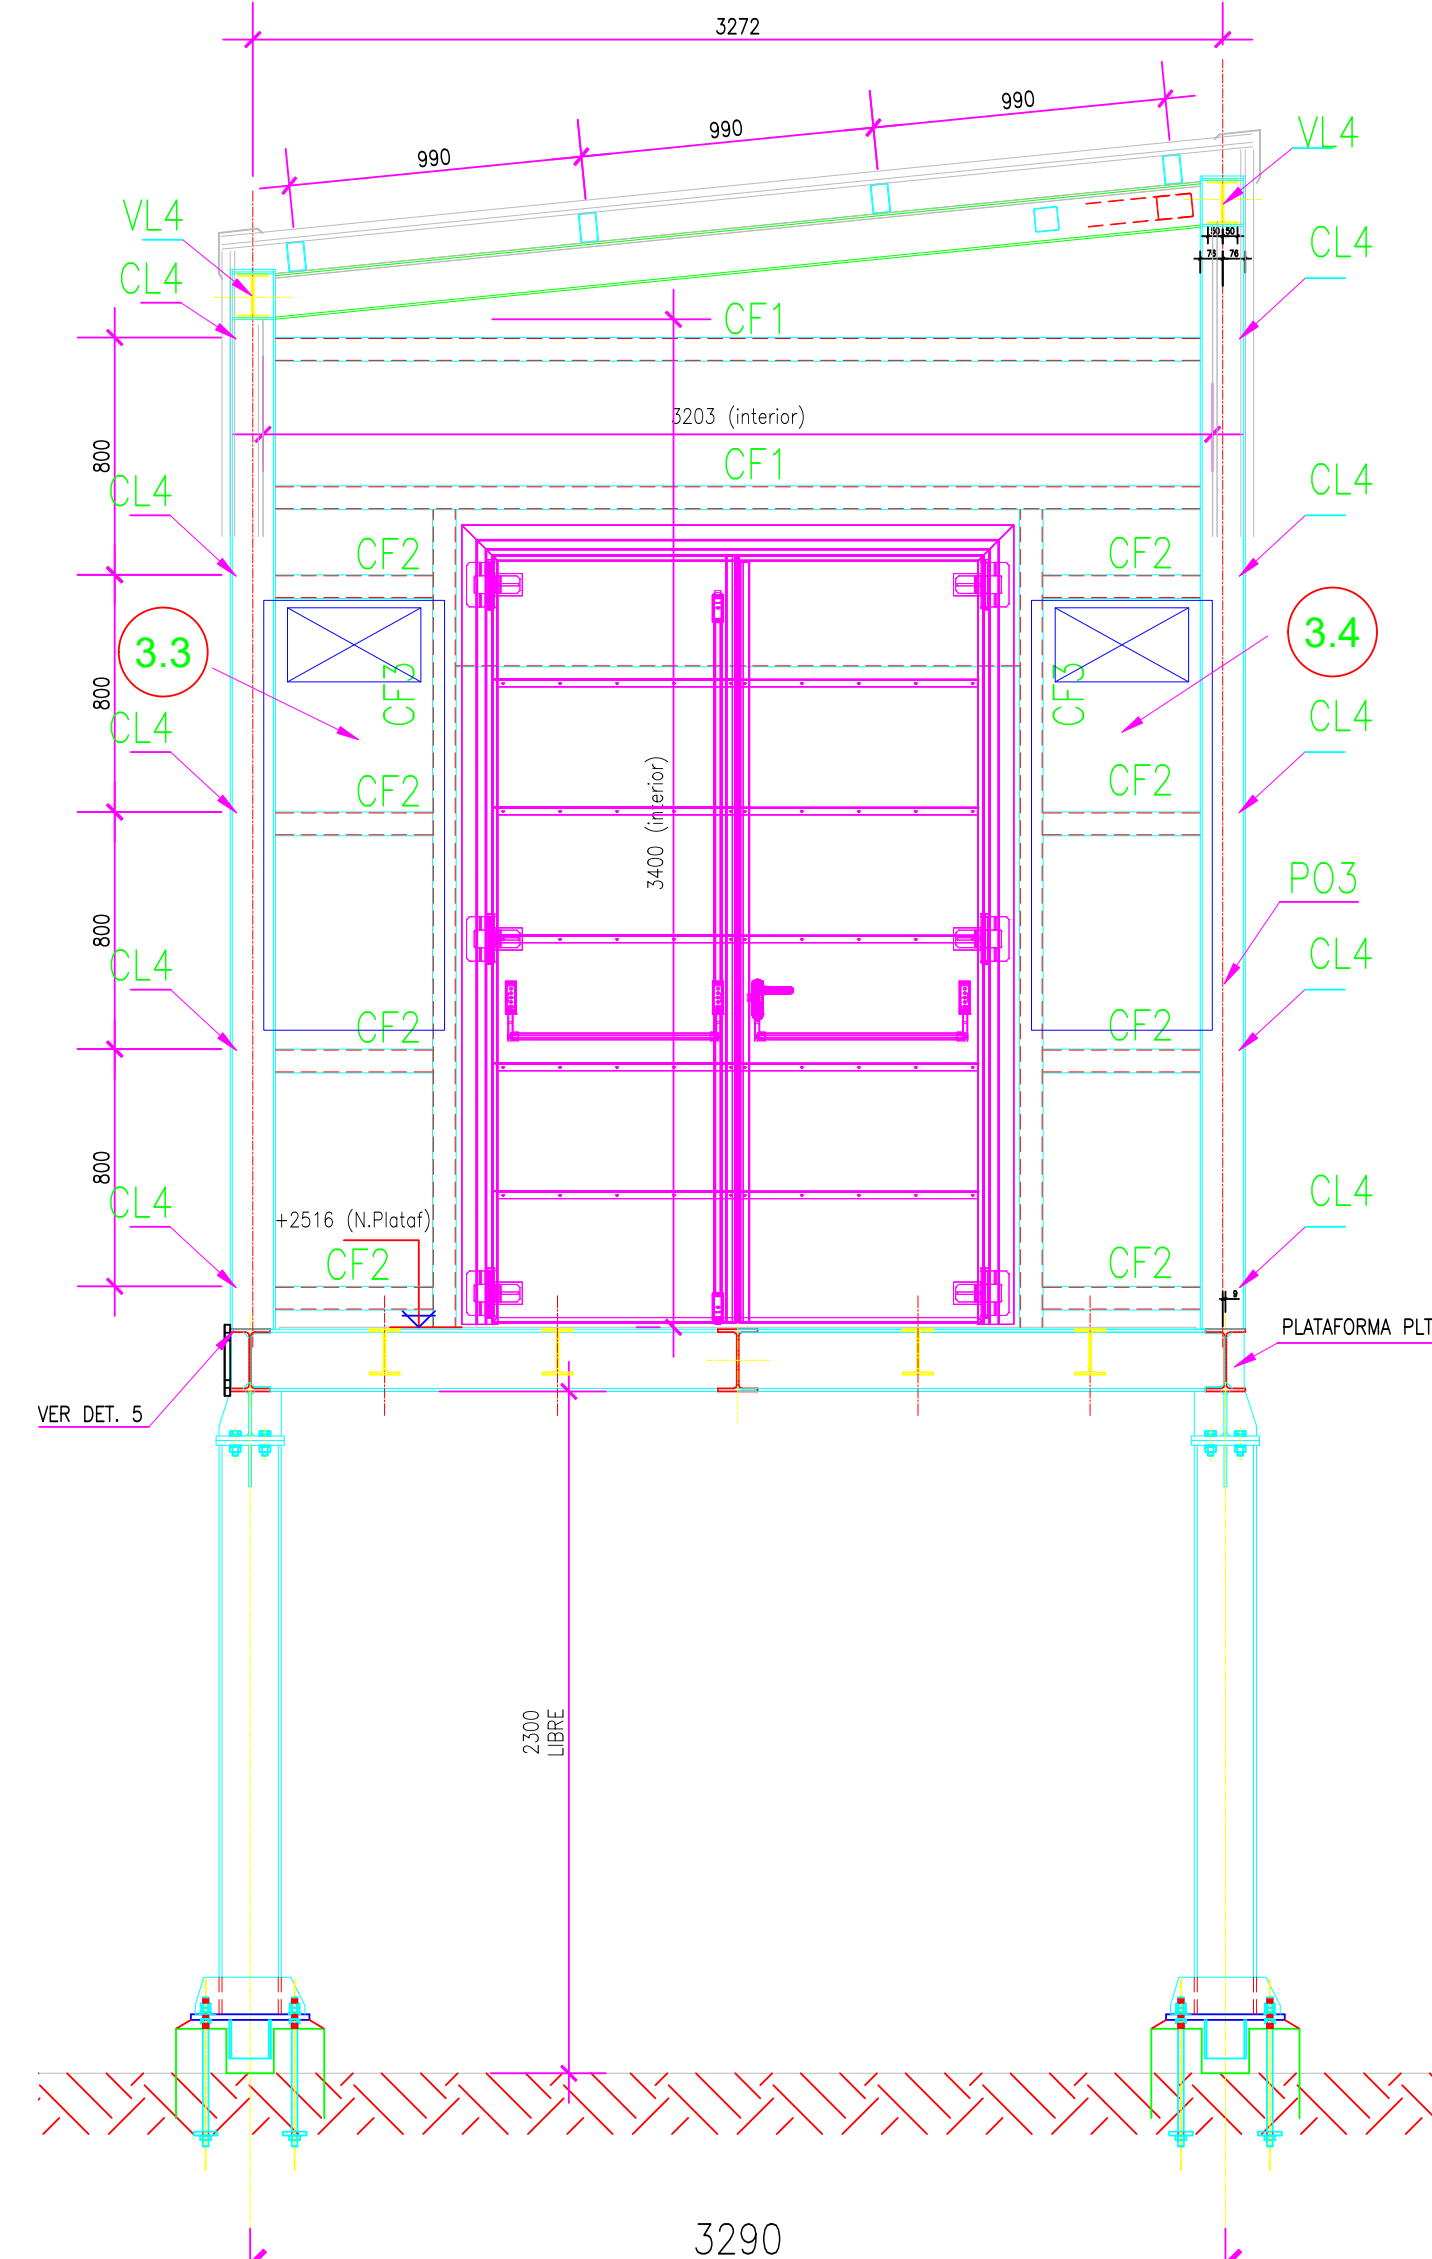

CORTE C-C SEM-03
ESCALA 1:25


NOTAS:

- MEDIDAS EN mm
- CALIDAD PERFILES LAMINADOS W: ACERO F-36 o ASTM A-572 Gr50
- CALIDAD PERFILES LAMINADOS, CHAPAS y PLANCHUELAS: ACERO F-24
- CALIDAD BULONES ASTM A-325
- TODAS LAS SOLDADURAS SE REALIZARAN S/NORMA A.W.S. D1.1-96 Y SEGUN LA ESPECIFICACION DE PROCEDIMIENTO.
- LAS COLUMNAS DE SOPORTE Y LAS FUNDACIONES INDICADAS SON MERAMENTE ILUSTRATIVAS, ESTAN FUERA DEL ALCANCEL DEL PROYECTO.

DOCUMENTOS DE REFERENCIA

- TE-631-104728-LY-C-1701 - LAYOUT GENERAL DE IMPLANTACIÓN SALAS (TAG: SEM-01 / SEM-02 / SEM-03)
- TE-631-104728-MC-C-1701 - MEMORIA DE CÁLCULOS SALAS SEM-01/02/03

0	15/12/2025	EMISIÓN PARA APROBACIÓN	AMB	RMP	JJA
REV.	FECHA	DESCRIPCIÓN	ELABORO	REVISO	APROBO
tgs		DIRECCIÓN DE OPERACIONES GERENCIA			
LUGAR: NEUQUÉN - PLANTA TRATAYÉN		TÍTULO: PLANO DE ESTRUCTURAS METÁLICAS MÓDULO N°3 (TAG: SEM-03)			
OBRA: SALAS ELÉCTRICAS PLANTA ESTABILIZADORA CONDENSADOS SLUG CATCHER - NGL ETAPA TEMPORARIA					
ESPACIO CONTRATISTA		FECHA: 15/12/25	OBRA N°: 104.728	ESCALA: INDICADAS	HOJA: 1 de 5
N° Doc. Ingeniería:		DOCUMENTO: TE-631-104728-PL-C-1703		REVISIÓN: 0	

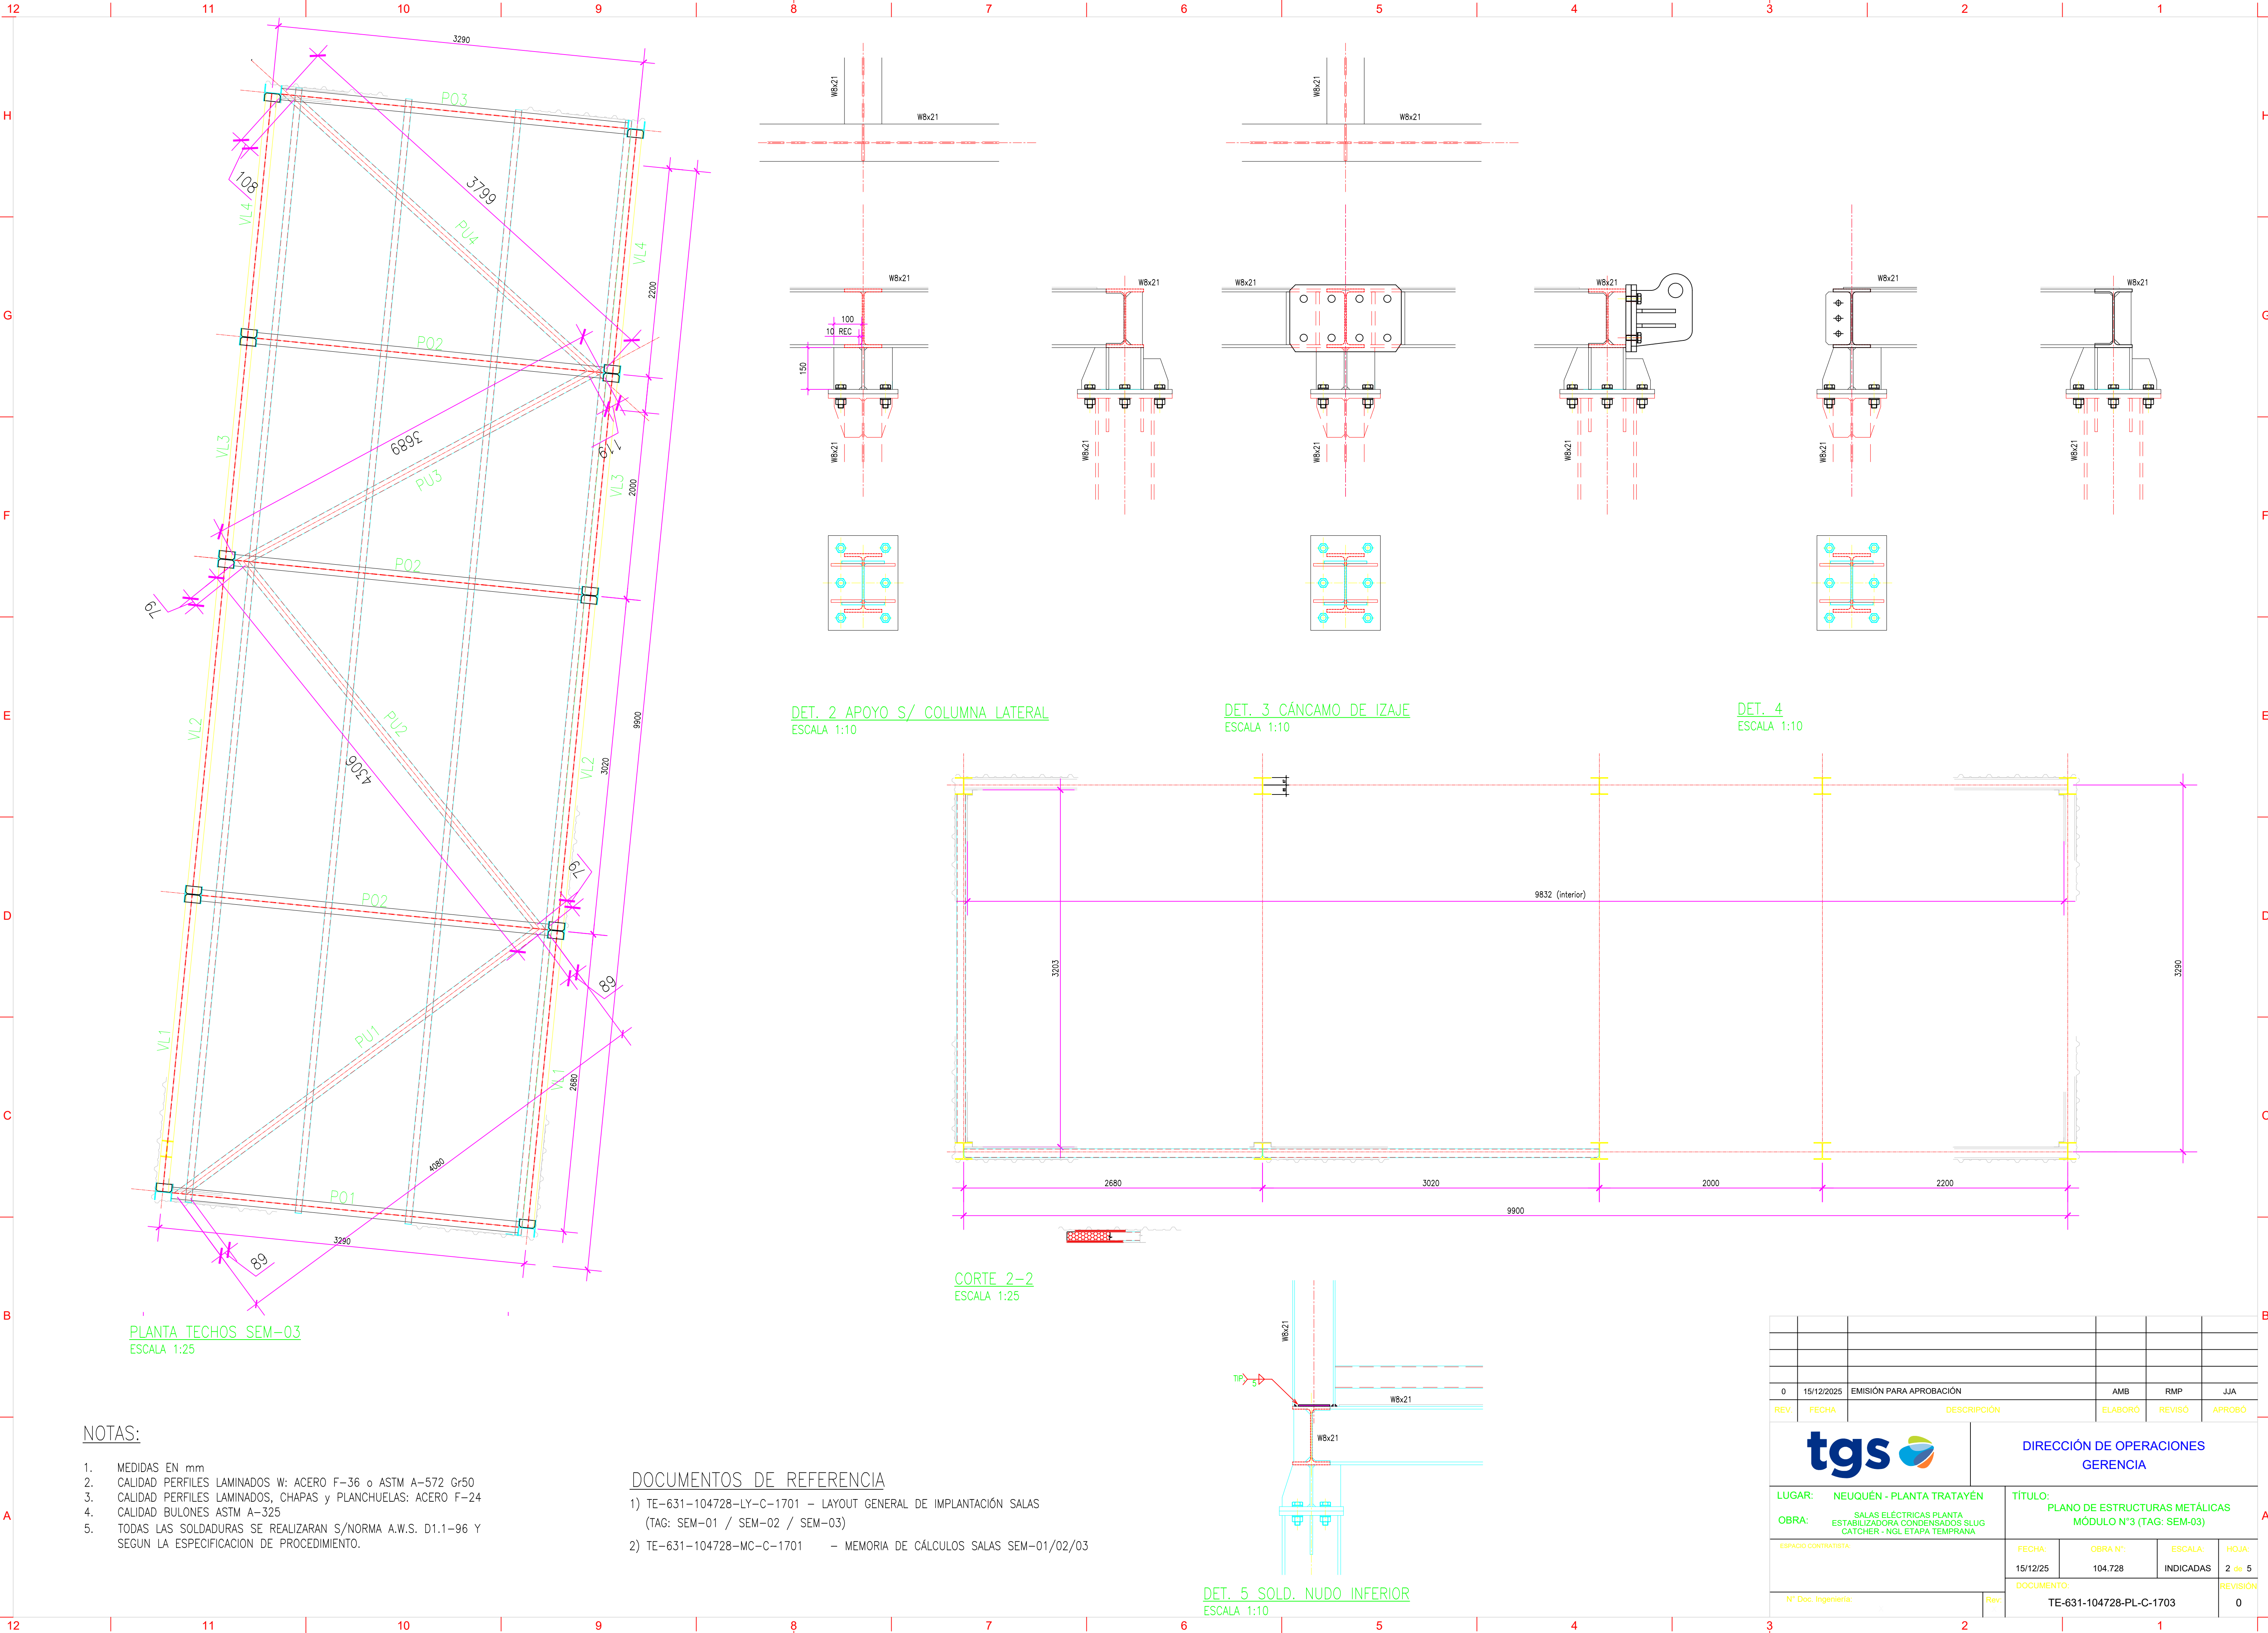

PLANTA TECHOS SEM-03
ESCALA 1:25


NOTAS:

- MEDIDAS EN mm
- CALIDAD PERFILES LAMINADOS W: ACERO F-36 o ASTM A-572 Gr50
- CALIDAD PERFILES LAMINADOS, CHAPAS y PLANCHUELAS: ACERO F-24
- CALIDAD BULONES ASTM A-325
- TODAS LAS SOLDADURAS SE REALIZARAN S/NORMA A.W.S. D1.1-96 Y SEGUN LA ESPECIFICACION DE PROCEDIMIENTO.

DOCUMENTOS DE REFERENCIA

- TE-631-104728-LY-C-1701 - LAYOUT GENERAL DE IMPLANTACIÓN SALAS
(TAG: SEM-01 / SEM-02 / SEM-03)
- TE-631-104728-MC-C-1701 - MEMORIA DE CÁLCULOS SALAS SEM-01/02/03

0	15/12/2025	EMISIÓN PARA APROBACIÓN	AMB	RMP	JJA
REV.	FECHA	DESCRIPCIÓN	ELABORÓ	REVISÓ	APROBÓ
tgs			DIRECCIÓN DE OPERACIONES GERENCIA		
LUGAR: NEUQUÉN - PLANTA TRATAYÉN			TÍTULO: PLANO DE ESTRUCTURAS METÁLICAS MÓDULO N°3 (TAG: SEM-03)		
OBRA: SALAS ELÉCTRICAS PLANTA ESTABILIZADORA CONDENSADOS SLUG CATCHER - NGL ETAPA TEMPRANA					
ESPACIO CONTRATISTA			FECHA: 15/12/25	OBRA N°: 104.728	ESCALA: INDICADAS
N° Doc. Ingeniería:			DOCUMENTO: TE-631-104728-PL-C-1703		HOJA: 2 de 5
Rev:					REVISIÓN 0

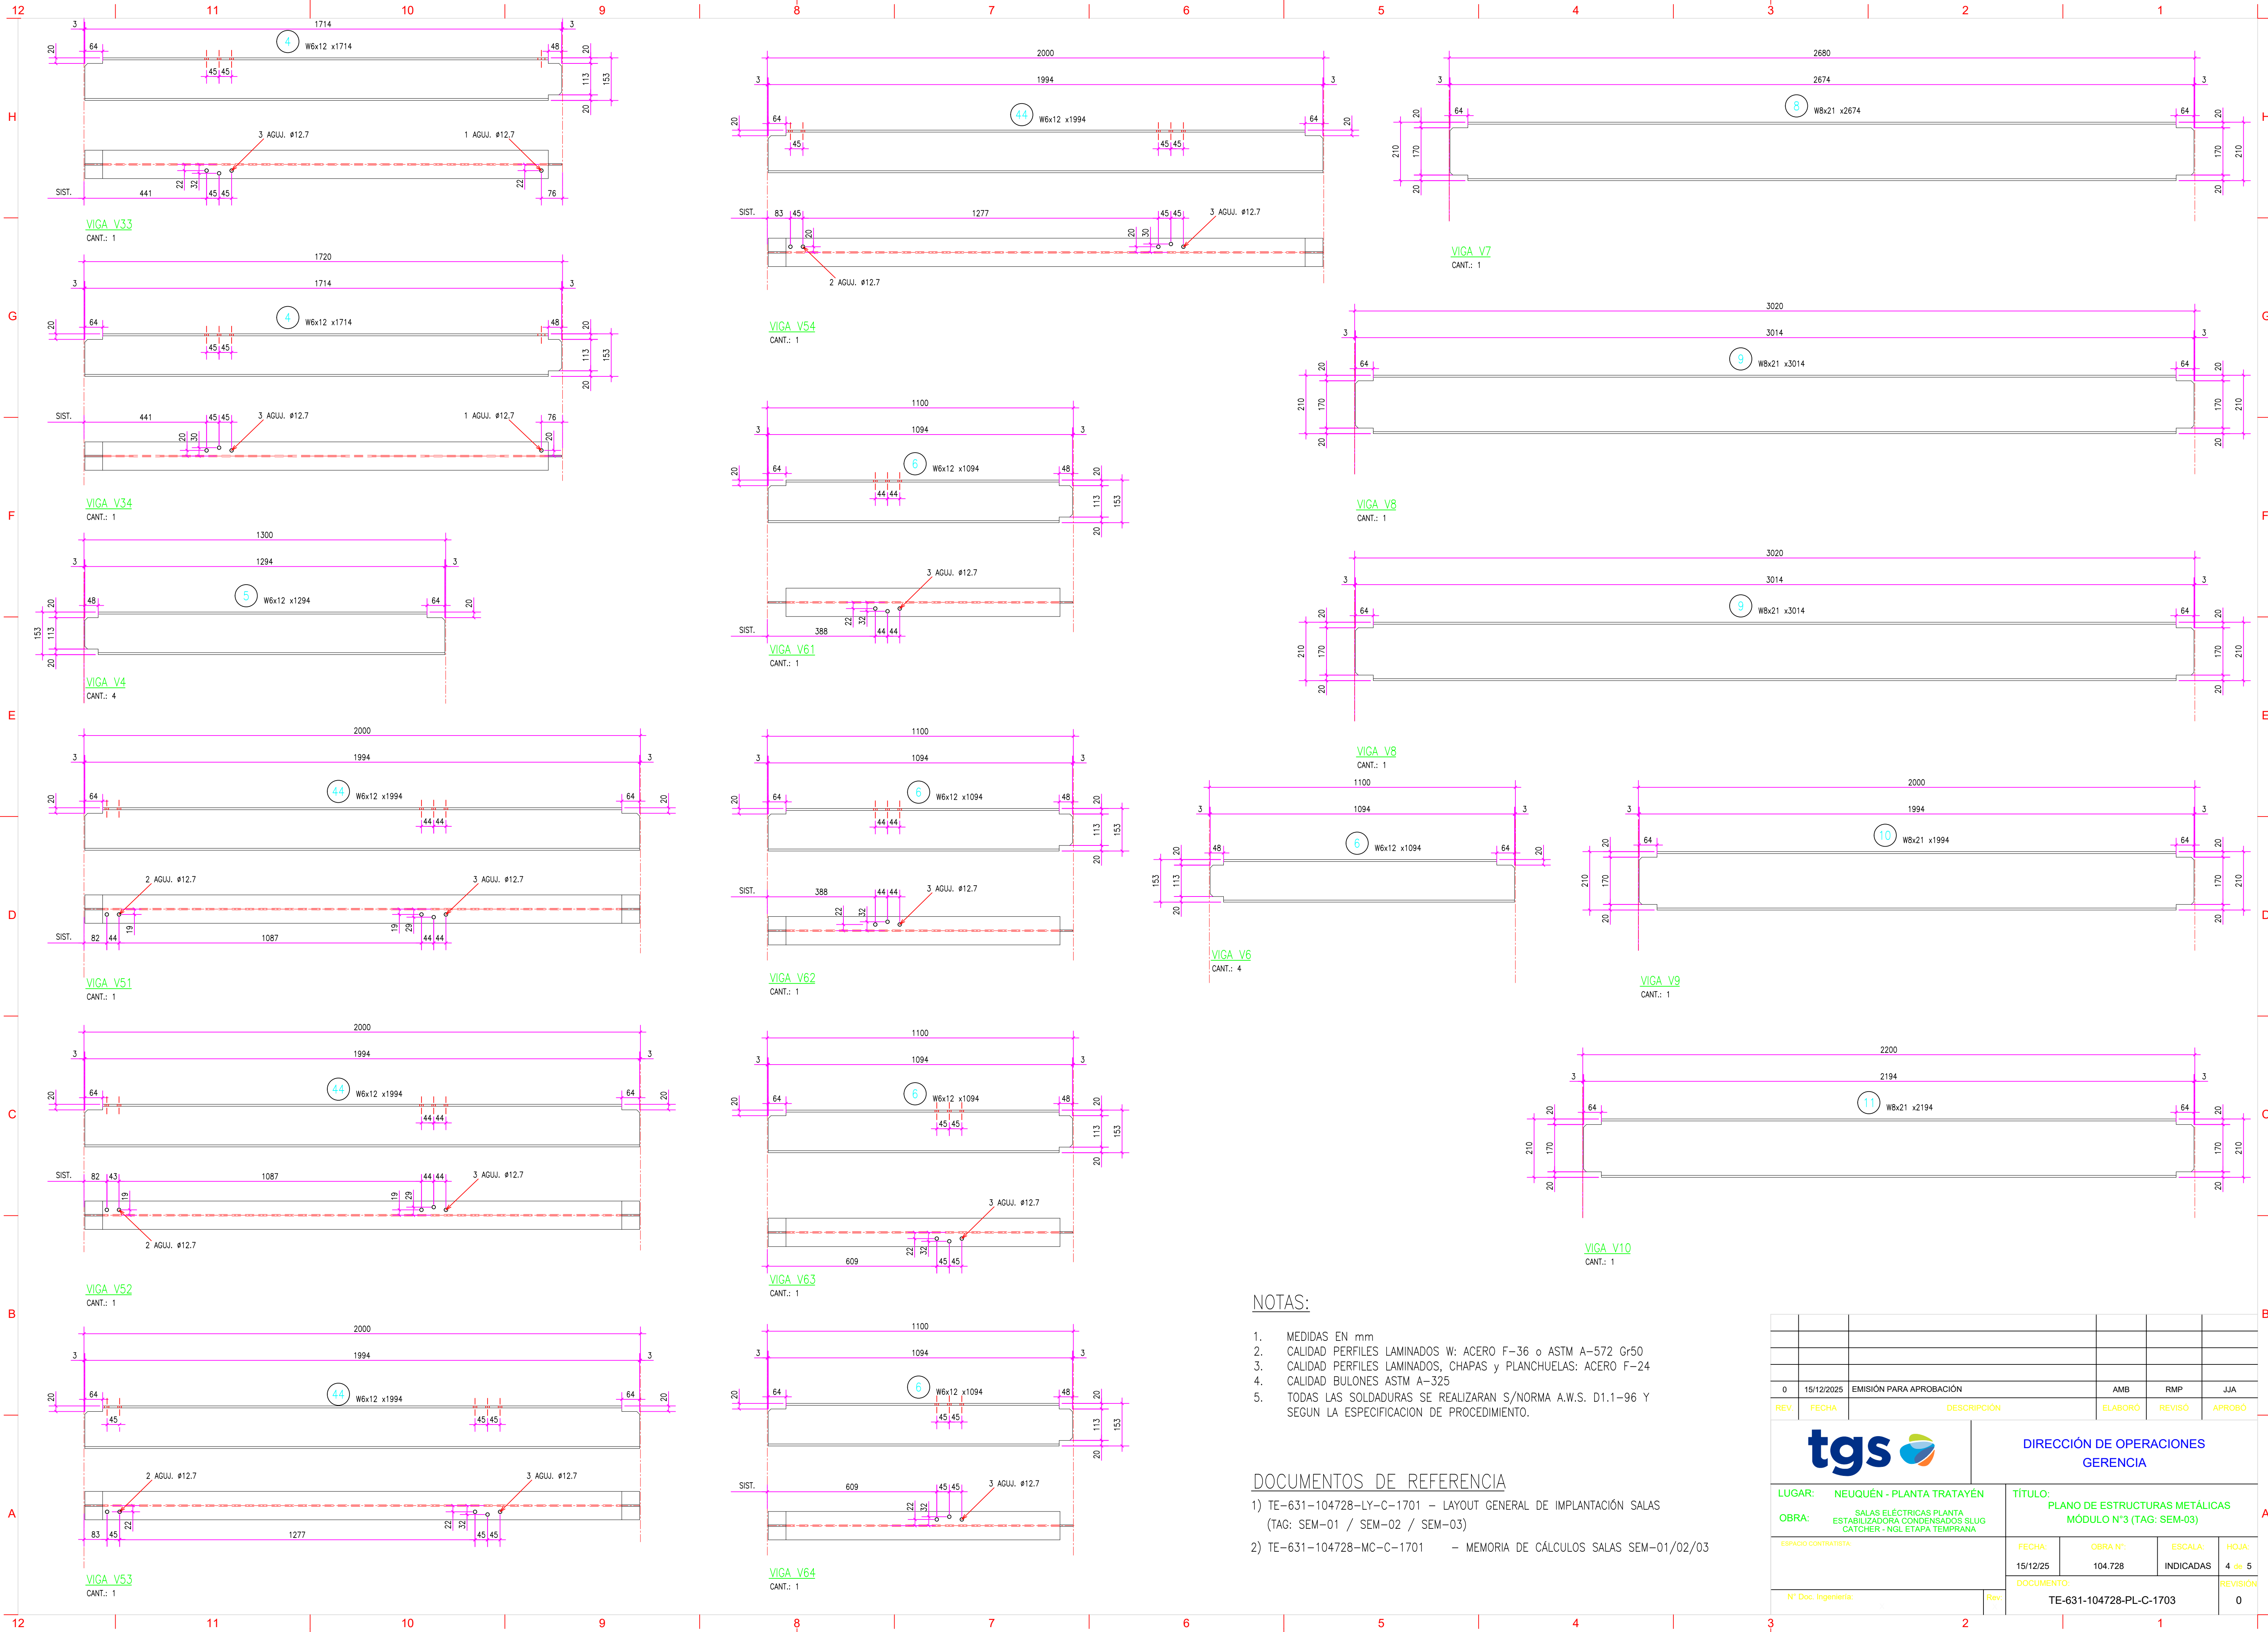






NOTAS:

1. MEDIDAS EN mm
2. CALIDAD PERFILES LAMINADOS W: ACERO F-36 o ASTM A-572 Gr50
3. CALIDAD PERFILES LAMINADOS, CHAPAS y PLANCHUELAS: ACERO F-24
4. CALIDAD BULONES ASTM A-325
5. TODAS LAS SOLDADURAS SE REALIZARAN S/NORMA A.W.S. D1.1-96 Y SEGUN LA ESPECIFICACION DE PROCEDIMIENTO.

DOCUMENTOS DE REFERENCIA


- 1) TE-631-104728-LY-C-1701 - LAYOUT GENERAL DE IMPLANTACIÓN SALAS (TAG: SEM-01 / SEM-02 / SEM-03)
- 2) TE-631-104728-MC-C-1701 - MEMORIA DE CÁLCULOS SALAS SEM-01/02/03

0	15/12/2025	EMISIÓN PARA APROBACIÓN		AMB	RMP
REV.	FECHA	DESCRIPCIÓN	ELABORO	REVISO	APROBO
tgs			DIRECCIÓN DE OPERACIONES GERENCIA		
LUGAR: NEUQUÉN - PLANTA TRATAYÉN			TÍTULO: PLANO DE ESTRUCTURAS METÁLICAS MÓDULO N°3 (TAG: SEM-03)		
OBRA: SALAS ELÉCTRICAS PLANTA ESTABILIZADORA CONDENSADOS SLUG CATCHER - NGL ETAPA TEMPRANA					
ESPACIO CONTRASTA			FECHA: 15/12/25	OBRA N°: 104.728	ESCALA: INDICADAS
N° Doc. Ingeniería:			DOCUMENTO: TE-631-104728-PL-C-1703	HOJA: 4 de 5	REVISIÓN: 0

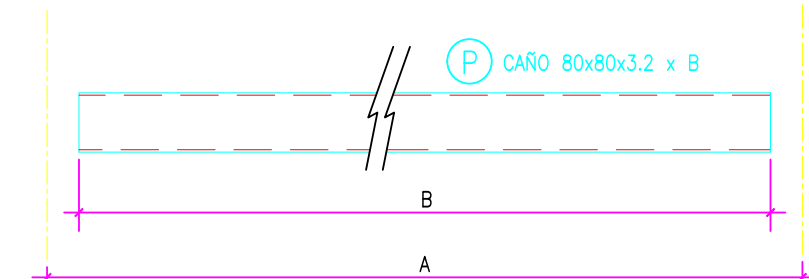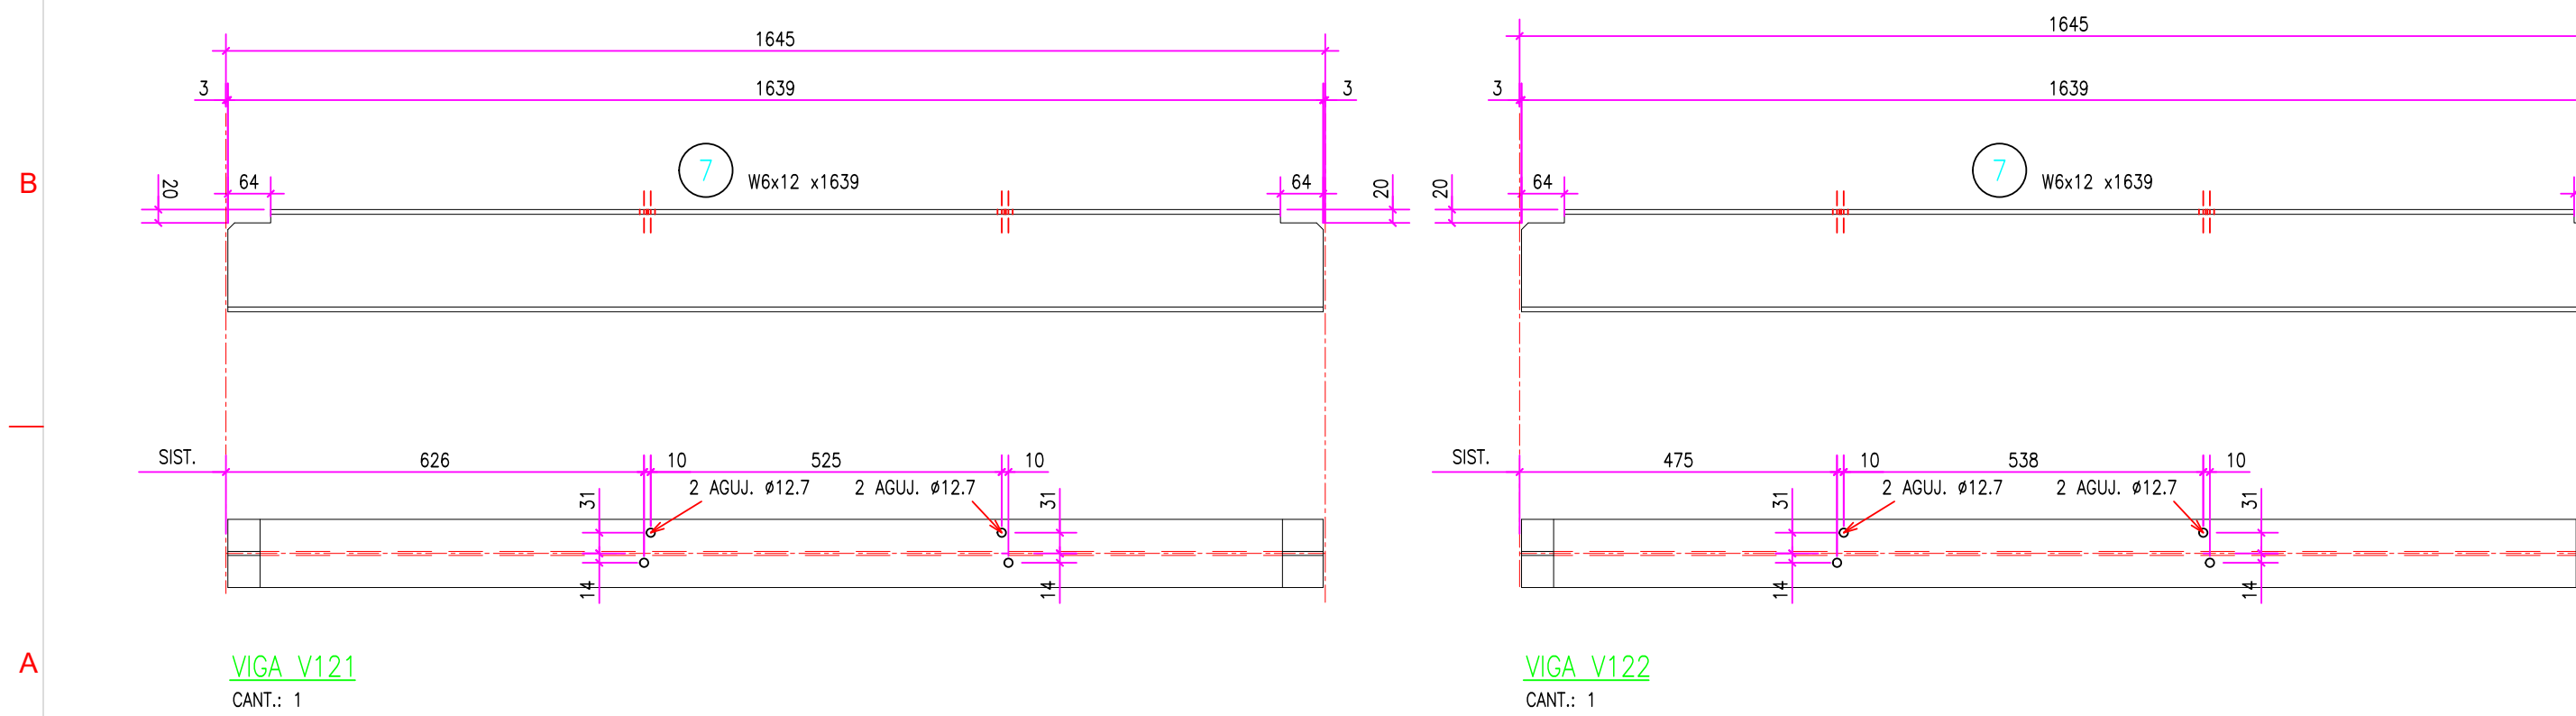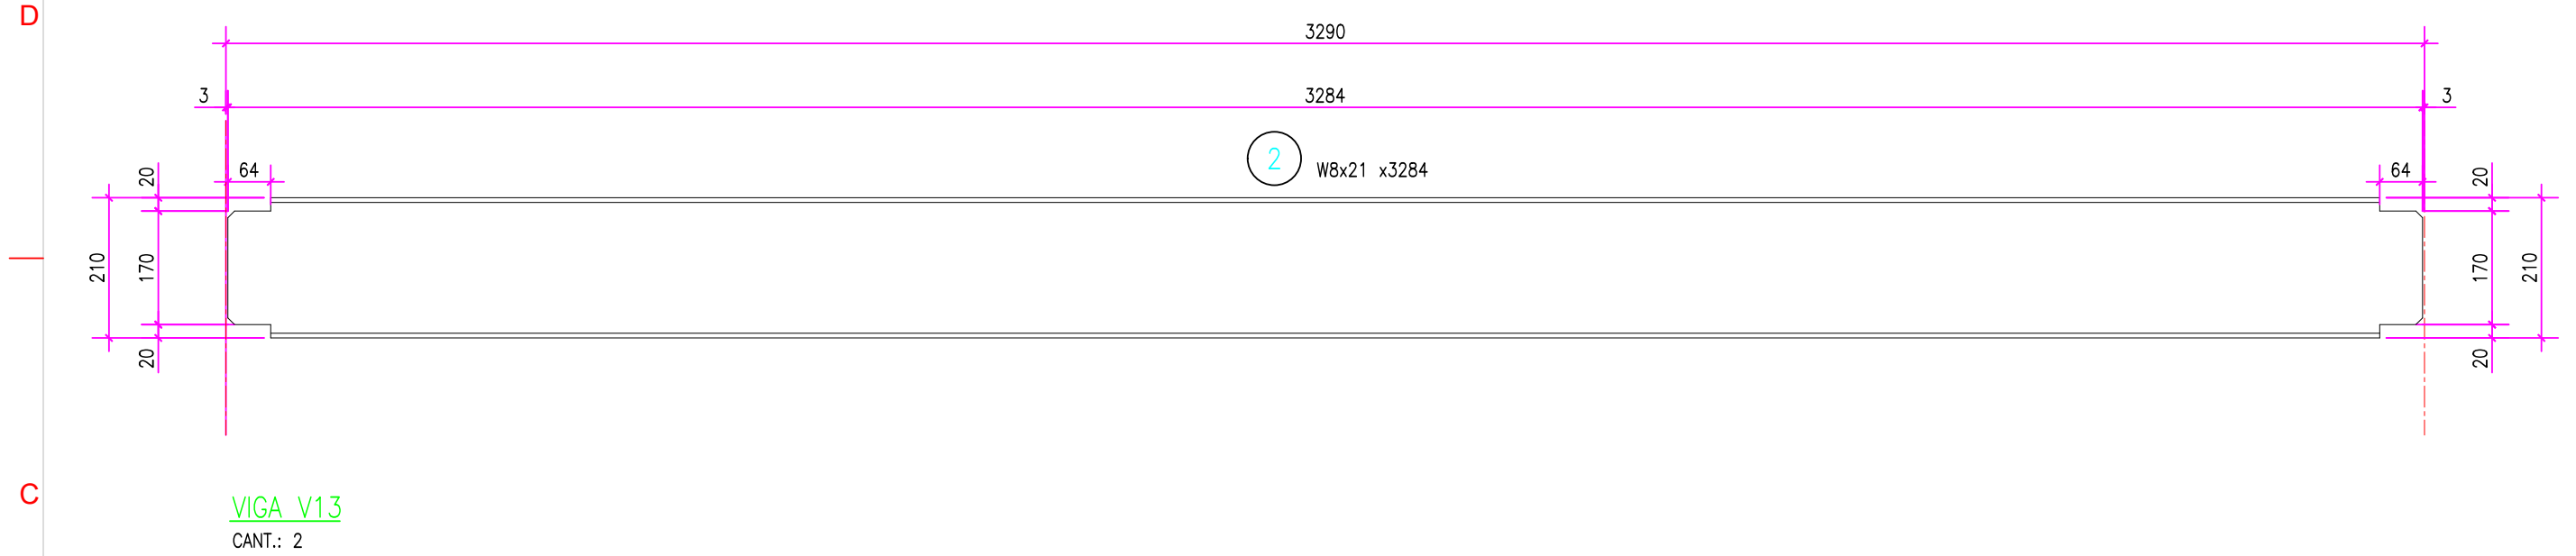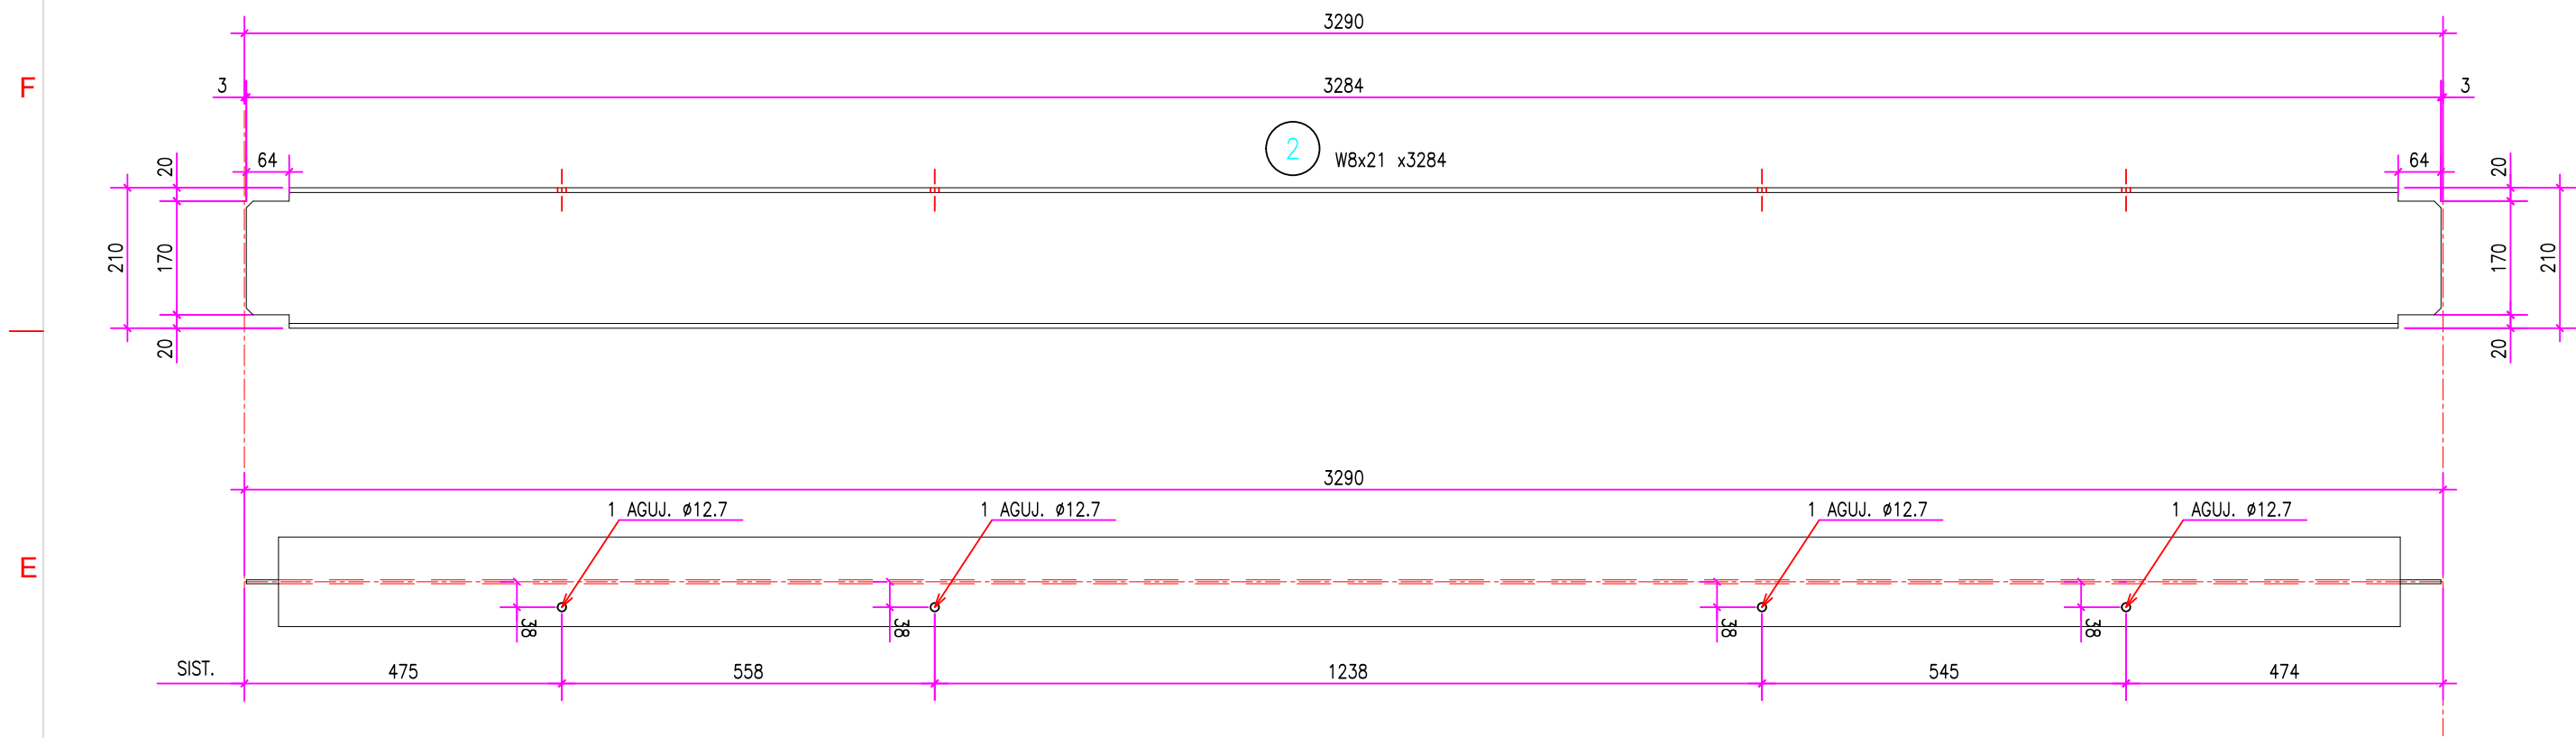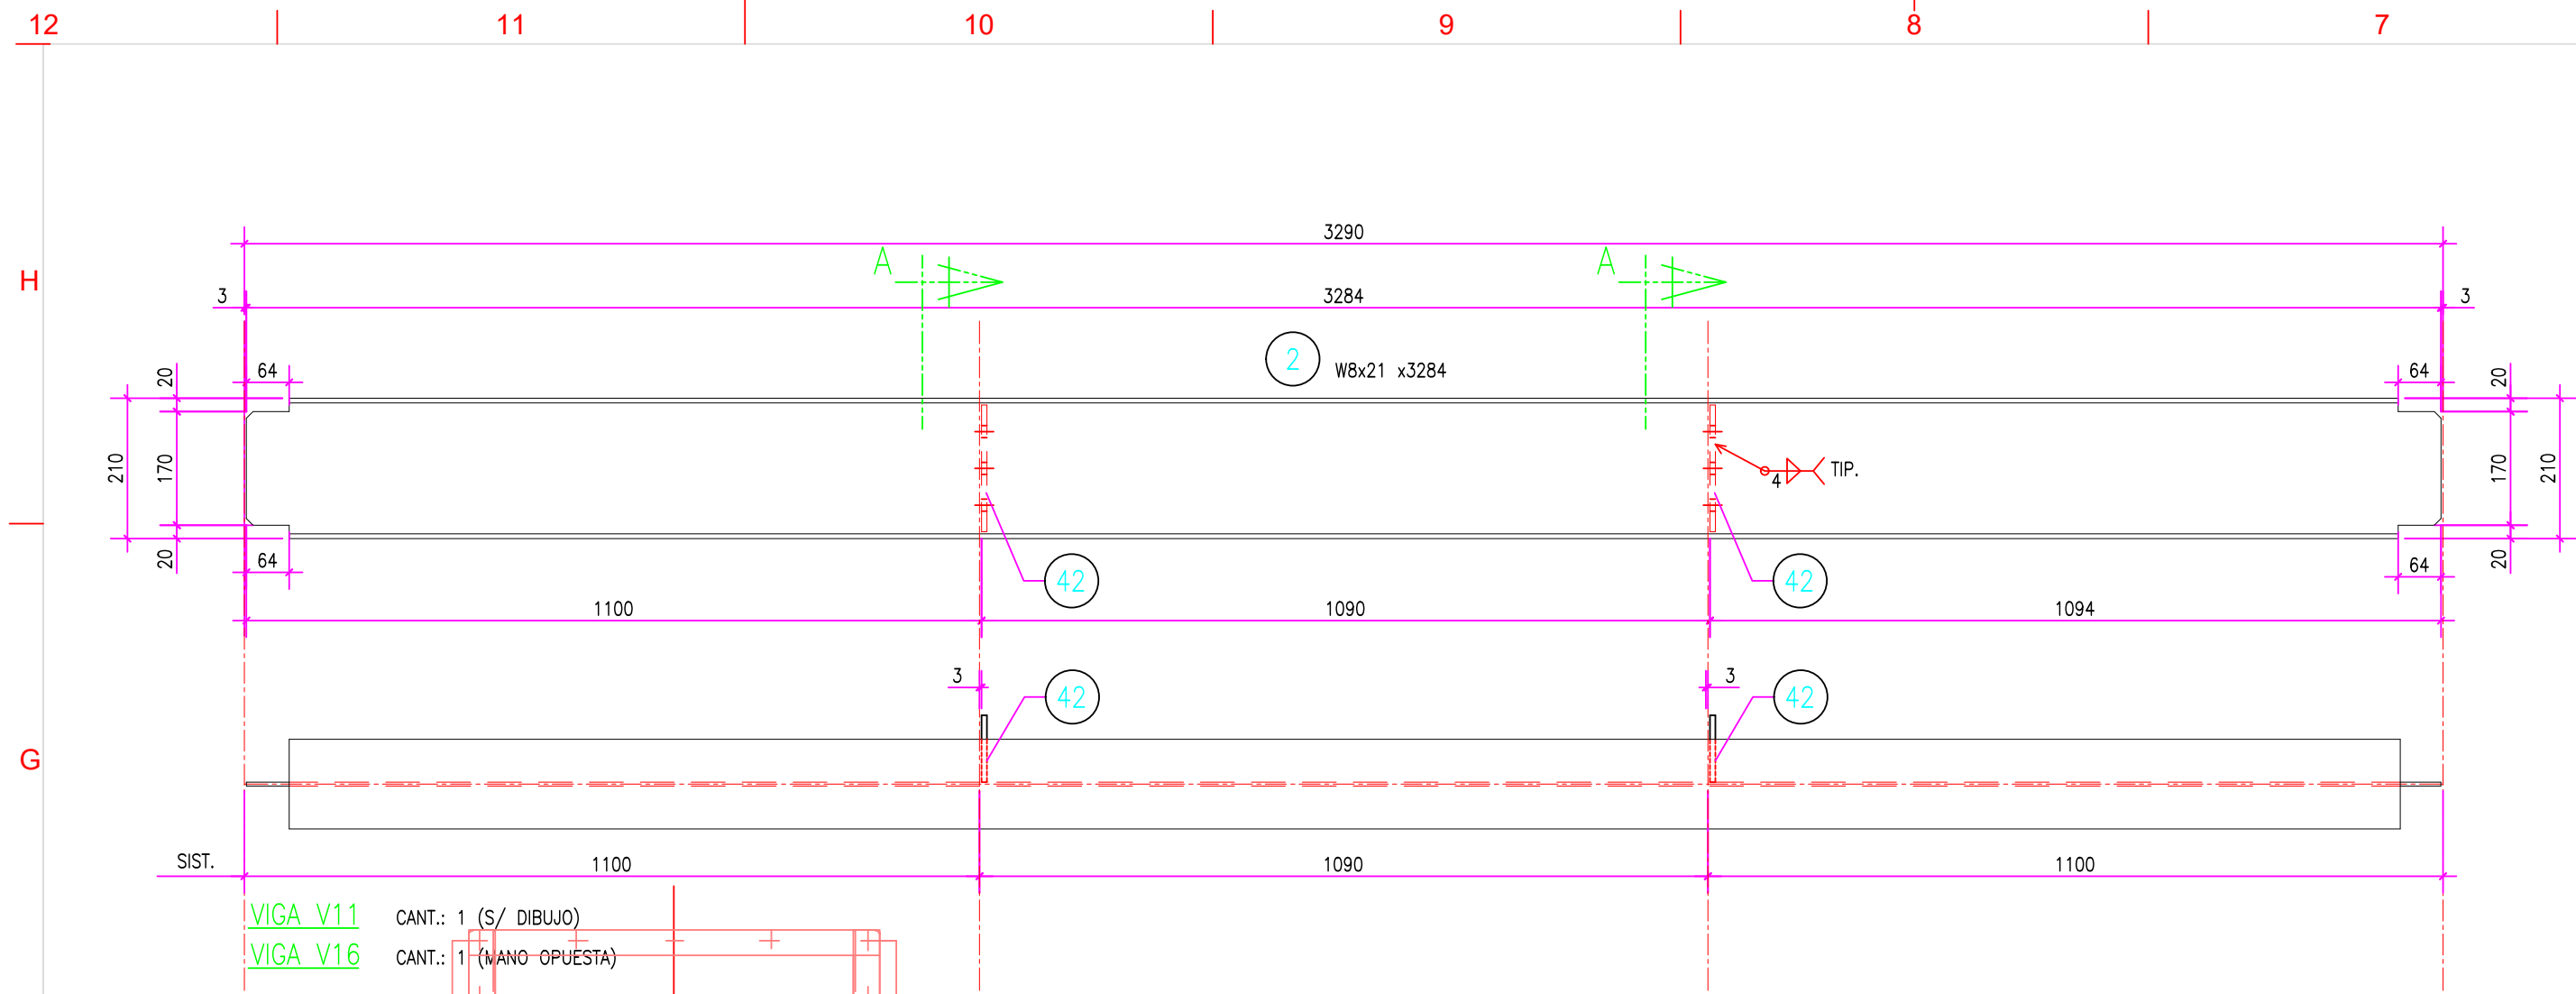


CORREA	CANT.	Pos	MAT	A	B
CF1	4	23	CAÑO 80x80x3.2	3120	
CF2	8	24	CAÑO 80x80x3.2	530	
CF3	2	25	CAÑO 80x80x3.2	2760	
CF4	6	26	CAÑO 80x80x3.2	930	
CF5	1	27	CAÑO 80x80x3.2	1100	
CF6	2	28	CAÑO 80x80x3.2	2460	

CORREAS FRONTS
ESCALA 1:10

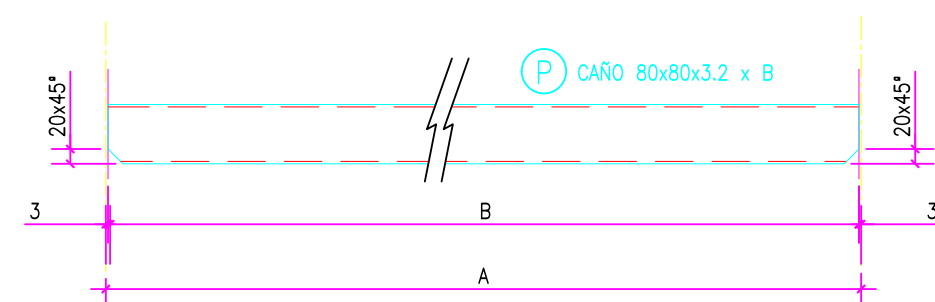


CORREA	CANT.	Pos	MAT	A	B
CL1	10	19	CAÑO 80x80x3.2	2680	2674
CL2	10	20	CAÑO 80x80x3.2	3020	3014
CL3	10	21	CAÑO 80x80x3.2	2000	1994
CL4	10	22	CAÑO 80x80x3.2	2200	2194

CORREAS LATERALES
ESCALA 1:10

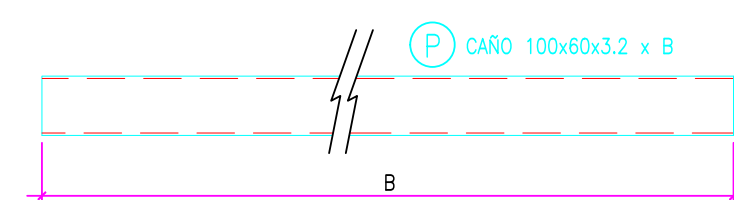


CORREA	CANT.	Pos	MAT	A	B
CT1	5	29	CAÑO 100x60x3.2		10040

CORREAS TERCHO
ESCALA 1:10

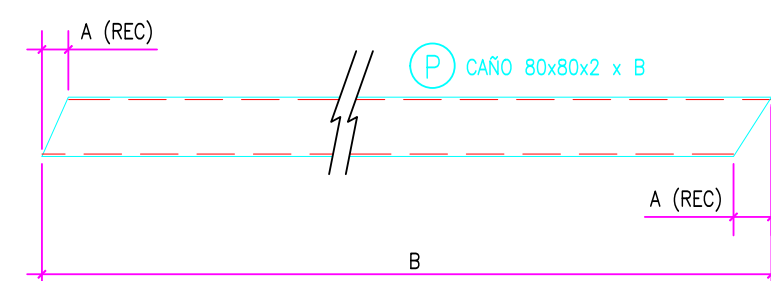


CORREA	CANT.	Pos	MAT	A	B
PU1	1	30	CAÑO 80x80x2	89	4080
PU2	1	31	CAÑO 80x80x2	79	4306
PU3	1	32	CAÑO 80x80x2	119	3689
PU4	1	33	CAÑO 80x80x2	108	3799

PUNTALES DE TECHO
ESCALA 1:10

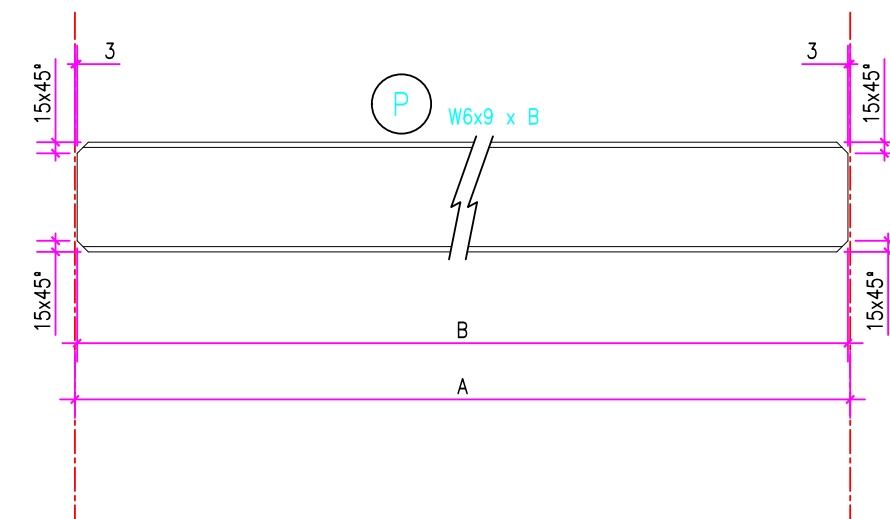


VIGA	CANT.	Pos	MAT	A	B
VL1	2	15	W6x9	2680	2674
VL2	2	16	W6x9	3020	3014
VL3	2	17	W6x9	2000	1994
VL4	2	18	W6x9	2200	2194

VIGAS LONGITUDINALES VL

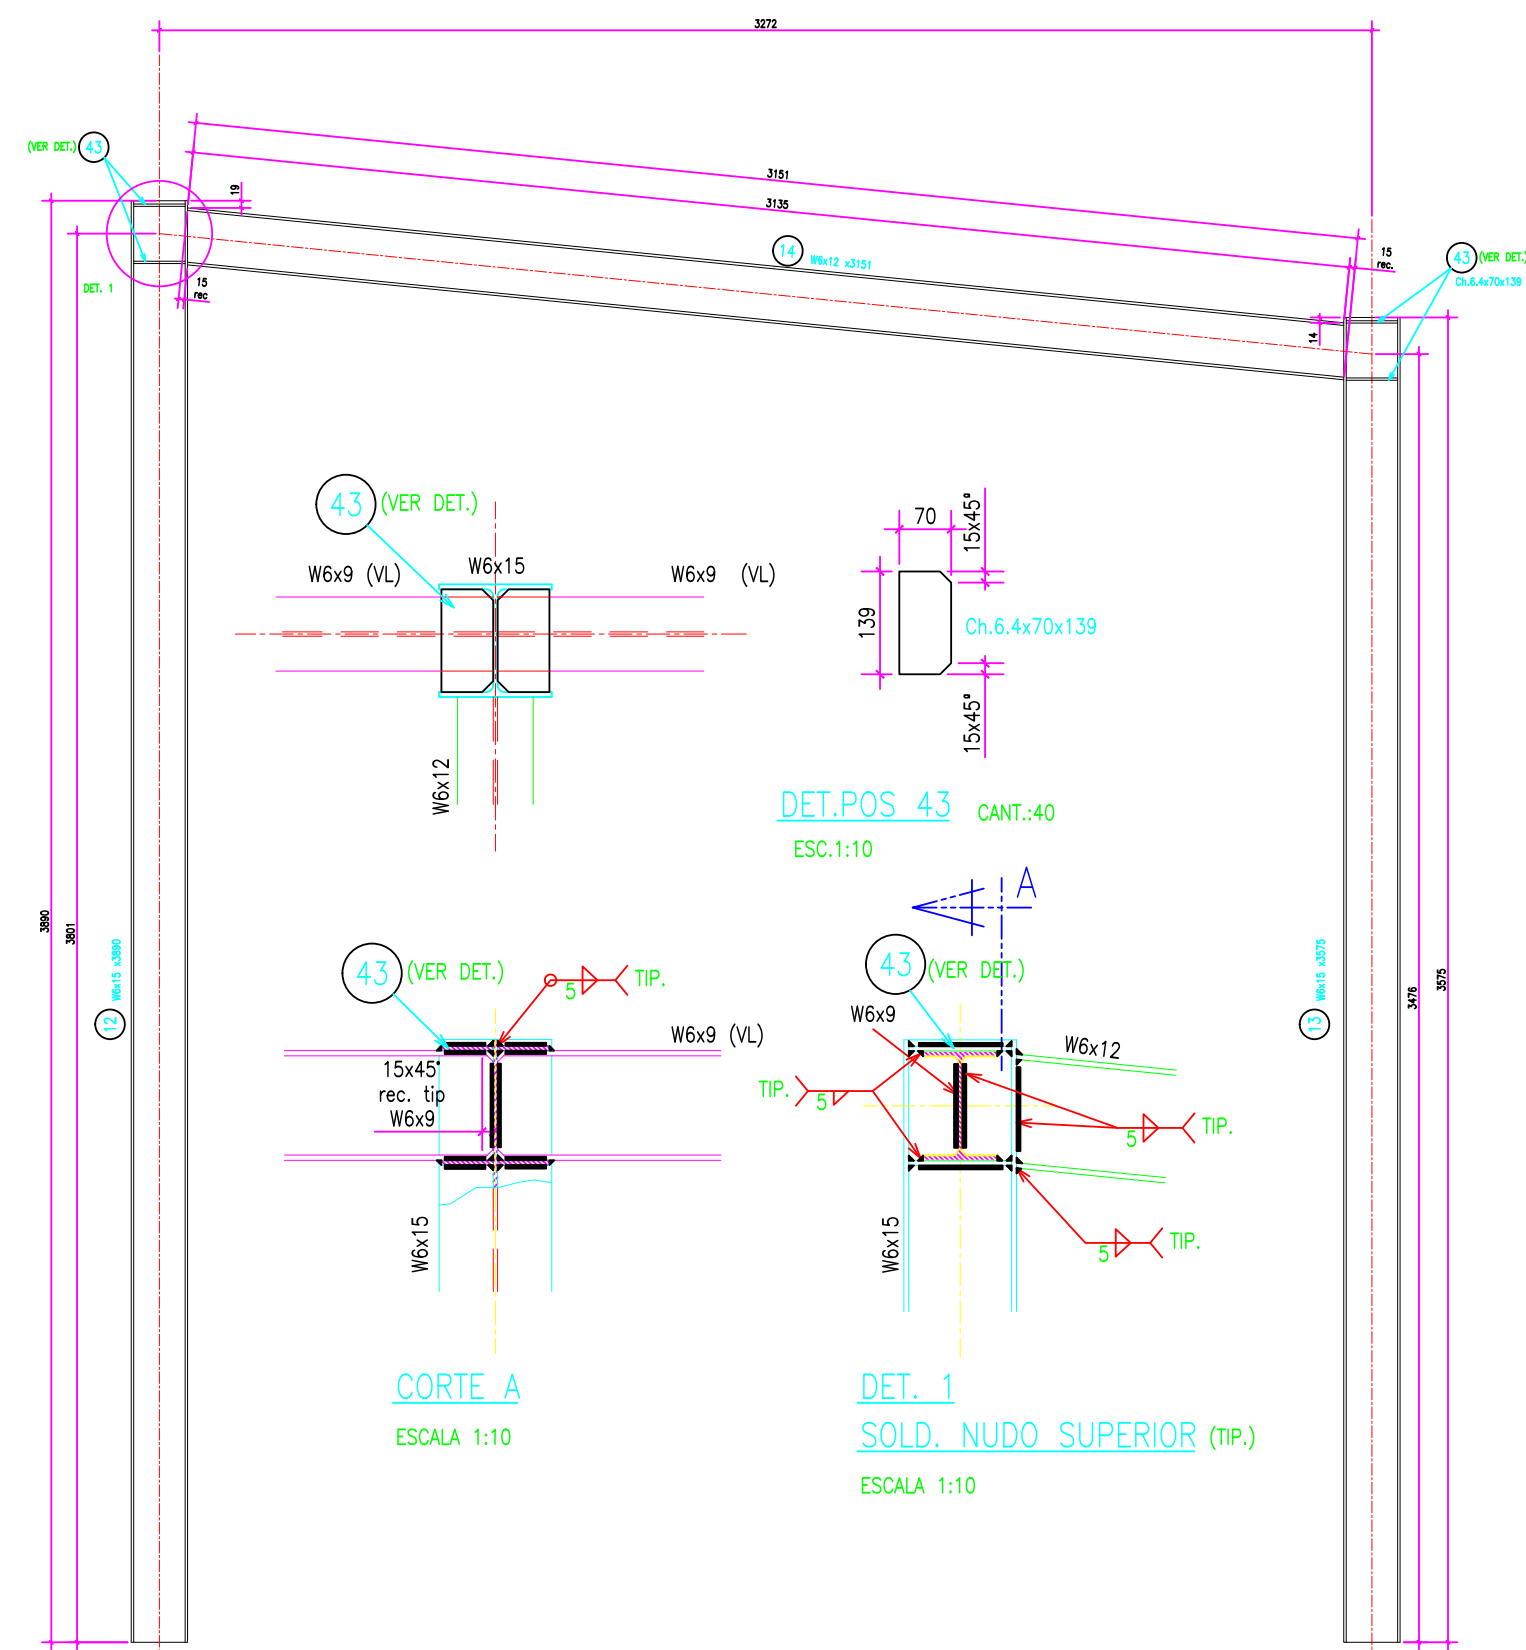

DET. POS. 43
ESC. 1:10

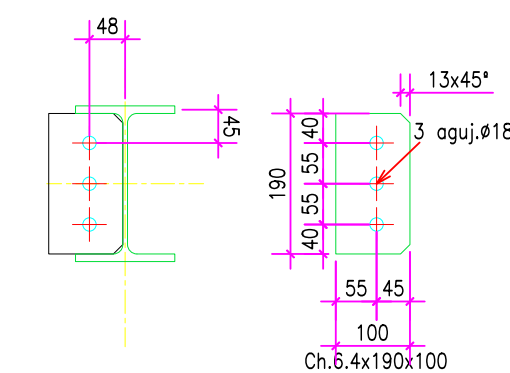

DET. POS. 42
ESC. 1:10

NOTAS:

- MEDIDAS EN mm
- CALIDAD PERFILES LAMINADOS W: ACERO F-36 o ASTM A-572 Gr50
- CALIDAD PERFILES LAMINADOS, CHAPAS y PLANCHUELAS: ACERO F-24
- CALIDAD BULONES ASTM A-325
- TODAS LAS SOLDADURAS SE REALIZARAN S/NORMA A.W.S. D1.1-96 Y SEGUN LA ESPECIFICACION DE PROCEDIMIENTO.

DOCUMENTOS DE REFERENCIA

- TE-631-104728-LY-C-1701 - LAYOUT GENERAL DE IMPLANTACIÓN SALAS (TAG: SEM-01 / SEM-02 / SEM-03)
- TE-631-104728-MC-C-1701 - MEMORIA DE CÁLCULOS SALAS SEM-01/02/03

0	15/12/2025	EMISIÓN PARA APROBACIÓN	AMB	RMP	JJA
REV.	FECHA	DESCRIPCIÓN	ELABORÓ	REVISÓ	APROBO
tgs			DIRECCIÓN DE OPERACIONES GERENCIA		
LUGAR: NEUQUÉN - PLANTA TRATAYÉN			TÍTULO: PLANO DE ESTRUCTURAS METÁLICAS MÓDULO N°3 (TAG: SEM-03)		
OBRA: SALAS ELÉCTRICAS PLANTA ESTABILIZADORA CONDENSADOS SLUG CATCHER - NGL ETAPA TEMPRANA			FECHA: 15/12/25	OBRA N°: 104.728	ESCALA: INDICADAS
N° Doc. Ingeniería:			DOCUMENTO: TE-631-104728-PL-C-1703	HOJA: 5 de 5	
Rev:			REVISIÓN		0